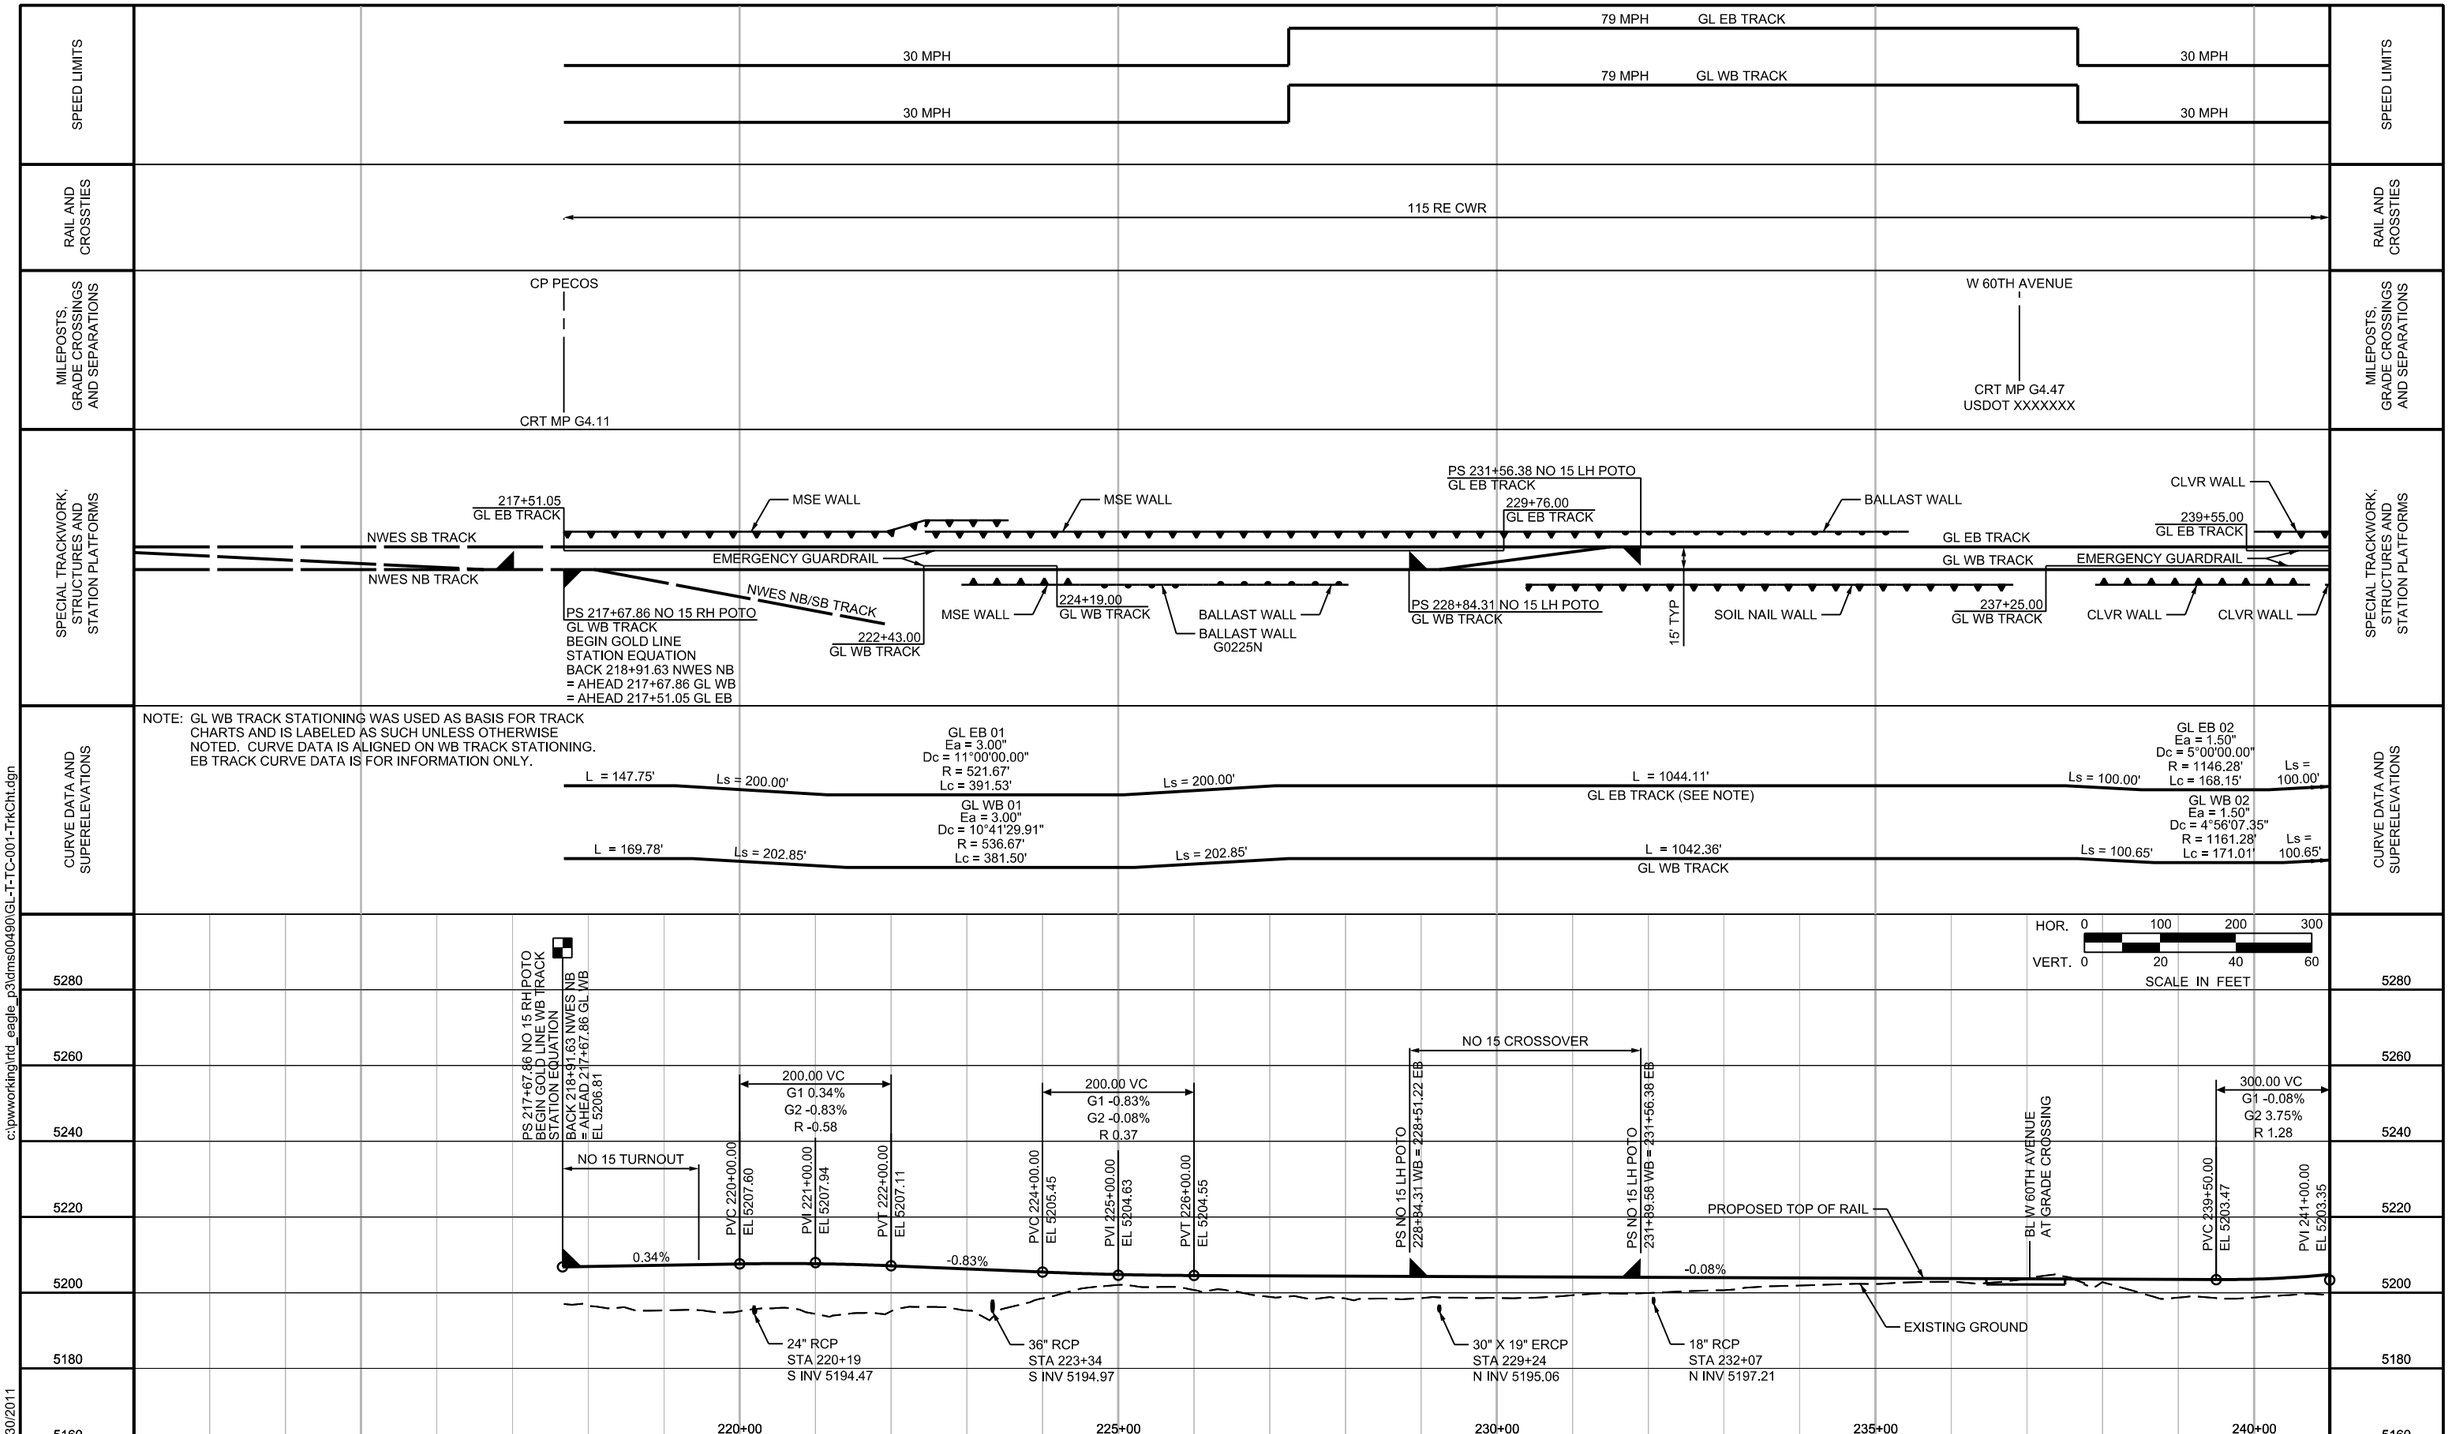

NO.	REVISIONS	BY	DATE
B	ISSUED FOR 60% SUBMITTAL, CDRL #7B-03.07, REV B	AD	06/13/11
A1	ISSUED FOR CONST REVIEW, CDRL #7B-03.07, REV A1	AD	05/23/11

DESIGNED BY: DWH/VHH DATE: 05/13/11
DRAWN BY: DWH/VHH DATE: 05/13/11
CHECKED BY: DATE:
APPROVED BY: DATE:

RTD FASTRACKS eagle P3 FLUOR HDR GLOBAL DESIGN CONSULTANTS

DENVER TRANSIT PARTNERS

GOLD LINE

TRACK CHARTS
STA 217+67.86 TO STA 241+00

SHEET REFERENCE NUMBER: TC-001

c:\pwworking\rtd_eagle_p3\dms00490\GL-T-TC-001-TrkCht.dgn
6/30/2011
USER: icrowe

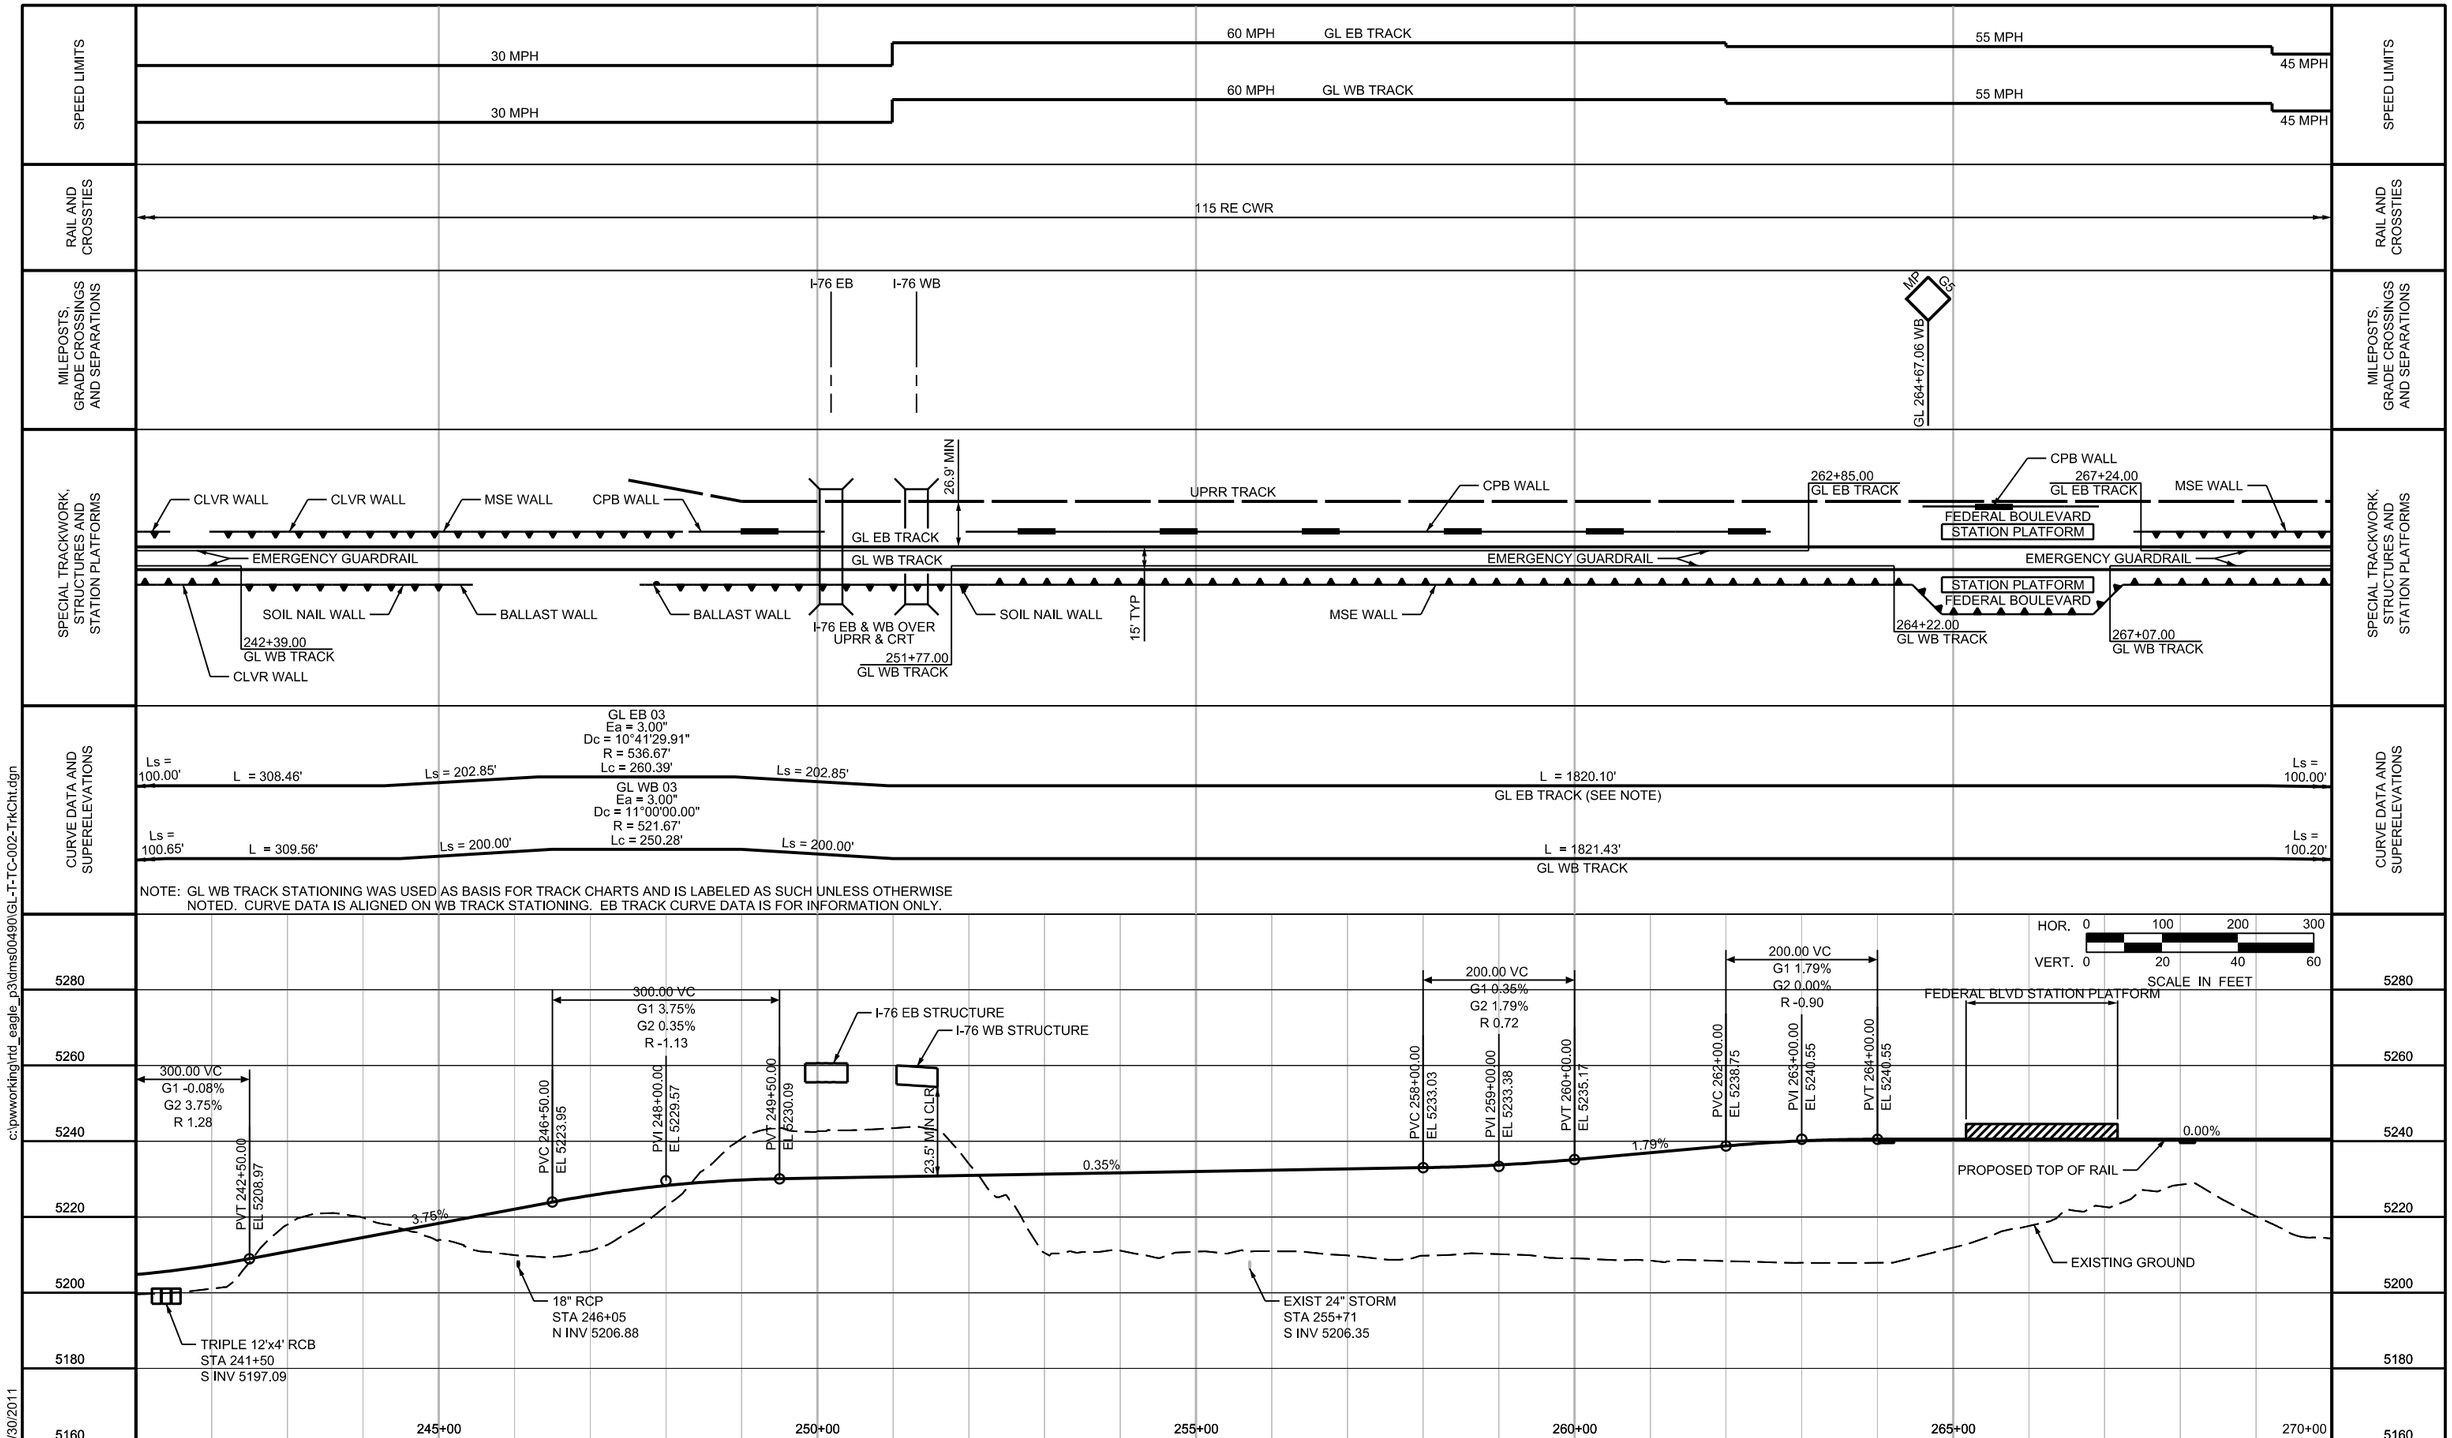

c:\pwworking\rtd_eagle_p3\dms00490\GL-T-TC-002-TrkCht.dgn

6/30/2011

USER: icrowe

NO.	REVISIONS	BY	DATE
B	ISSUED FOR 60% SUBMITTAL, CDRL #7B-03.07, REV B	AD	06/13/11
A1	ISSUED FOR CONST REVIEW, CDRL #7B-03.07, REV A1	AD	05/23/11

DESIGNED BY: DWH/VHH DATE: 05/13/11
DRAWN BY: DWH/VHH DATE: 05/13/11
CHECKED BY: DATE:
APPROVED BY: DATE:

RTD FASTRACKS
eagle P3
FLUOR HDR
GLOBAL DESIGN CONSULTANTS

DENVER TRANSIT PARTNERS

GOLD LINE

TRACK CHARTS
STA 241+00 TO STA 270+00

SHEET REFERENCE NUMBER:
TC-002

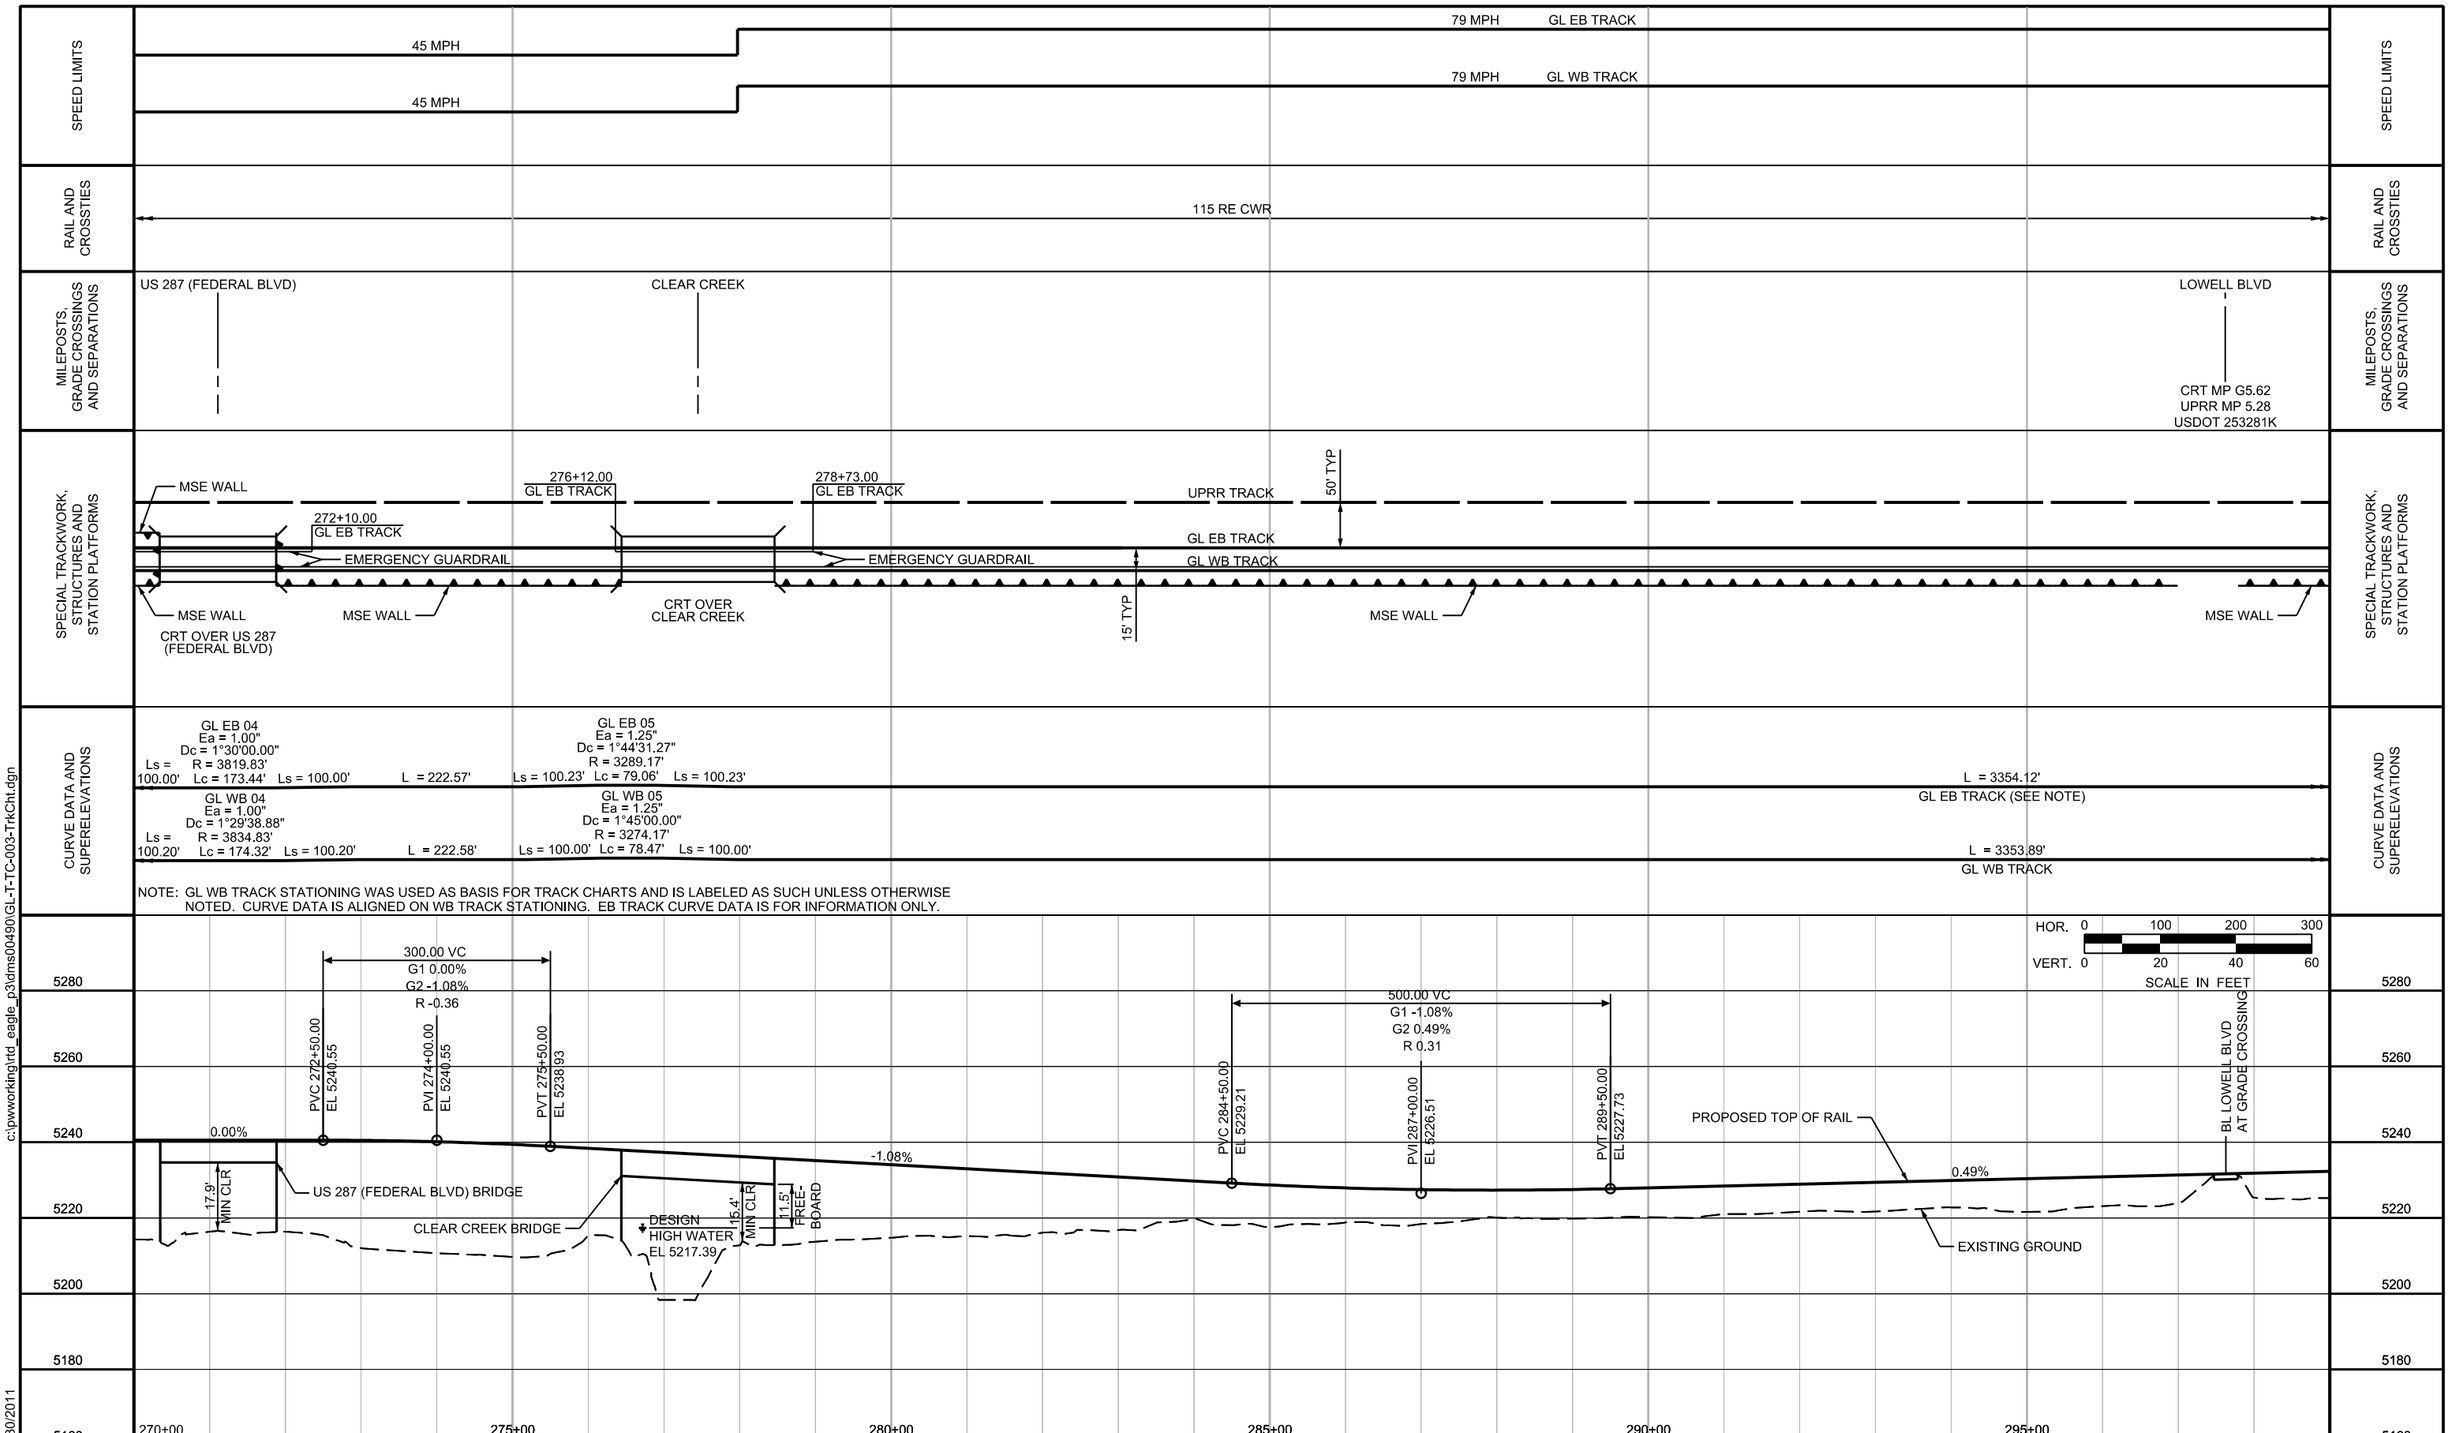

c:\pwworking\rtd_eagle_p3\dms00490\GL-T-TC-003-TrkCht.dgn

6/30/2011

USER: icrowe

NO.	REVISIONS	BY	DATE
B	ISSUED FOR 60% SUBMITTAL, CDRL #7B-03.07, REV B	AD	06/13/11
A1	ISSUED FOR CONST REVIEW, CDRL #7B-03.07, REV A1	AD	05/23/11

DESIGNED BY: DWH/VHH DATE: 05/13/11
DRAWN BY: DWH/VHH DATE: 05/13/11
CHECKED BY: DATE:
APPROVED BY: DATE:

RTD FASTTRACKS
eagle P3
FLUOR HDR GLOBAL DESIGN CONSULTANTS
DENVER TRANSIT PARTNERS

GOLD LINE

TRACK CHARTS
STA 270+00 TO STA 299+00

SHEET REFERENCE NUMBER:
TC-003

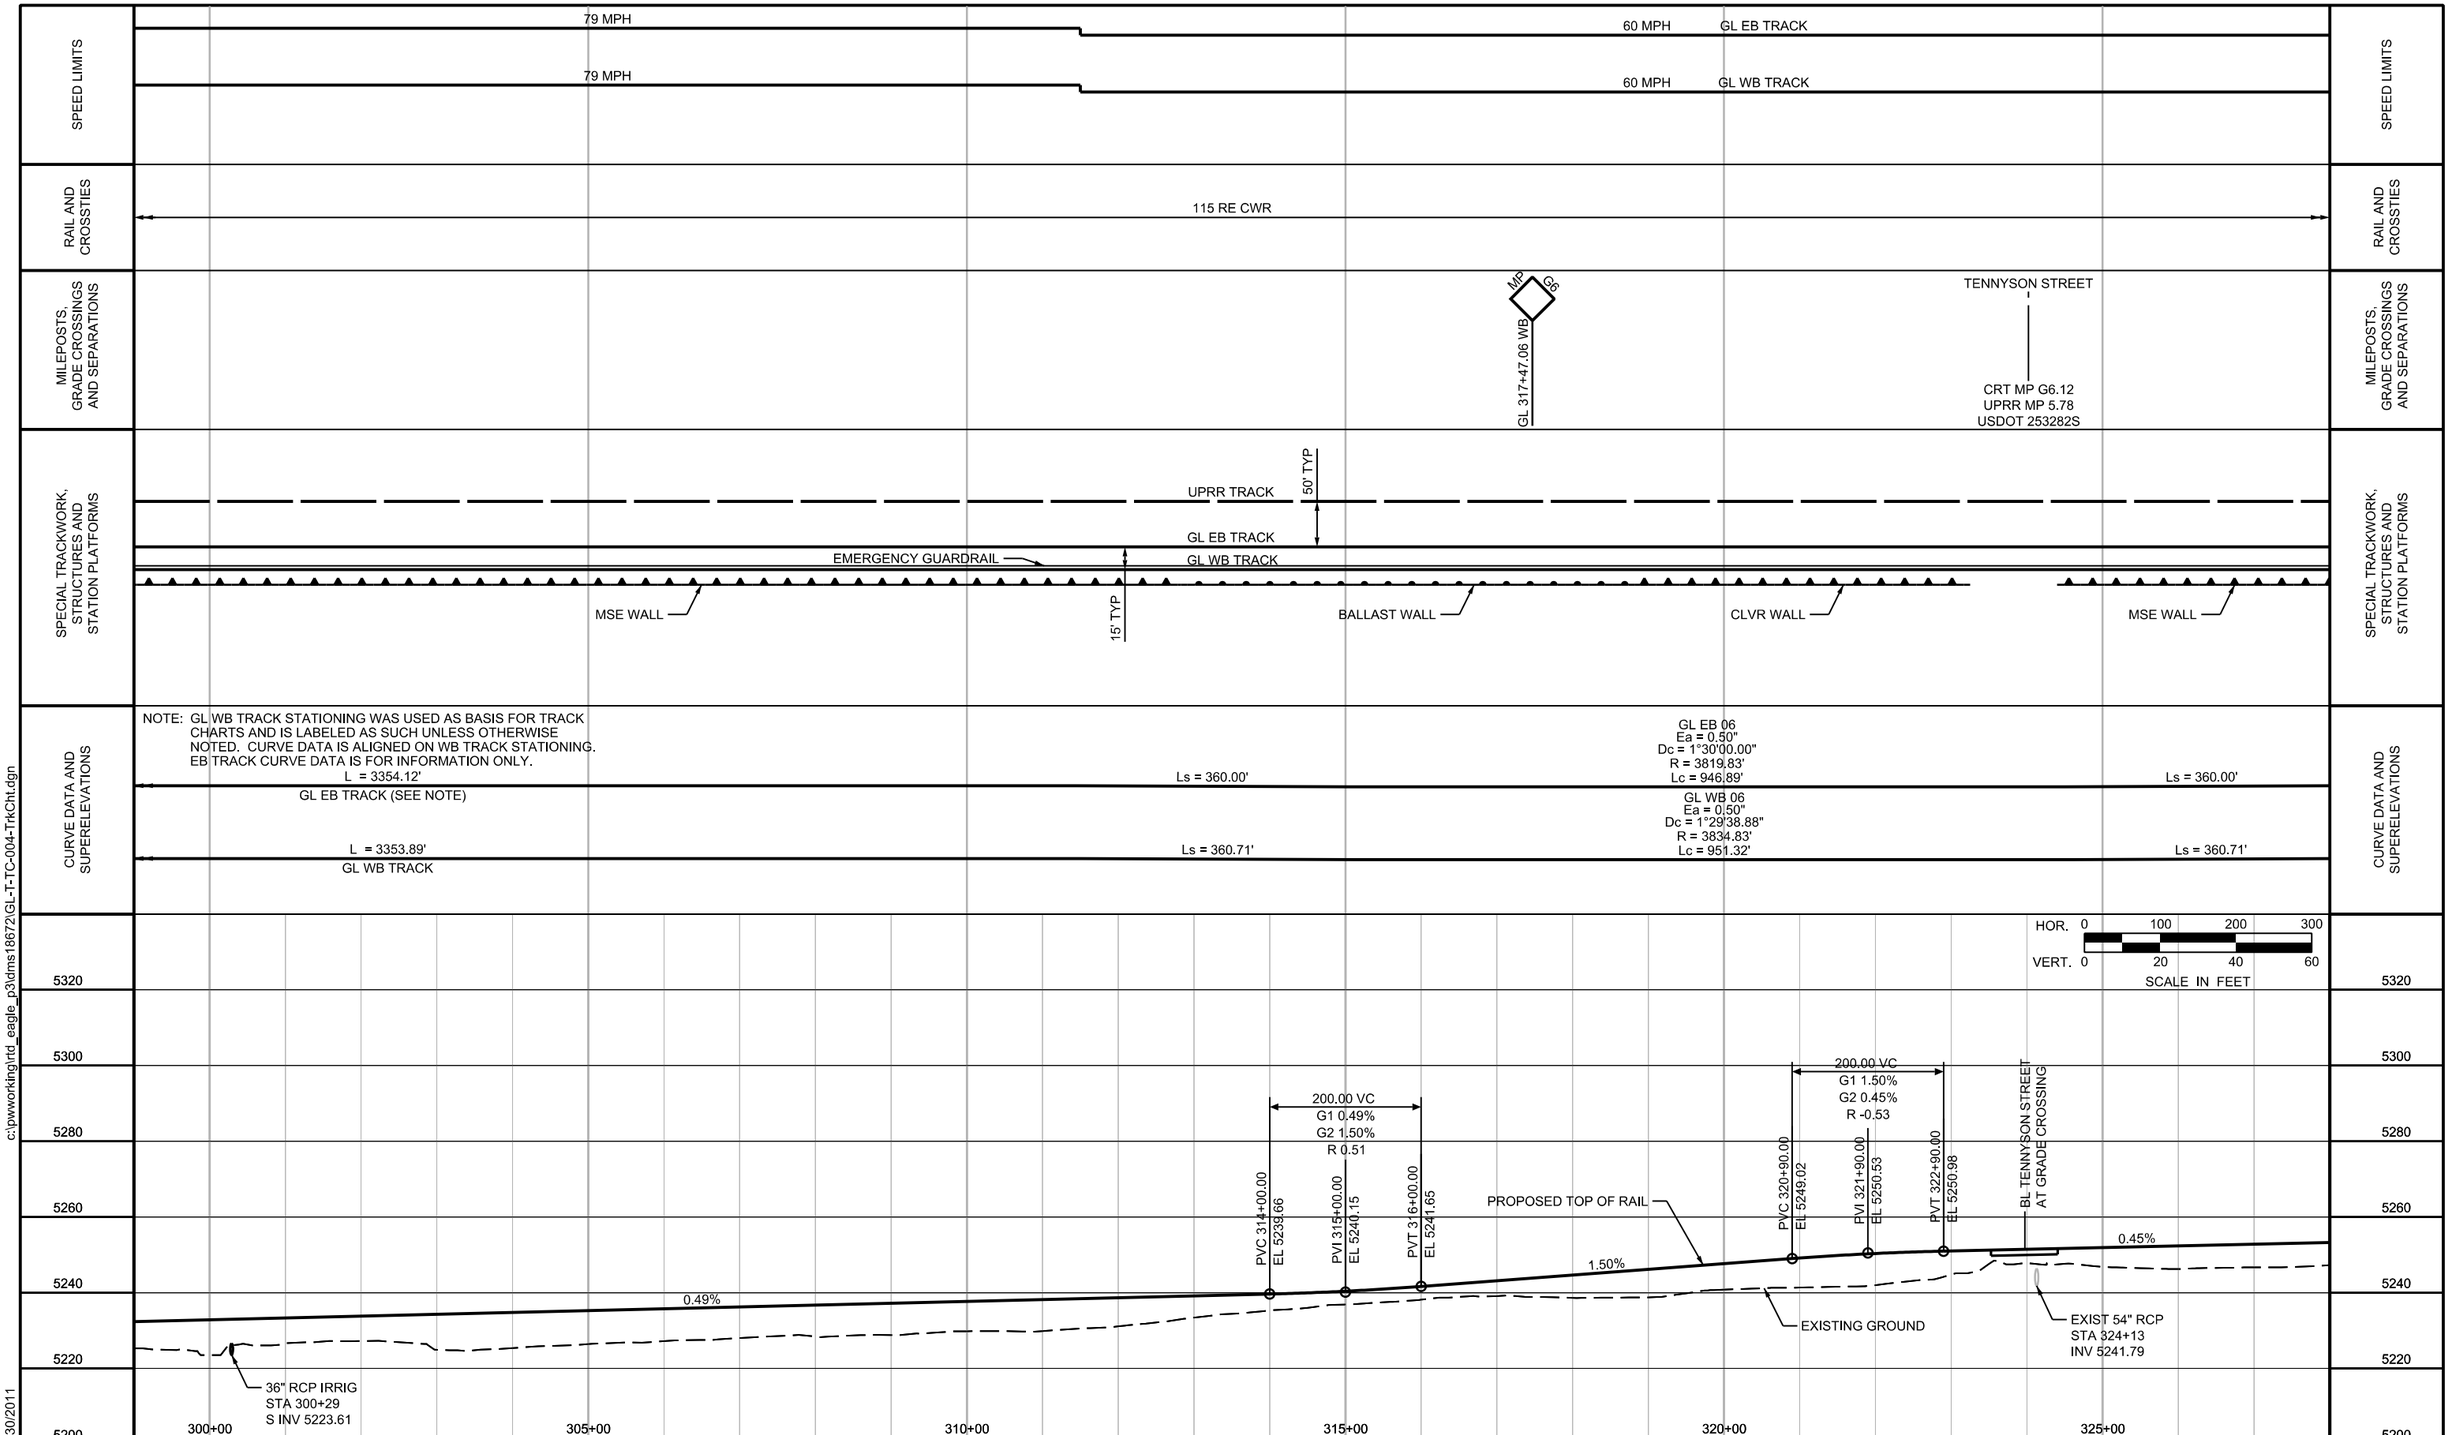

c:\pwworking\ttd_eagle_p3\dms18672\GL-T-TC-004-TrkCht.dgn

6/30/2011

USER: icrowe

NO.	REVISIONS	BY	DATE
B	ISSUED FOR 60% SUBMITTAL, CDRL #7B-03.07-08, REV B	AD	06/30/11
A1	ISSUED FOR CONST REVIEW, CDRL #7B-03.07-08, REV A1	AD	05/23/11

DESIGNED BY: DWH/VHH DATE: 05/13/11
DRAWN BY: DWH/VHH DATE: 05/13/11
CHECKED BY: DATE:
APPROVED BY: DATE:

RTD FASTTRACKS
eagle P3
FLUOR HDR GLOBAL DESIGN CONSULTANTS
DENVER TRANSIT PARTNERS

GOLD LINE

TRACK CHARTS
STA 299+00 TO STA 328+00

SHEET REFERENCE NUMBER:
TC-004

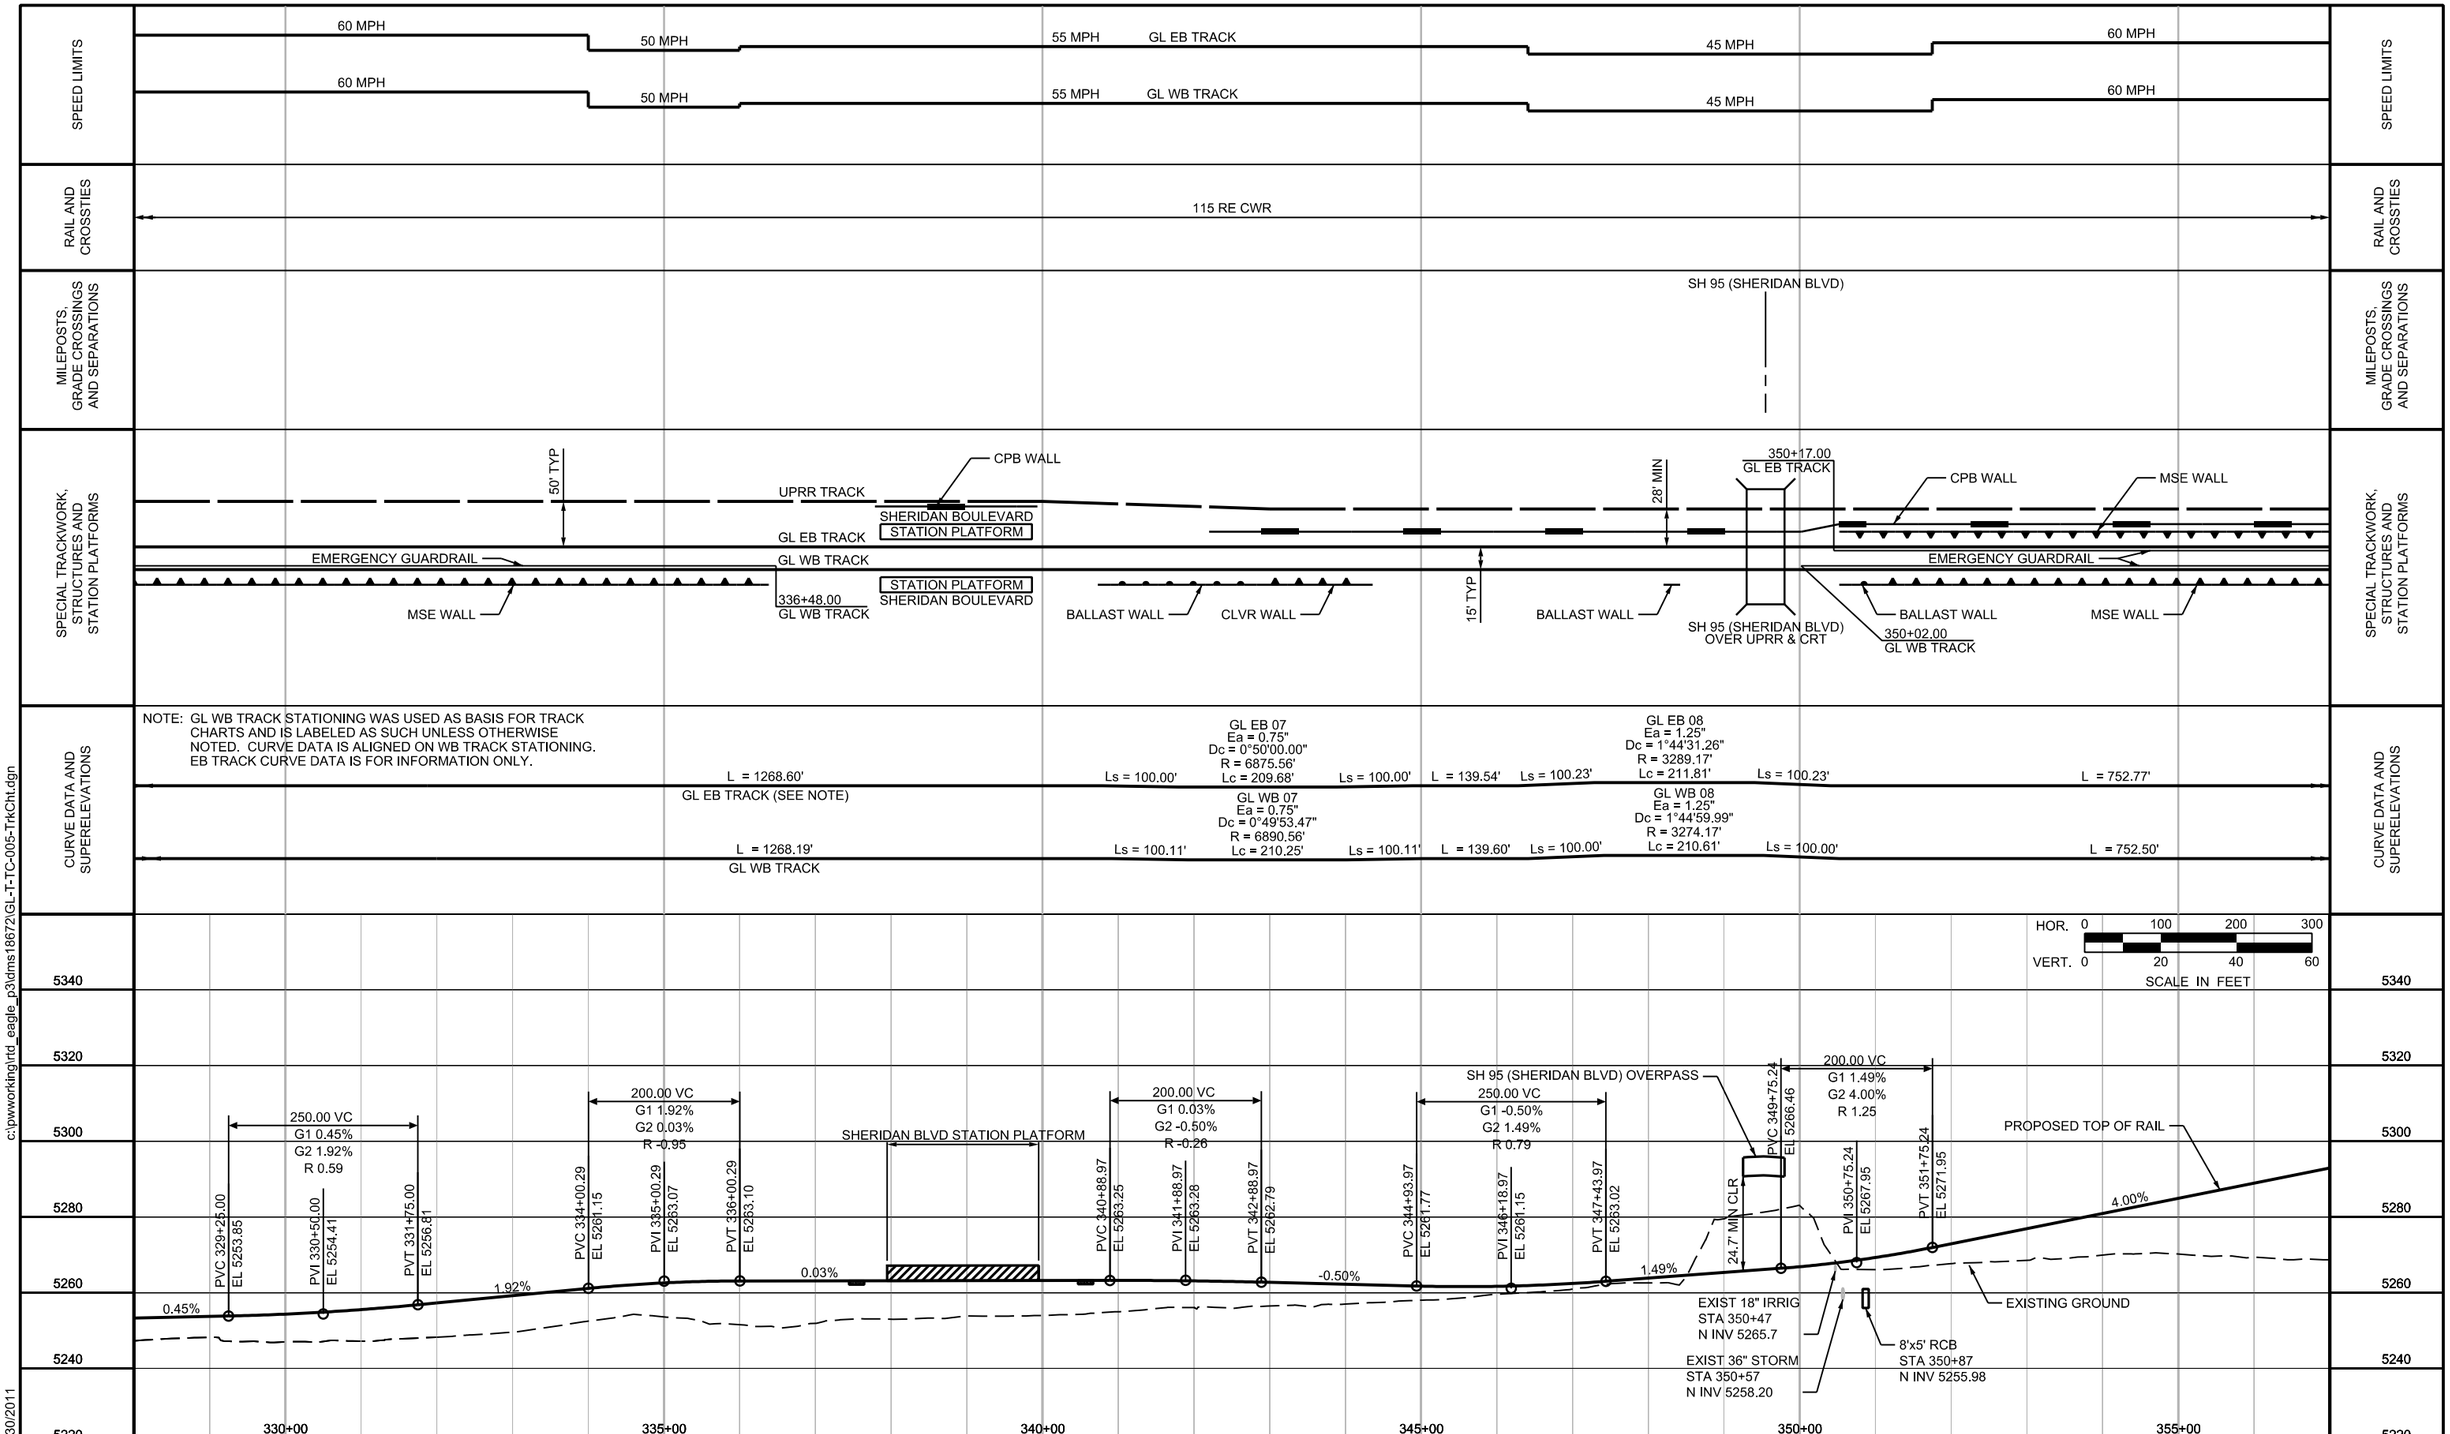

NO.	REVISIONS	BY	DATE
B	ISSUED FOR 60% SUBMITTAL, CDRL #7B-03.08, REV B	AD	06/30/11
A1	ISSUED FOR CONST REVIEW, CDRL #7B-03.07, REV A1	AD	05/23/11

DESIGNED BY: DWH/VHH DATE: 05/13/11
DRAWN BY: DWH/VHH DATE: 05/13/11
CHECKED BY: DATE:
APPROVED BY: DATE:

RTD FASTRACKS
eagle P3
FLUOR HDR GLOBAL DESIGN CONSULTANTS
DENVER TRANSIT PARTNERS

GOLD LINE

TRACK CHARTS
STA 328+00 TO STA 357+00

SHEET REFERENCE NUMBER: TC-005

c:\pwworking\rtd_eagle_p3\dms18672\GL-T-TC-005-TrkCht.dgn
6/30/2011
USER: icrowe

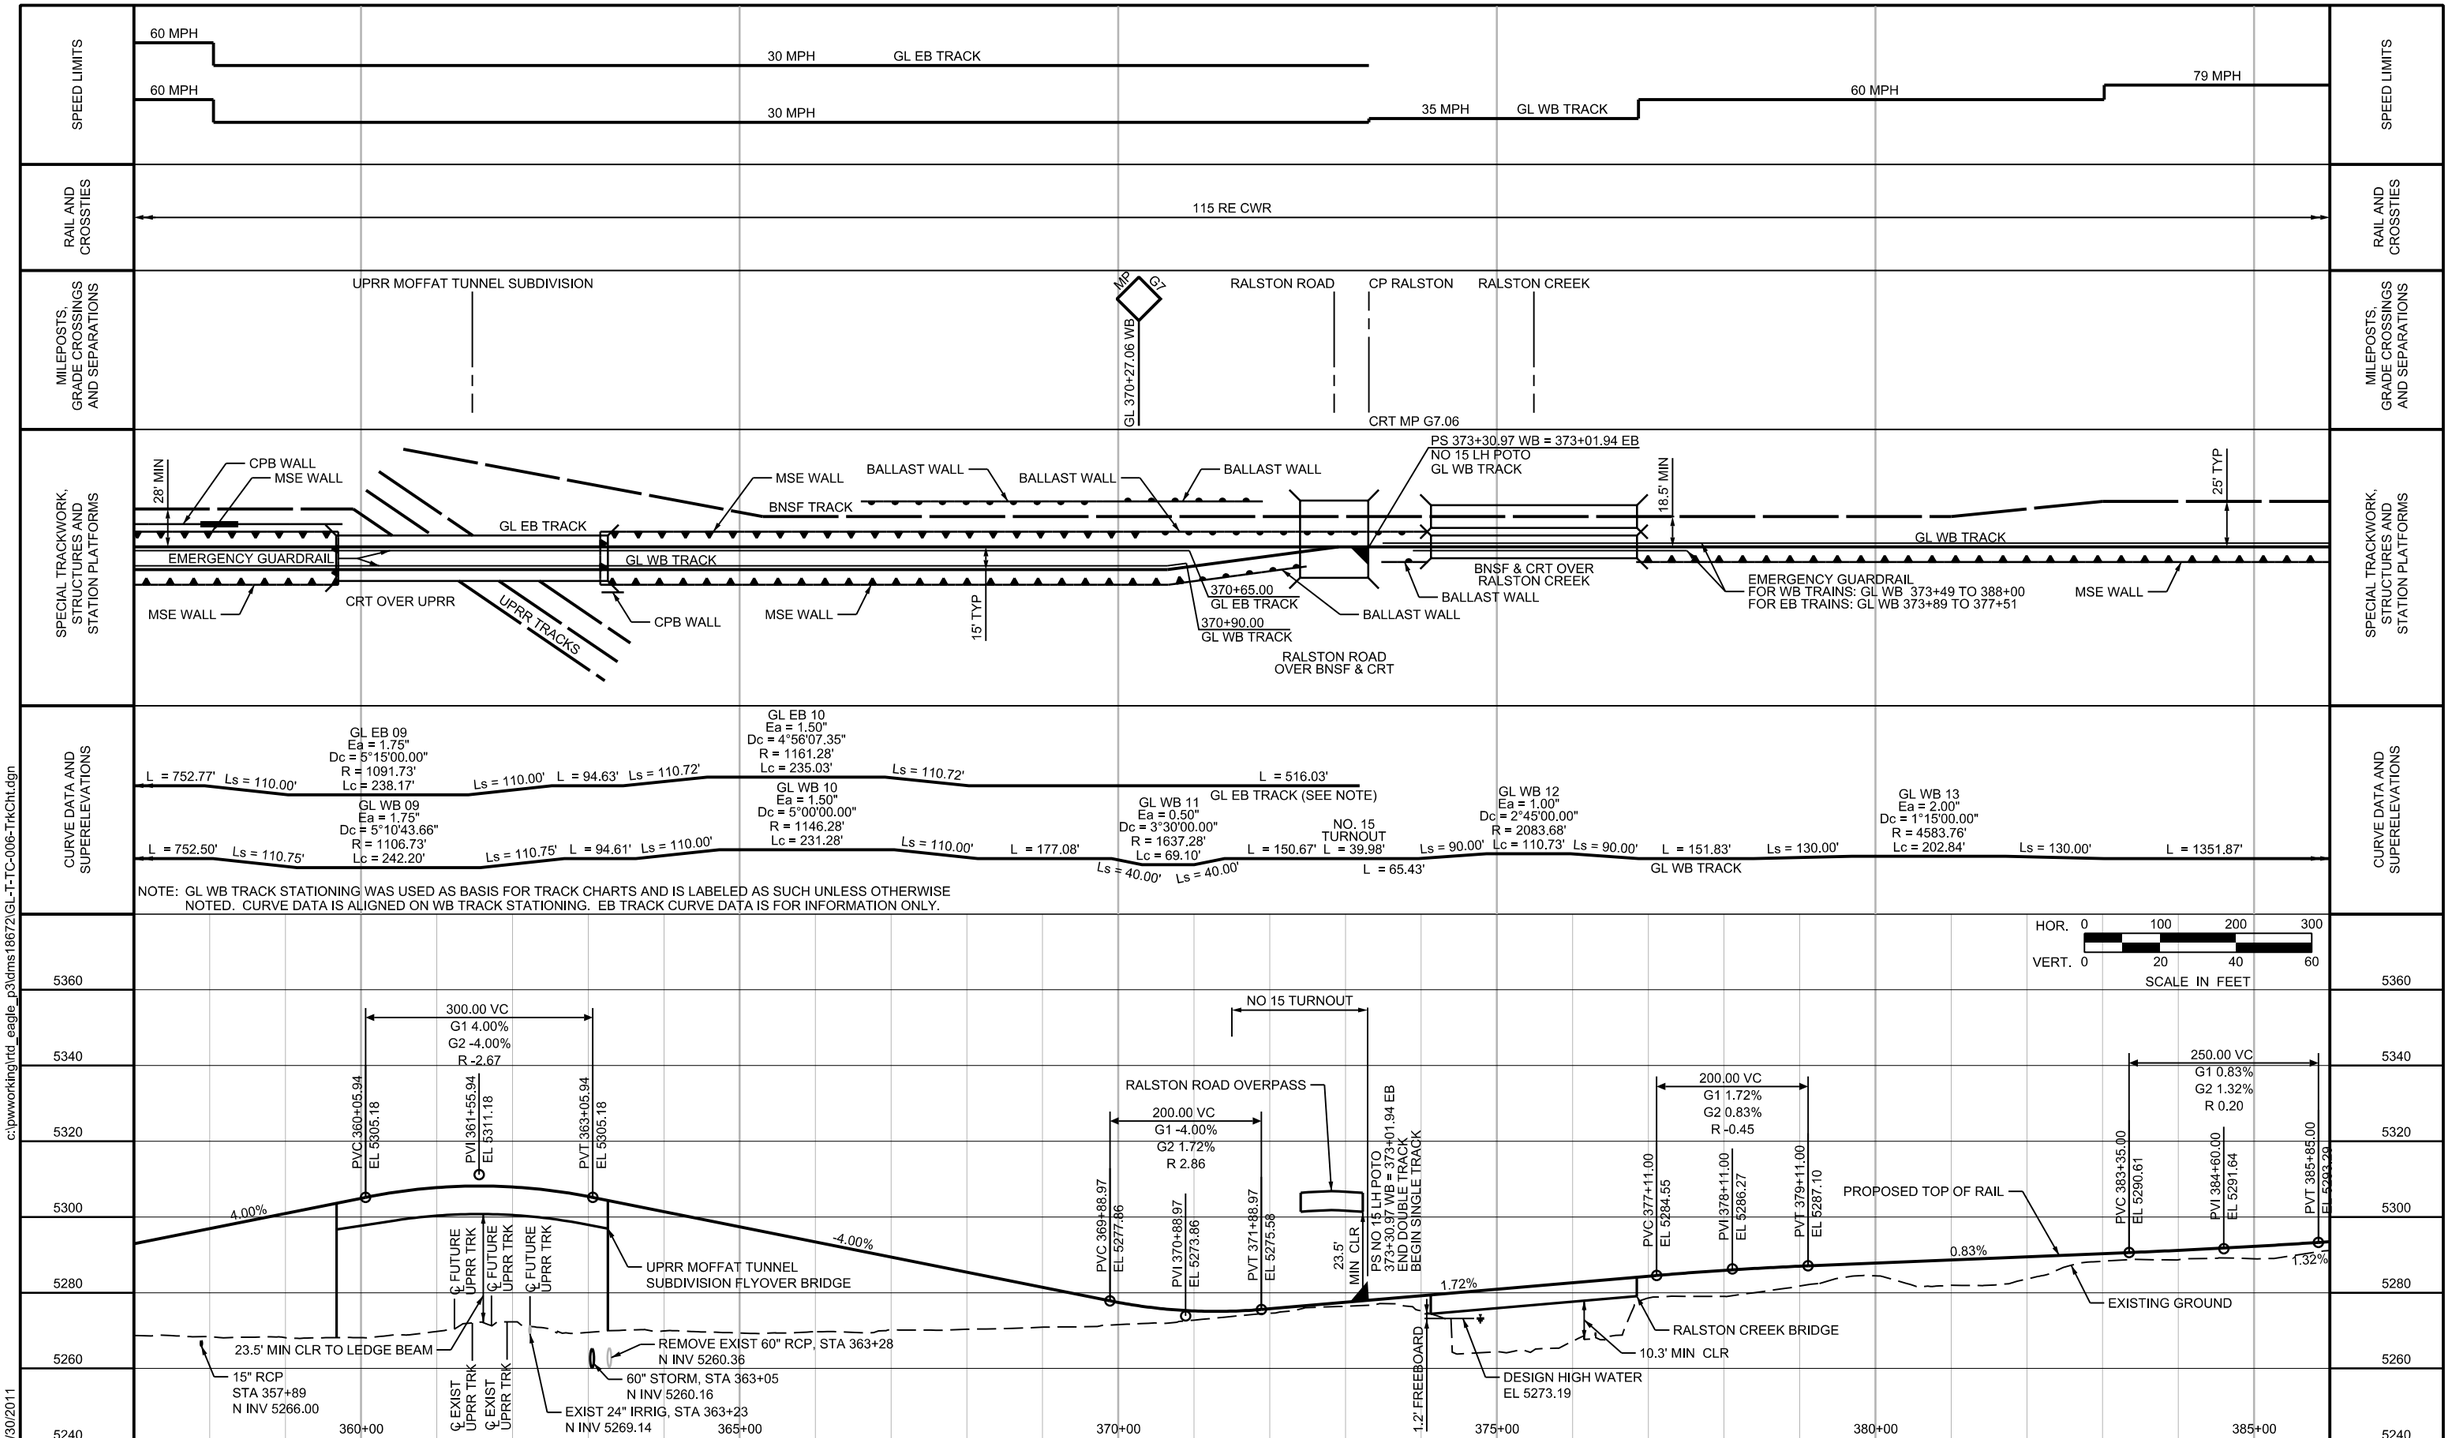

c:\pwworking\rtd_eagle_p3\dms18672\GL-T-TC-006-TrkCht.dgn

6/30/2011

USER: icrowe

NO.	REVISIONS	BY	DATE
B	ISSUED FOR 60% SUBMITTAL, CDRL #7B-03.08, REV B	AD	06/30/11
A1	ISSUED FOR CONST REVIEW, CDRL #7B-03.07, REV A1	AD	05/23/11

DESIGNED BY: DWH/VHH DATE: 05/13/11
DRAWN BY: DWH/VHH DATE: 05/13/11
CHECKED BY: DATE:
APPROVED BY: DATE:

RTD FASTTRACKS
eagle P3
FLUOR HDR
GLOBAL DESIGN CONSULTANTS

DENVER TRANSIT PARTNERS

GOLD LINE

TRACK CHARTS
STA 357+00 TO STA 386+00

SHEET REFERENCE NUMBER:
TC-006

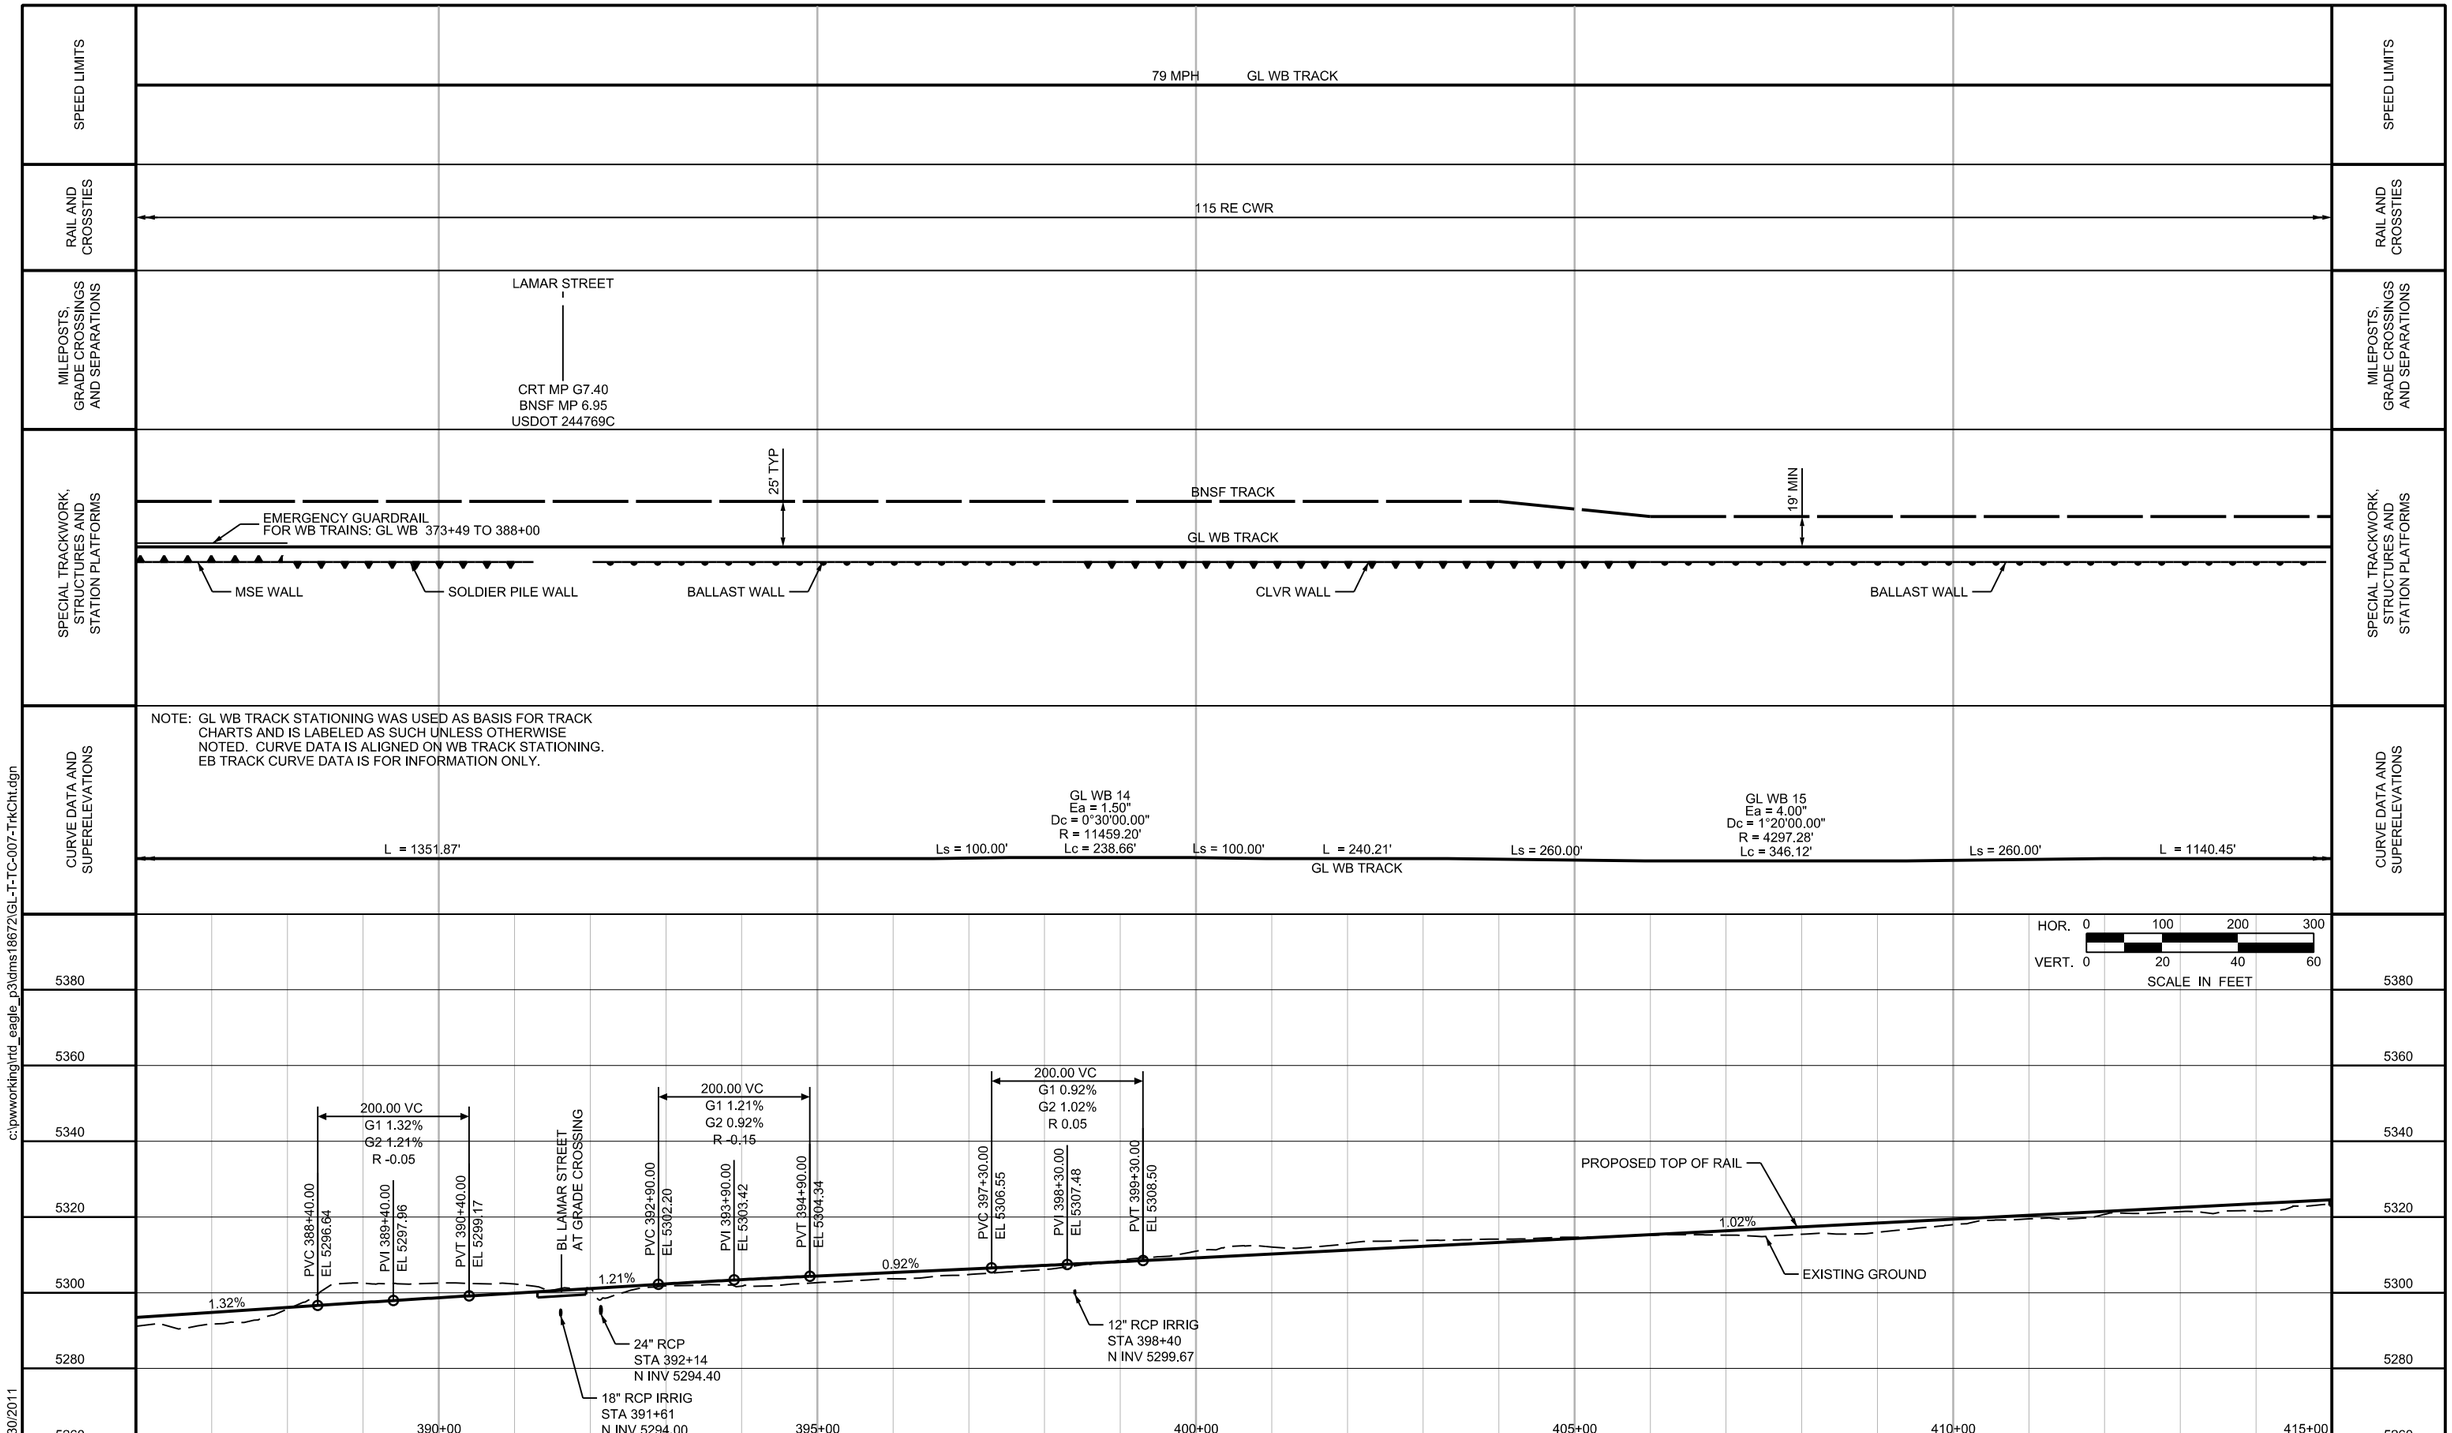

c:\pwworking\rtd_eagle_p3\dms18672\GL-T-TC-007-TrkCht.dgn

6/30/2011

USER: icrowe

NO.	REVISIONS	BY	DATE
B	ISSUED FOR 60% SUBMITTAL, CDRL #7B-03.08, REV B	AD	06/30/11
A1	ISSUED FOR CONST REVIEW, CDRL #7B-03.07, REV A1	AD	05/23/11

DESIGNED BY: DWH/VHH DATE: 05/13/11
DRAWN BY: DWH/VHH DATE: 05/13/11
CHECKED BY: DATE:
APPROVED BY: DATE:

RTD FASTRACKS
eagle P3
FLUOR HDR GLOBAL DESIGN CONSULTANTS
DENVER TRANSIT PARTNERS

GOLD LINE

TRACK CHARTS
STA 386+00 TO 415+00

SHEET REFERENCE NUMBER:
TC-007

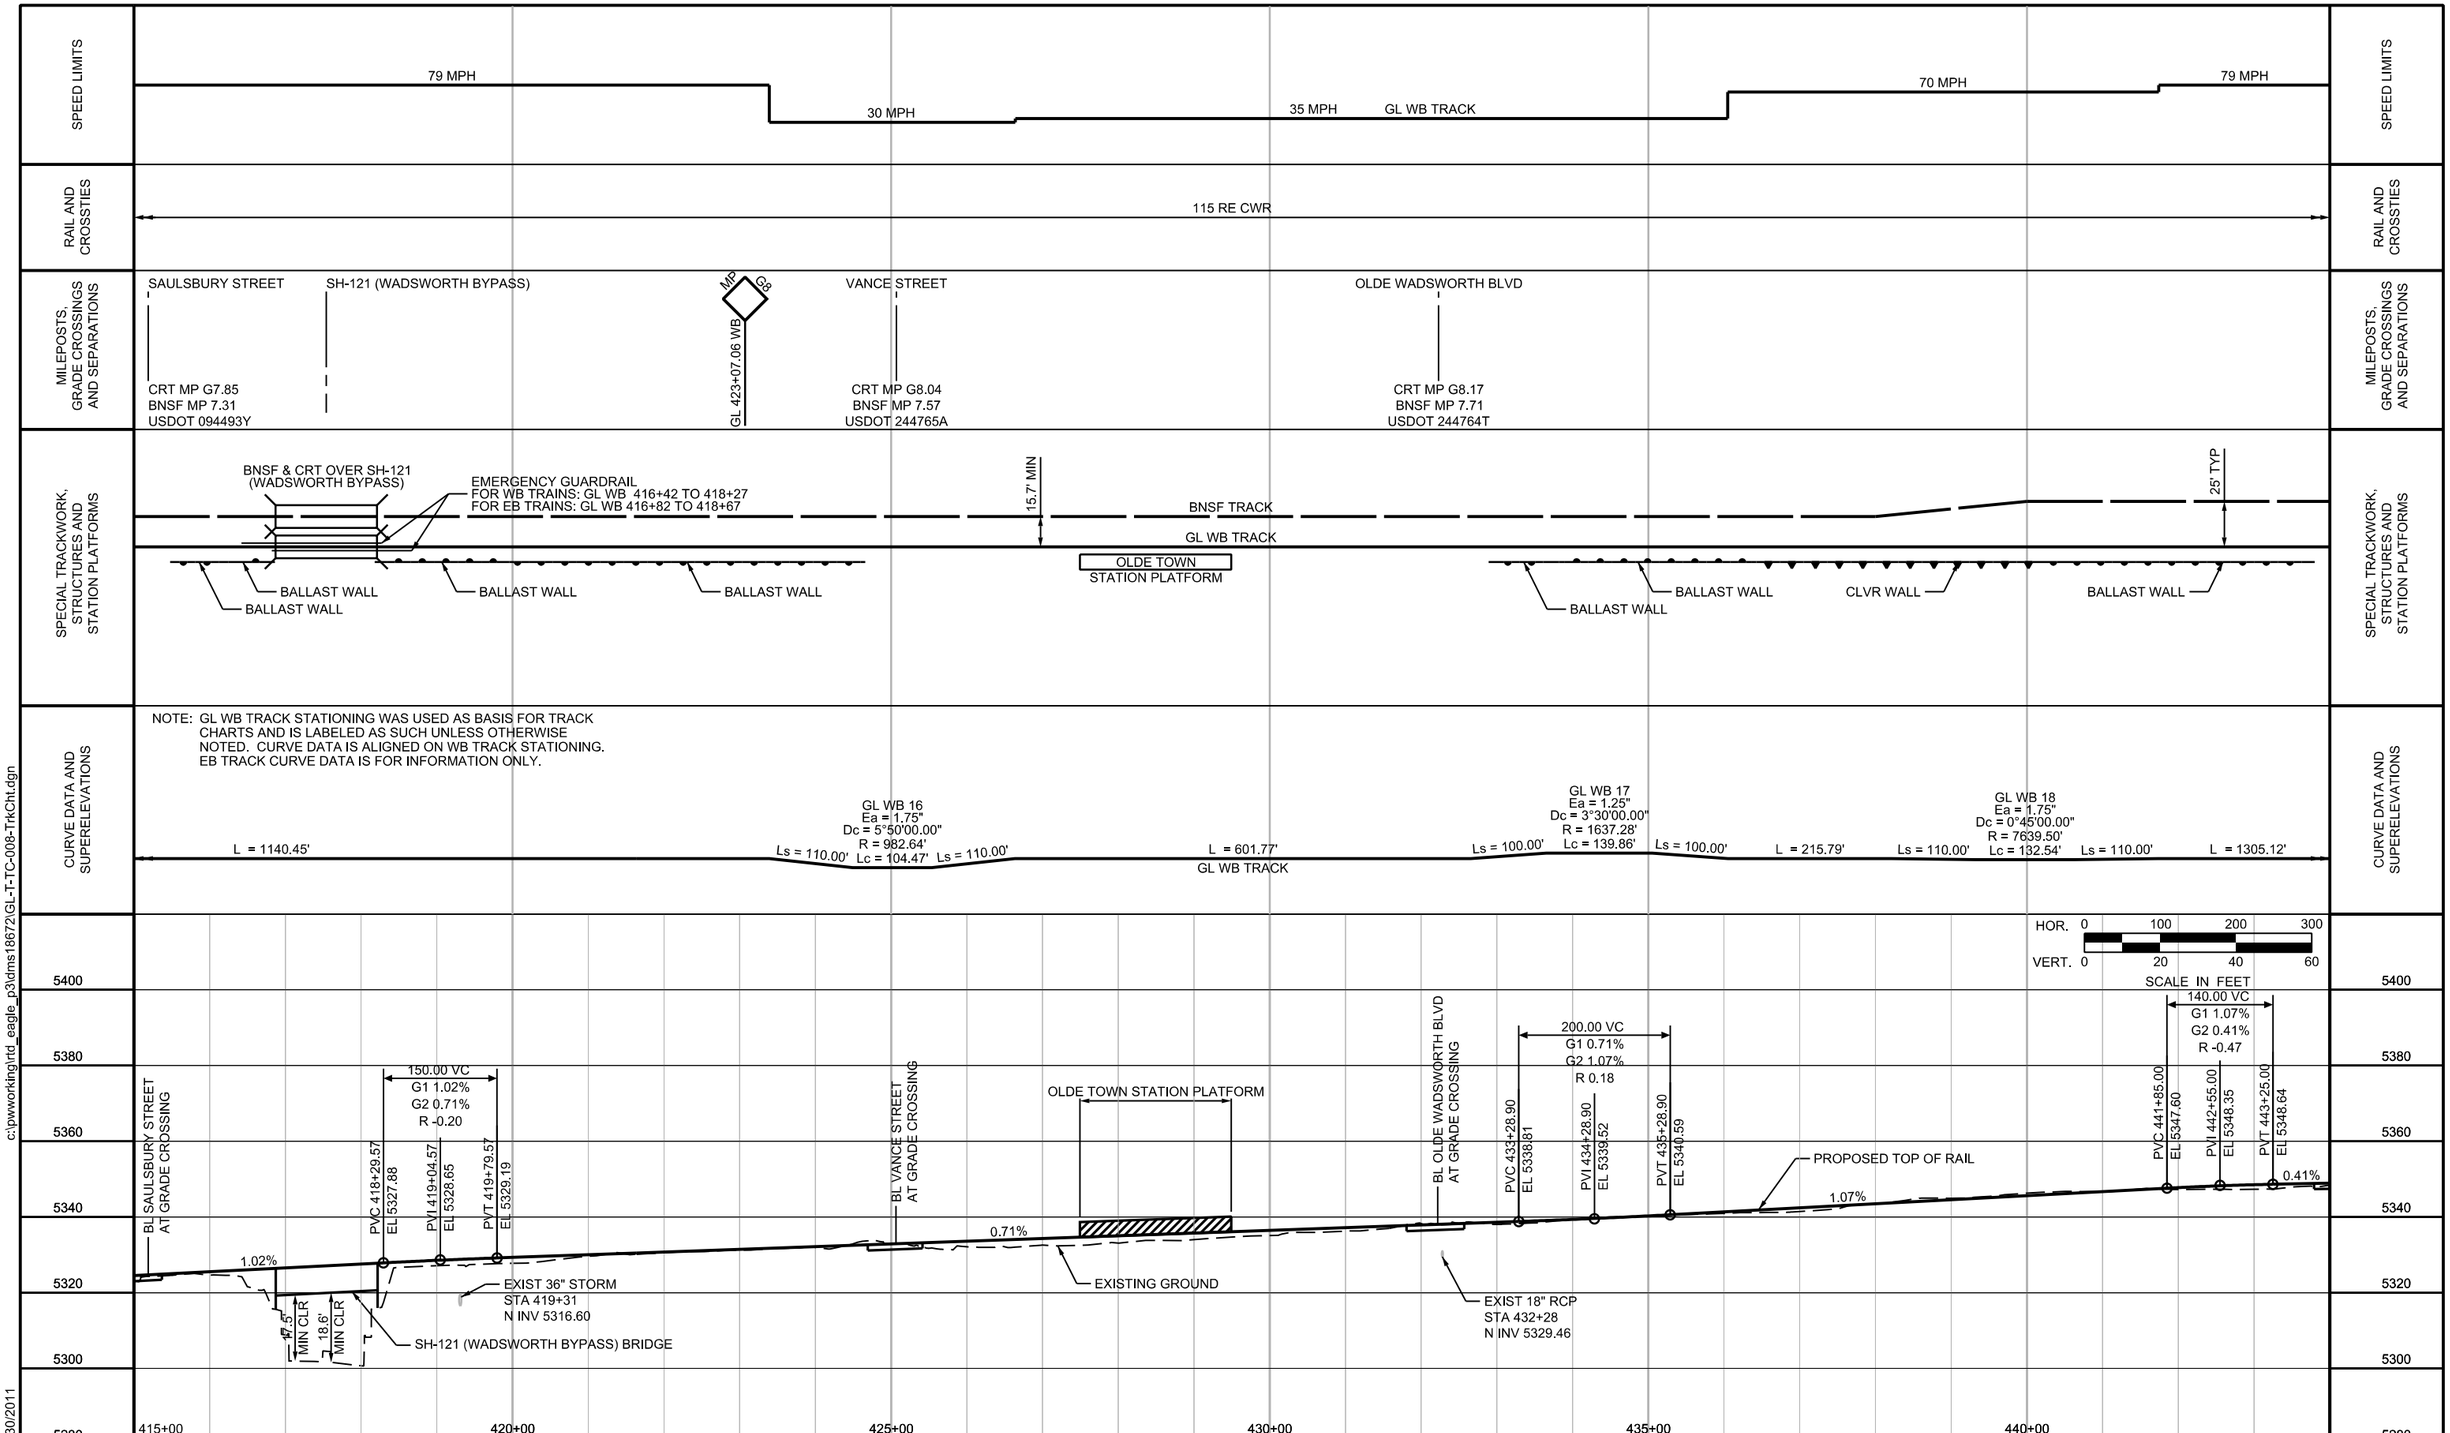

c:\pwworking\rtd_eagle_p3\dms18672\GL-T-TC-008-TrkCht.dgn

6/30/2011

USER: icrowe

NO.	REVISIONS	BY	DATE
B	ISSUED FOR 60% SUBMITTAL, CDRL #7B-03.08, REV B	AD	06/30/11
A1	ISSUED FOR CONST REVIEW, CDRL #7B-03.07, REV A1	AD	05/23/11

DESIGNED BY: DWH/VHH DATE: 05/13/11
DRAWN BY: DWH/VHH DATE: 05/13/11
CHECKED BY: DATE:
APPROVED BY: DATE:

RTD FASTRACKS
eagle P3
FLUOR HDR GLOBAL DESIGN CONSULTANTS
DENVER TRANSIT PARTNERS

GOLD LINE

TRACK CHARTS
STA 415+00 TO STA 444+00

SHEET REFERENCE NUMBER:
TC-008

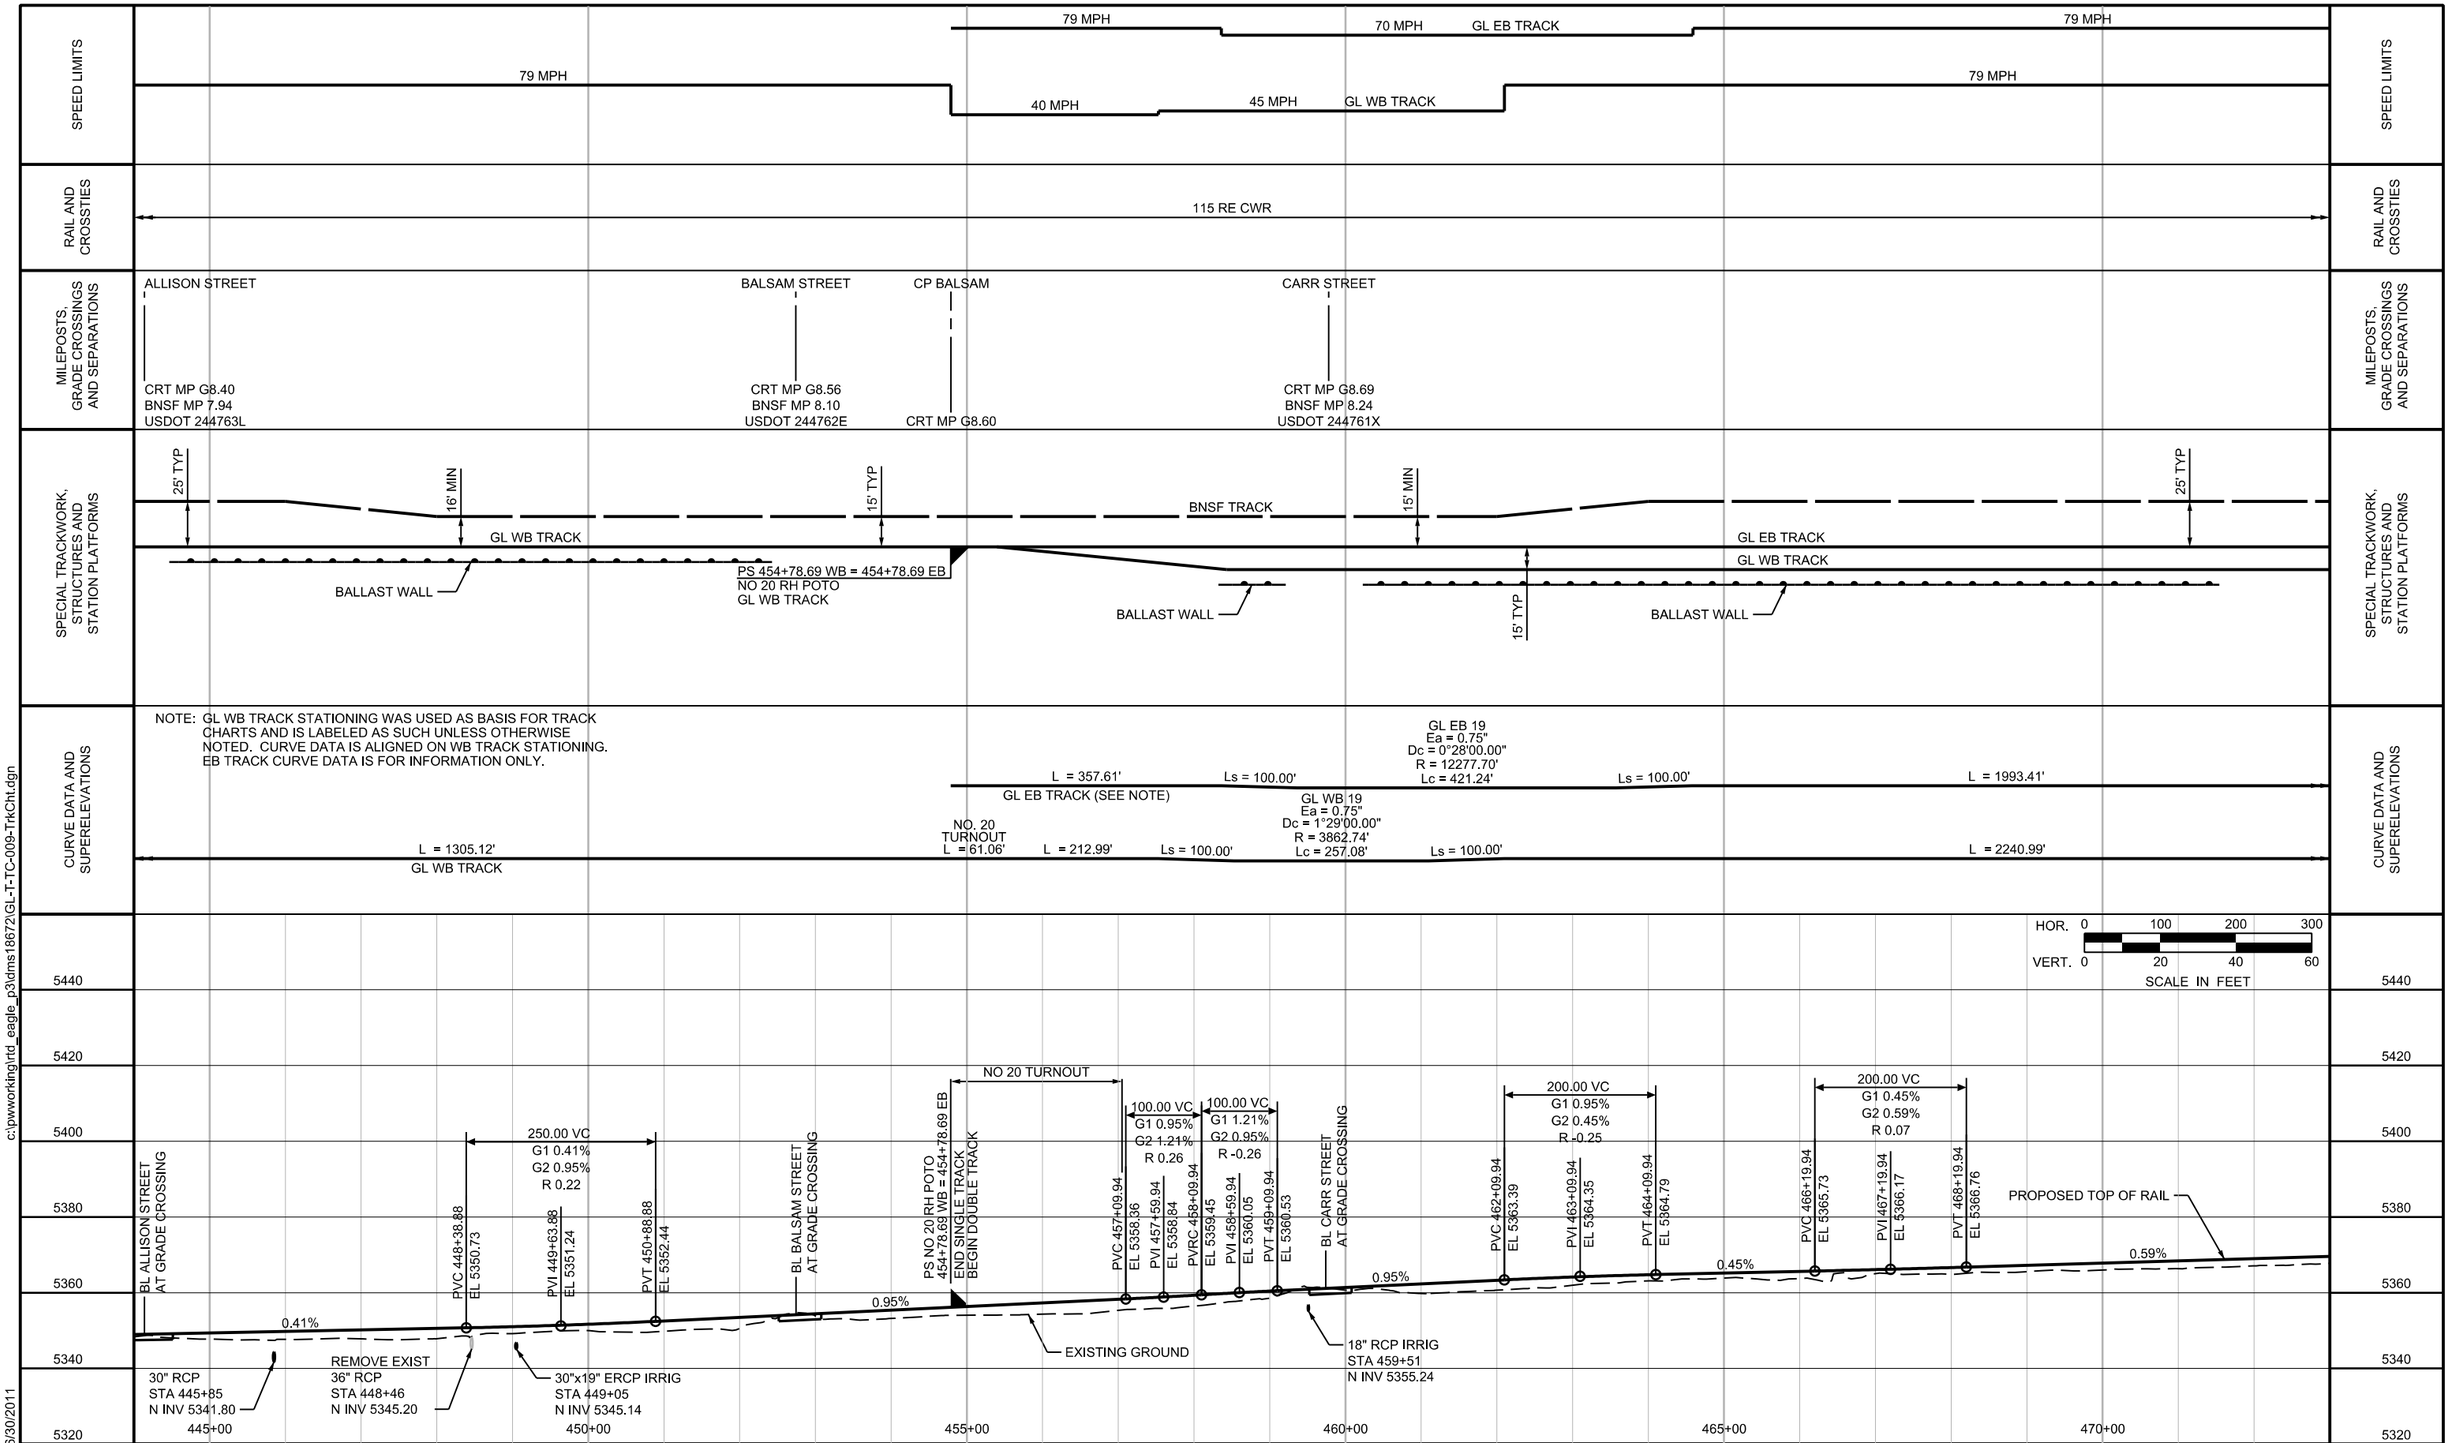

c:\pwworking\rtd_eagle_p3\dms18672\GL-T-TC-009-TrkCht.dgn

6/30/2011

USER: icrowe

NO.	REVISIONS	BY	DATE
B	ISSUED FOR 60% SUBMITTAL, CDRL #7B-03.08, REV B	AD	06/30/11
A1	ISSUED FOR CONST REVIEW, CDRL #7B-03.07, REV A1	AD	05/23/11

DESIGNED BY: DWH/VHH DATE: 05/13/11
DRAWN BY: DWH/VHH DATE: 05/13/11
CHECKED BY: DATE:
APPROVED BY: DATE:

RTD FASTRACKS eagle P3 FLUOR HDR GLOBAL DESIGN CONSULTANTS

DENVER TRANSIT PARTNERS

GOLD LINE

TRACK CHARTS
STA 444+00 TO STA 473+00

SHEET REFERENCE NUMBER:

TC-009

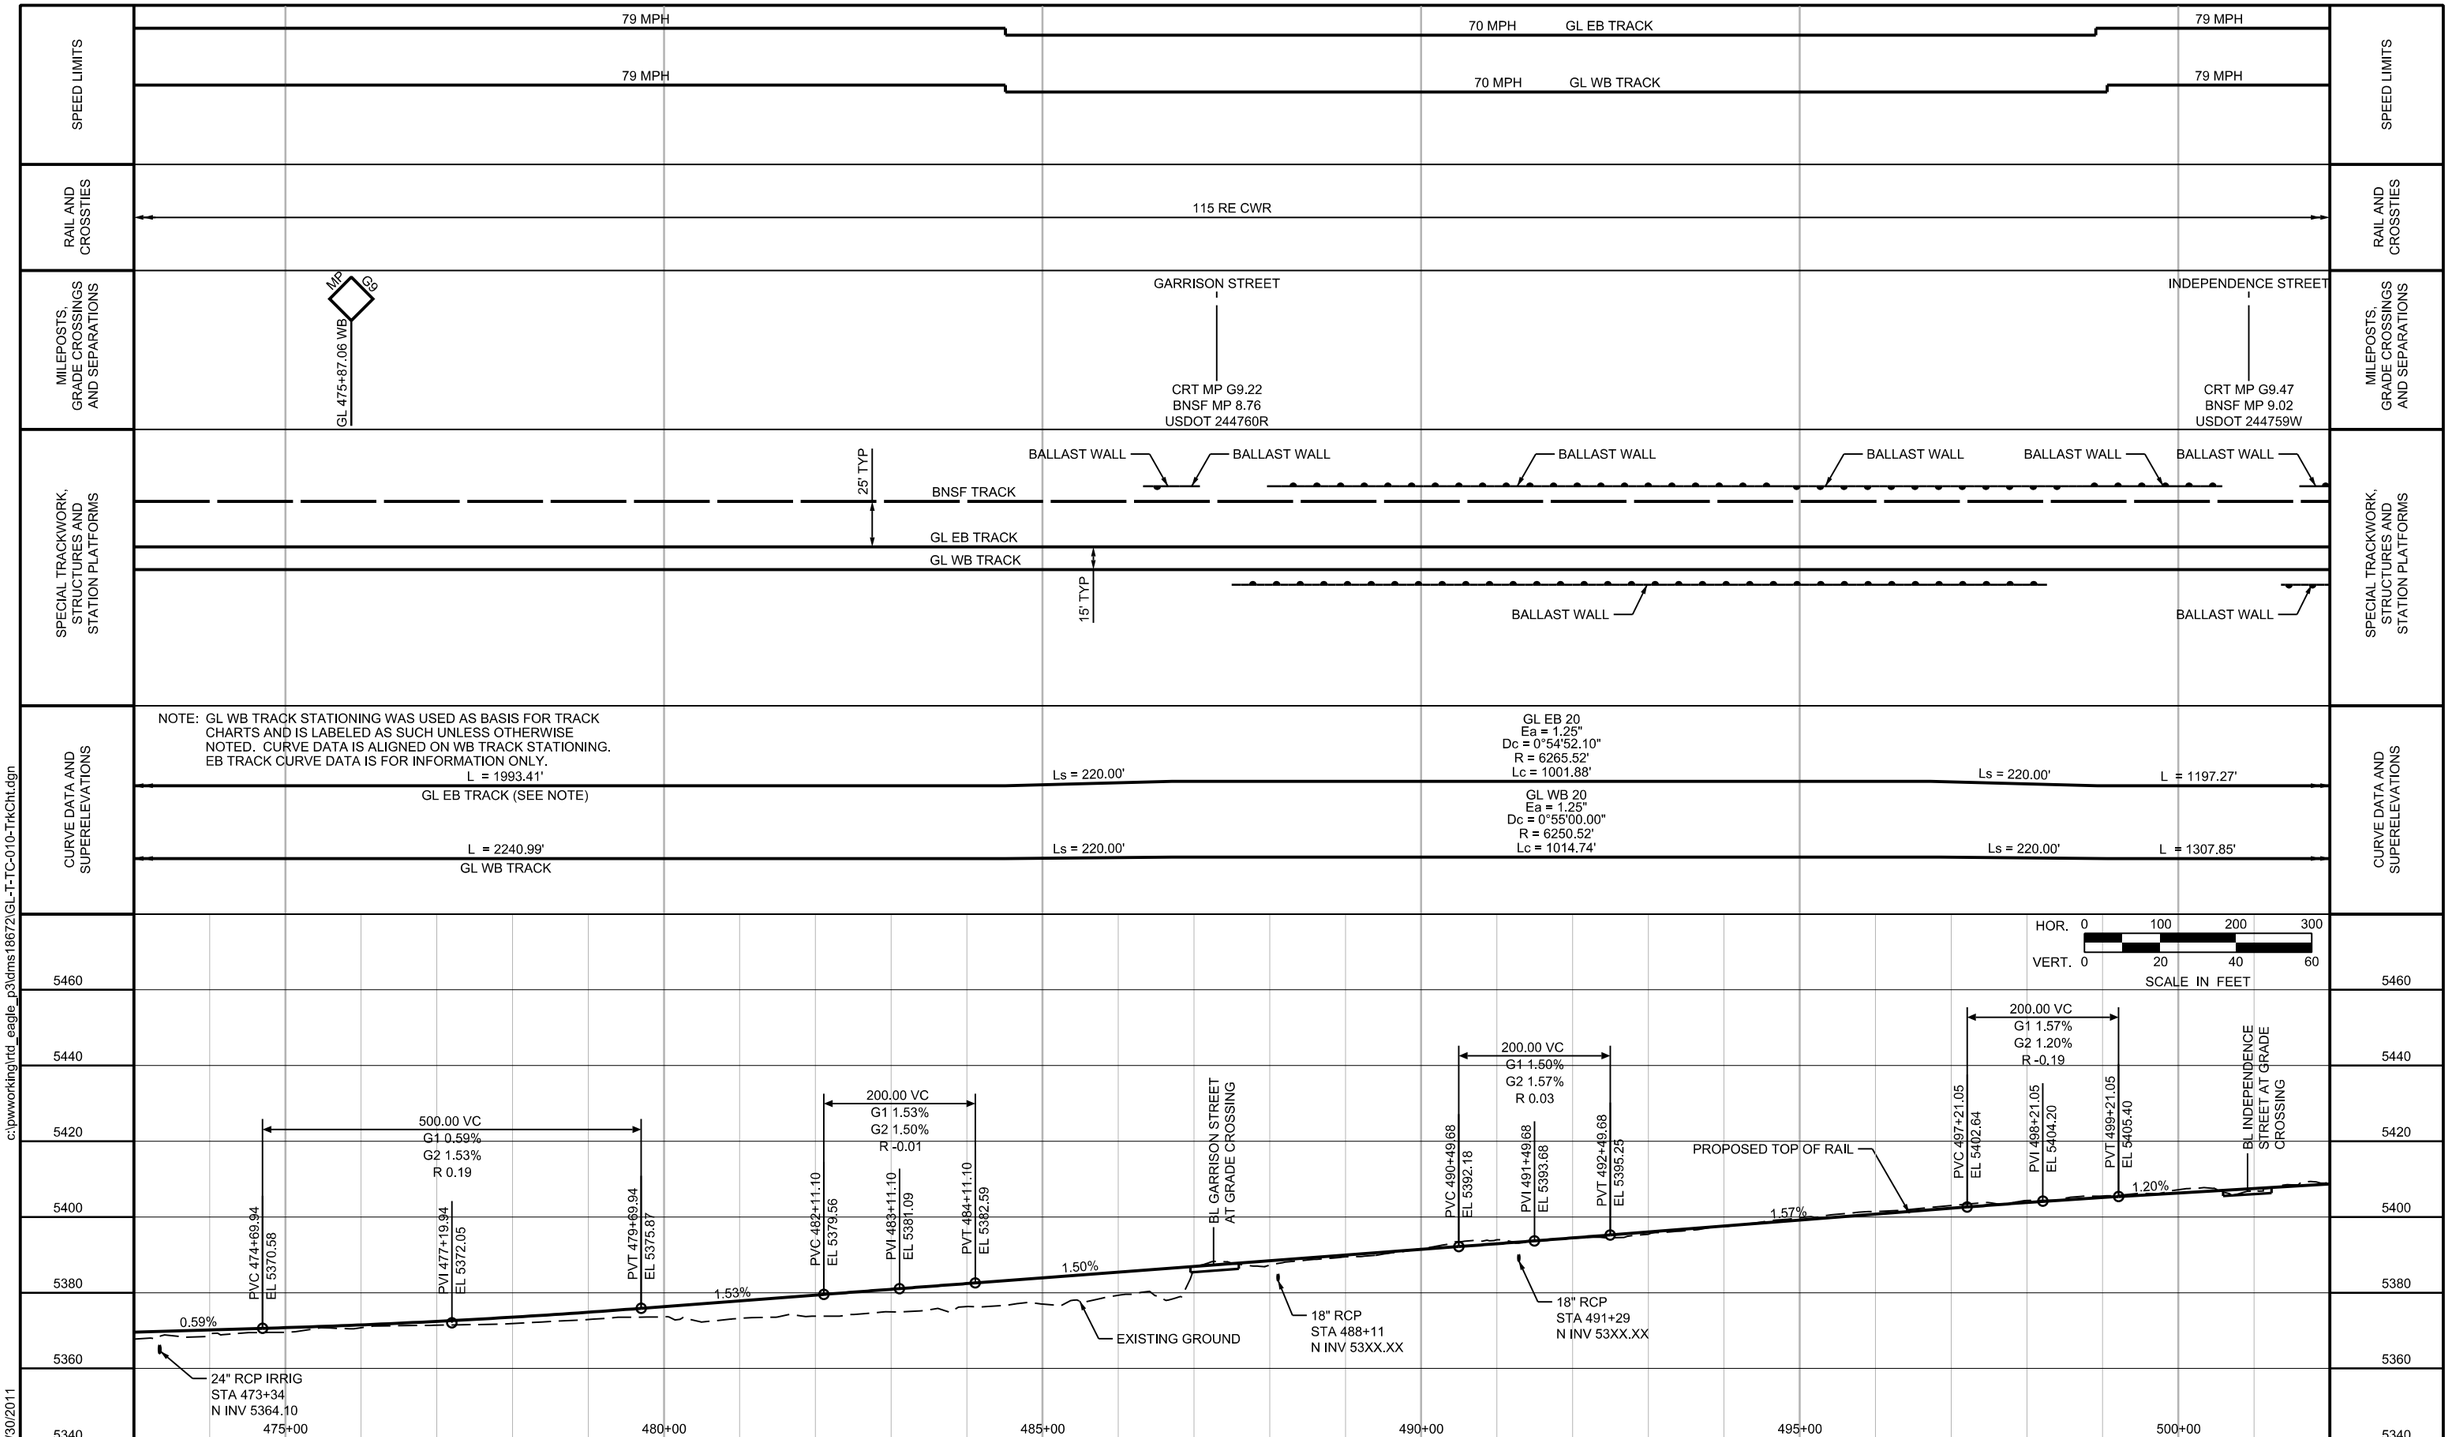

c:\pwworking\rtd_eagle_p3\dms18672\GL-T-TC-010-TrkCht.dgn

6/30/2011

USER: icrowe

NO.	REVISIONS	BY	DATE
B	ISSUED FOR 60% SUBMITTAL, CDRL #7B-03.08, REV B	AD	06/30/11
A1	ISSUED FOR CONST REVIEW, CDRL #7B-03.07, REV A1	AD	05/23/11

DESIGNED BY: DWH/VHH DATE: 05/13/11
DRAWN BY: DWH/VHH DATE: 05/13/11
CHECKED BY: DATE:
APPROVED BY: DATE:

RTD FASTTRACKS
eagle P3
FLUOR HDR GLOBAL DESIGN CONSULTANTS
DENVER TRANSIT PARTNERS

GOLD LINE

TRACK CHARTS
STA 473+00 TO STA 502+00

SHEET REFERENCE NUMBER:
TC-010

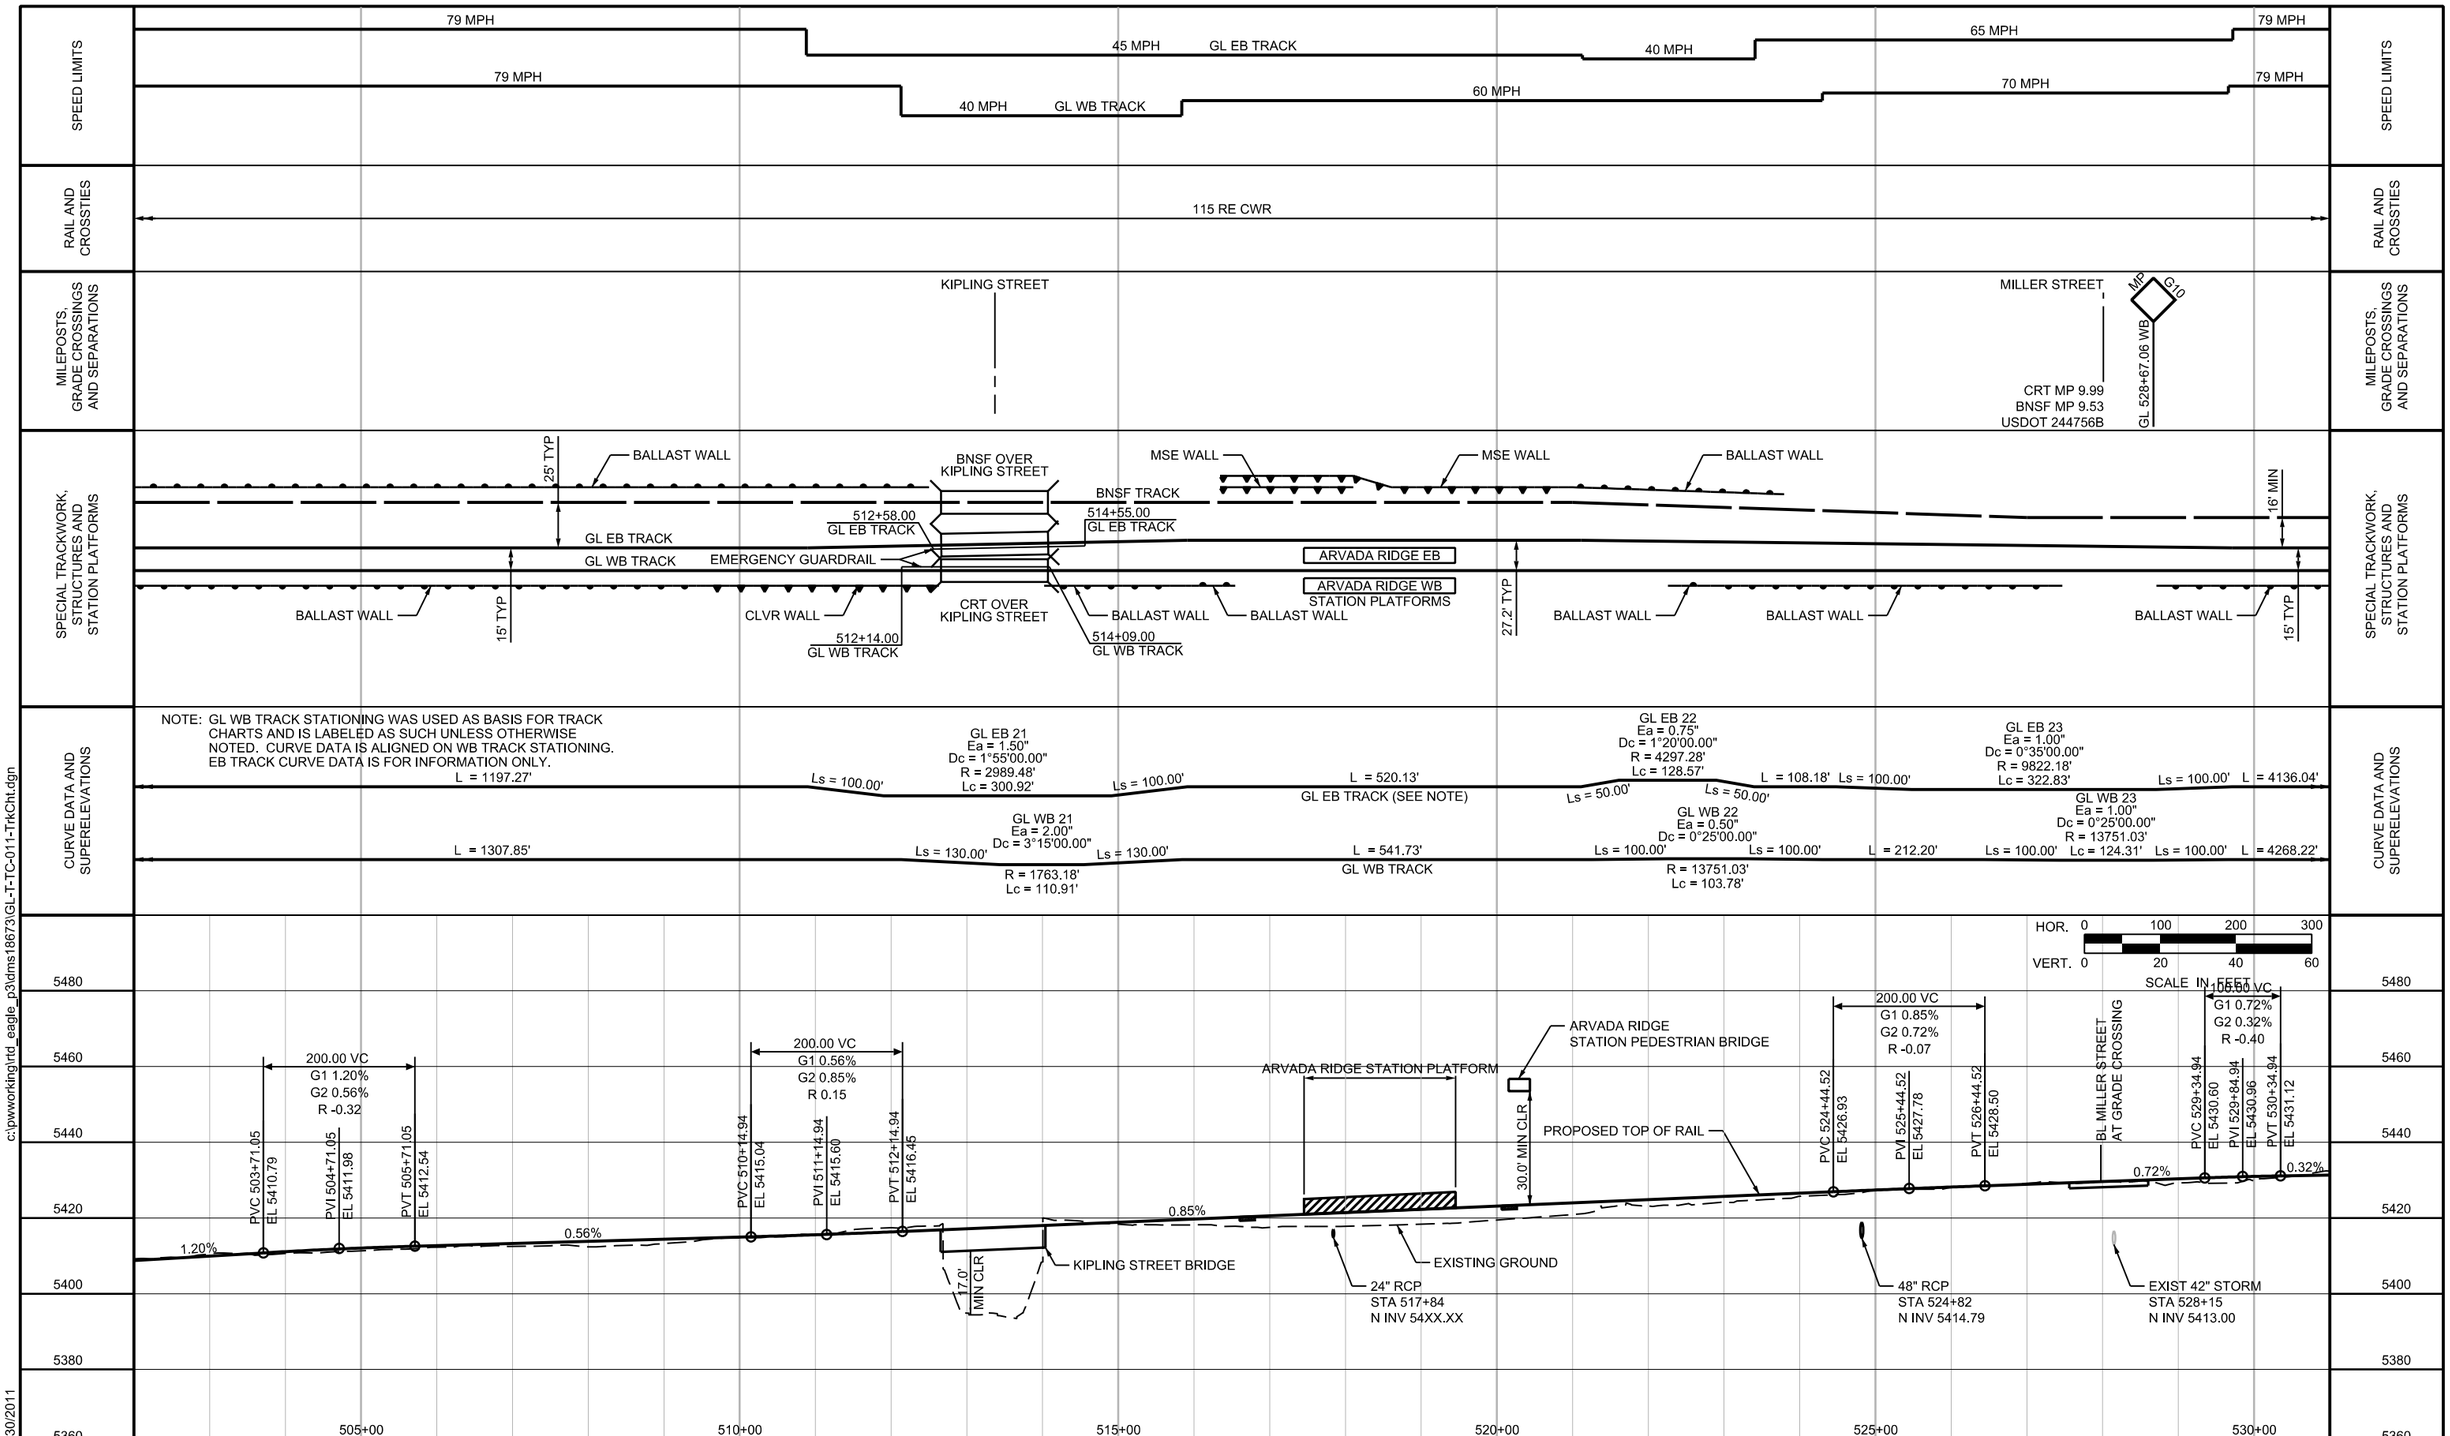

c:\pwworking\rtd_eagle_p3\dms18673\GL-T-TC-011-TrkCht.dgn

6/30/2011

USER: icrowe

NO.	REVISIONS	BY	DATE
B	ISSUED FOR 60% SUBMITTAL, CDRL #7B-03.08-09, REV B	AD	06/30/11
A1	ISSUED FOR CONST REVIEW, CDRL #7B-03.08-09, REV A1	AD	05/23/11

DESIGNED BY: DWH/VHH DATE: 05/13/11
DRAWN BY: DWH/VHH DATE: 05/13/11
CHECKED BY: DATE:
APPROVED BY: DATE:

RTD FASTTRACKS
eagle P3
FLUOR HDR GLOBAL DESIGN CONSULTANTS
DENVER TRANSIT PARTNERS

GOLD LINE

TRACK CHARTS
STA 502+00 TO STA 531+00

SHEET REFERENCE NUMBER:
TC-011

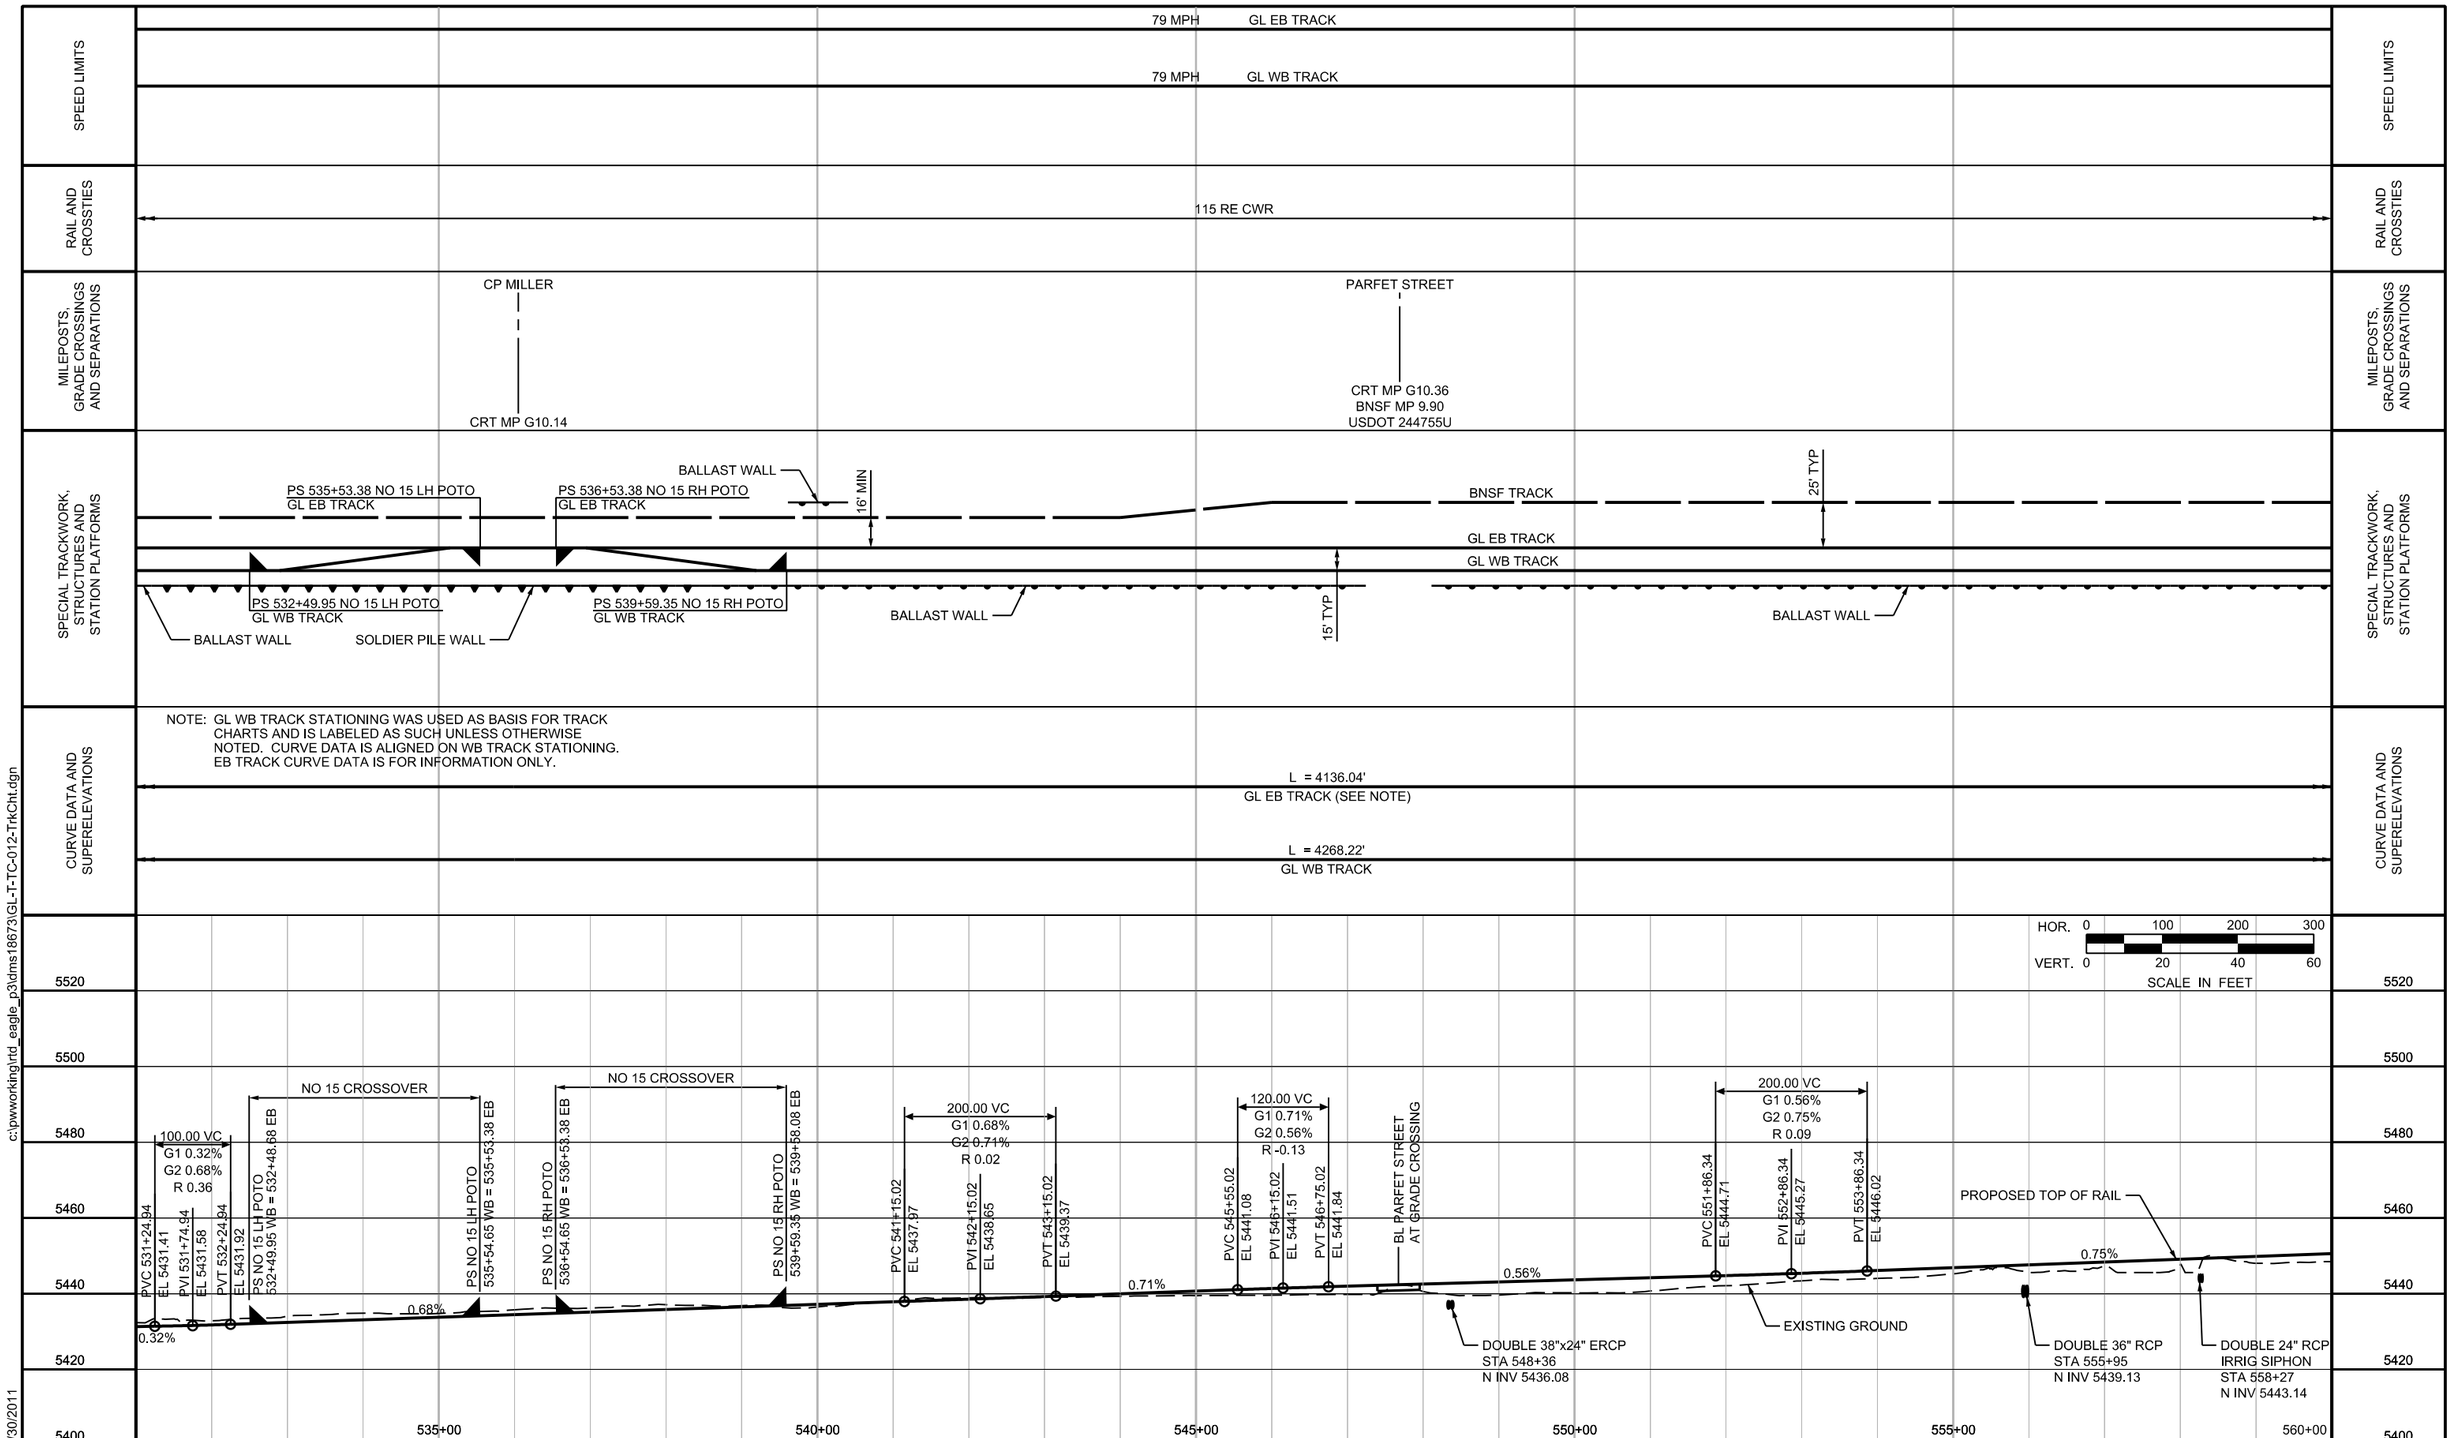

NO.	REVISIONS	BY	DATE
B	ISSUED FOR 60% SUBMITTAL, CDRL #7B-03.09, REV B	AD	06/22/11
A1	ISSUED FOR CONST REVIEW, CDRL #7B-03.07, REV A1	AD	05/23/11

DESIGNED BY: DWH/VHH DATE: 05/13/11
DRAWN BY: DWH/VHH DATE: 05/13/11
CHECKED BY: DATE:
APPROVED BY: DATE:

RTD FASTRACKS
eagle P3
FLUOR HDR GLOBAL DESIGN CONSULTANTS
DENVER TRANSIT PARTNERS

GOLD LINE

TRACK CHARTS
STA 531+00 TO STA 560+00

SHEET REFERENCE NUMBER: TC-012

c:\pwworking\rtd_eagle_p3\dms18673\GL-T-TC-012-TrkCht.dgn
6/30/2011
USER: icrowe

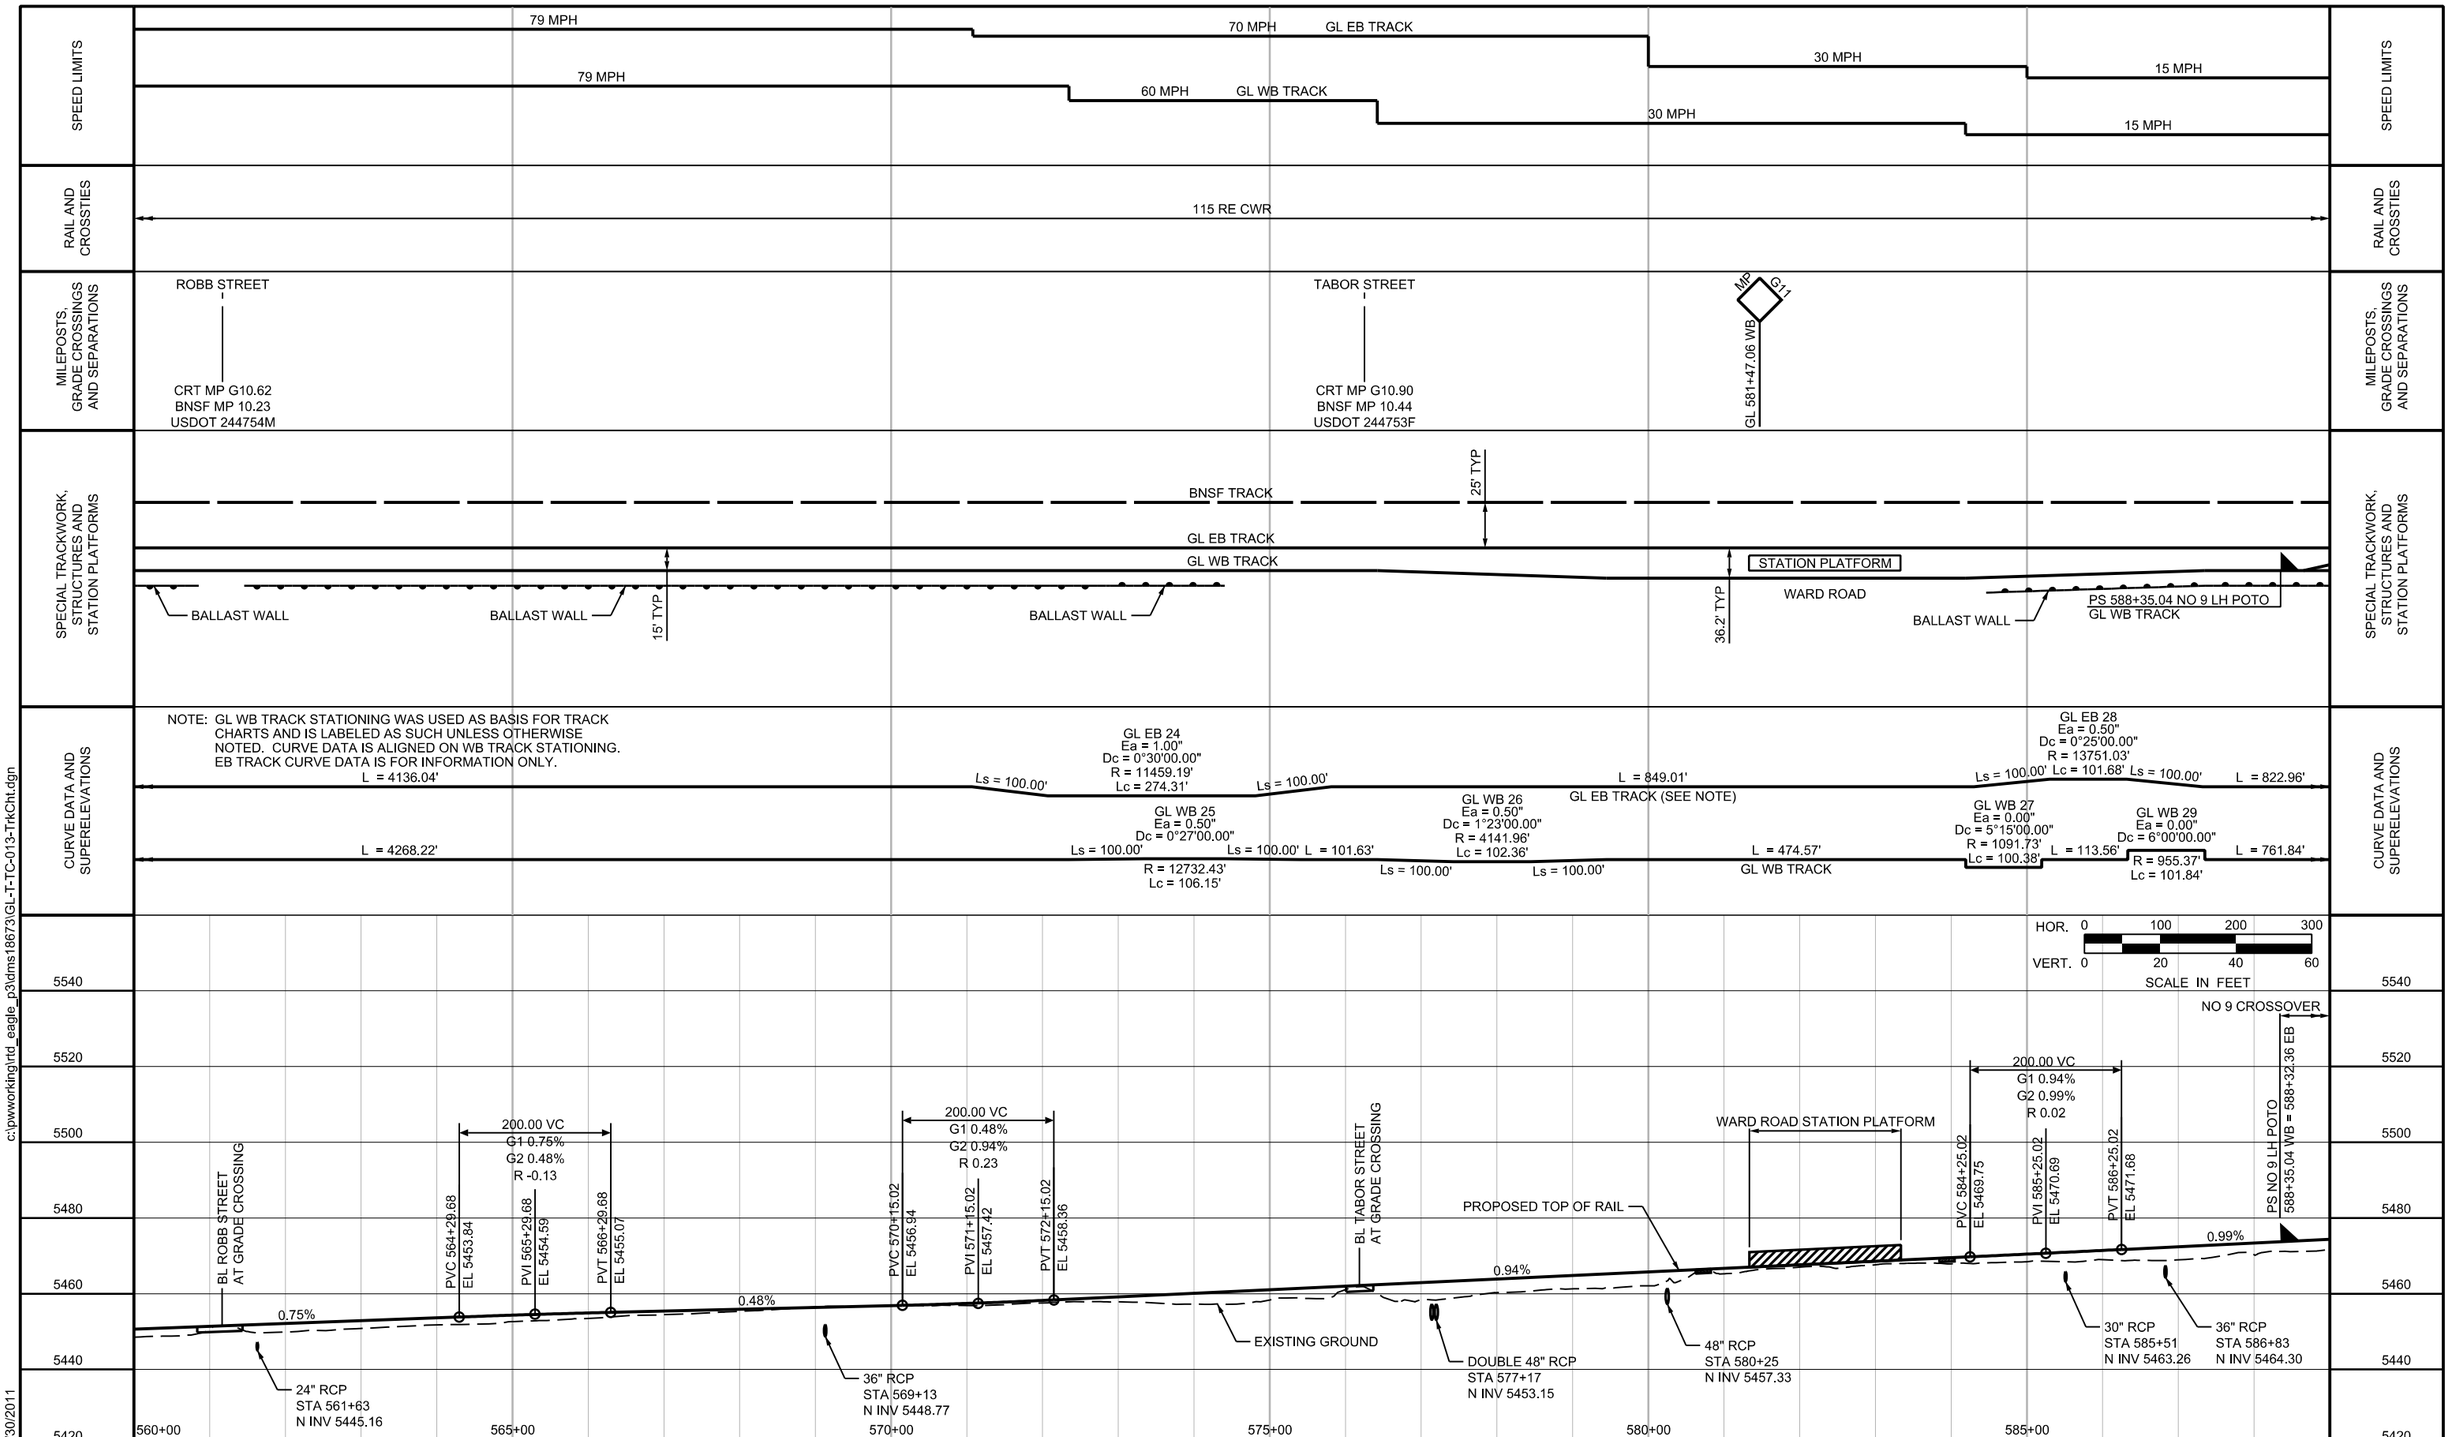

c:\pwworking\rtd_eagle_p3\dms18673\GL-T-TC-013-TrkCht.dgn

6/30/2011

USER: icrowe

NO.	REVISIONS	BY	DATE
B	ISSUED FOR 60% SUBMITTAL, CDRL #7B-03.09, REV B	AD	06/22/11
A1	ISSUED FOR CONST REVIEW, CDRL #7B-03.07, REV A1	AD	05/23/11

DESIGNED BY: DWH/VHH DATE: 05/13/11
DRAWN BY: DWH/VHH DATE: 05/13/11
CHECKED BY: DATE:
APPROVED BY: DATE:

RTD FASTTRACKS
eagle P3
FLUOR HDR GLOBAL DESIGN CONSULTANTS
DENVER TRANSIT PARTNERS

GOLD LINE

TRACK CHARTS
STA 560+00 TO STA 589+00

SHEET REFERENCE NUMBER:
TC-013

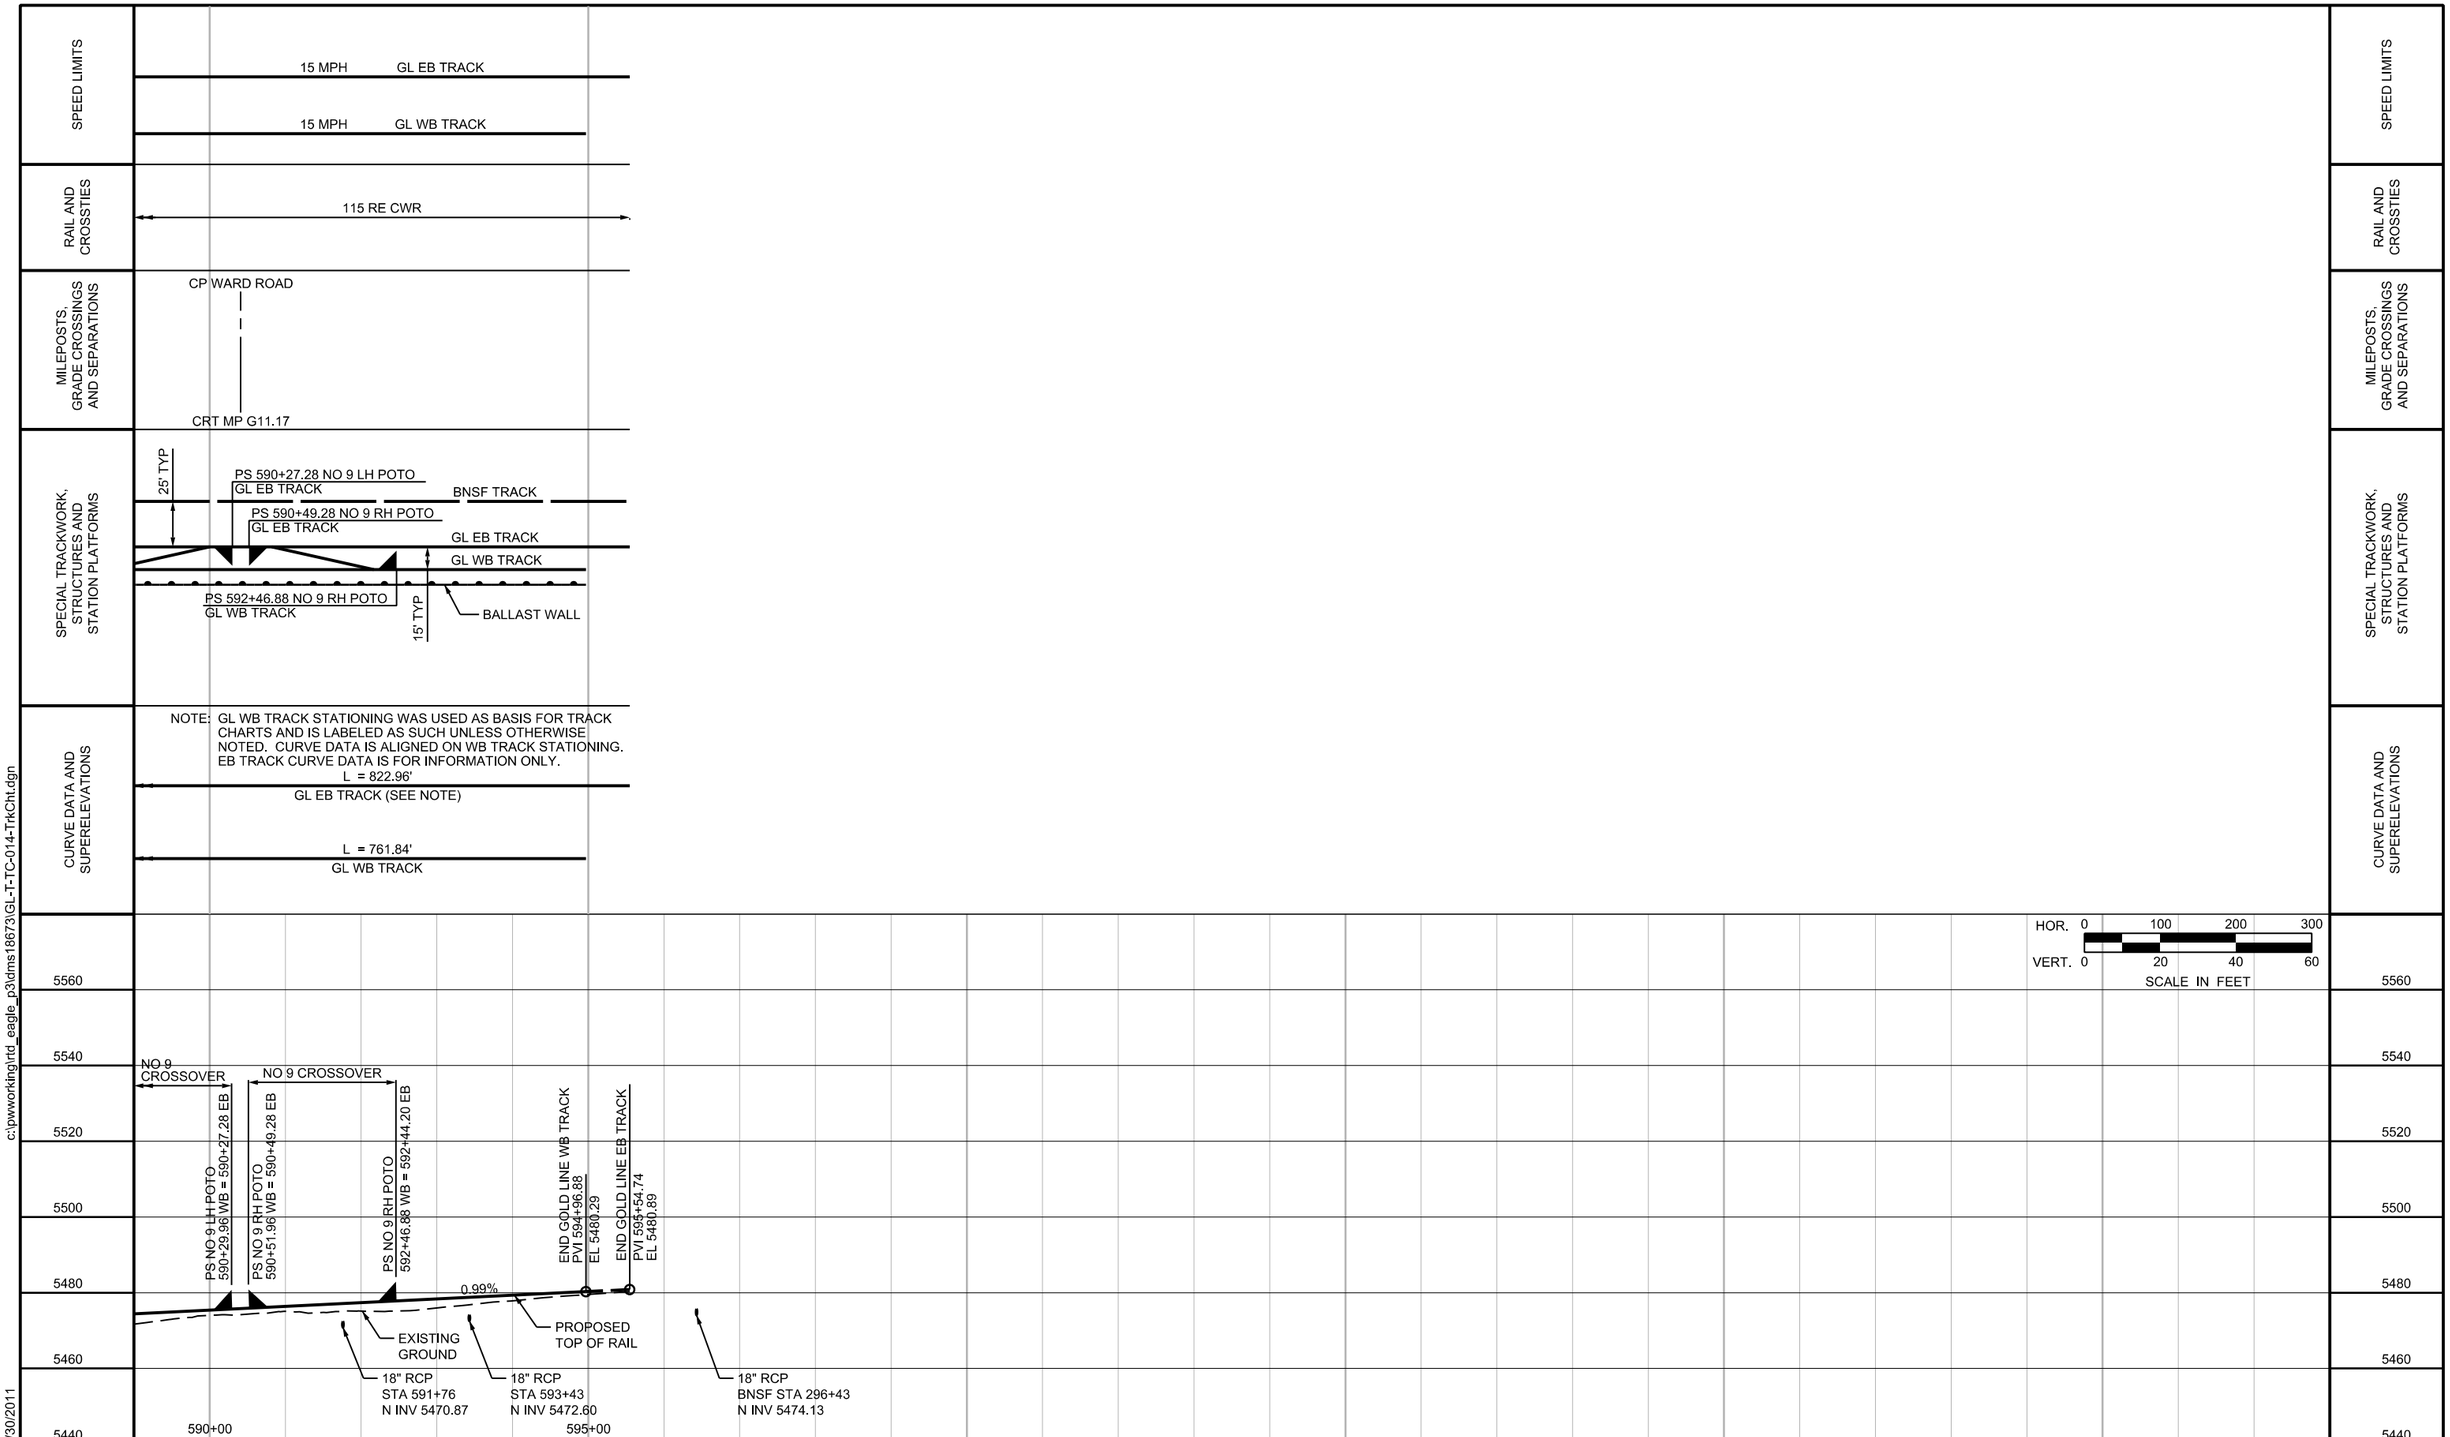

NO.	REVISIONS	BY	DATE
B	ISSUED FOR 60% SUBMITTAL, CDRL #7B-03.09, REV B	AD	06/22/11
A1	ISSUED FOR CONST REVIEW, CDRL #7B-03.07, REV A1	AD	05/23/11

DESIGNED BY: DWH/VHH DATE: 05/13/11
DRAWN BY: DWH/VHH DATE: 05/13/11
CHECKED BY: DATE:
APPROVED BY: DATE:

RTD FASTTRACKS eagle P3 FLUOR HDR GLOBAL DESIGN CONSULTANTS

DENVER TRANSIT PARTNERS

GOLD LINE

TRACK CHARTS
STA 589+00 TO STA 594+96.88

SHEET REFERENCE NUMBER: TC-014

c:\pwworking\rtd_eagle_p3\dms18673\GL-T-TC-014-TrkCht.dgn
6/30/2011
USER: icrowe