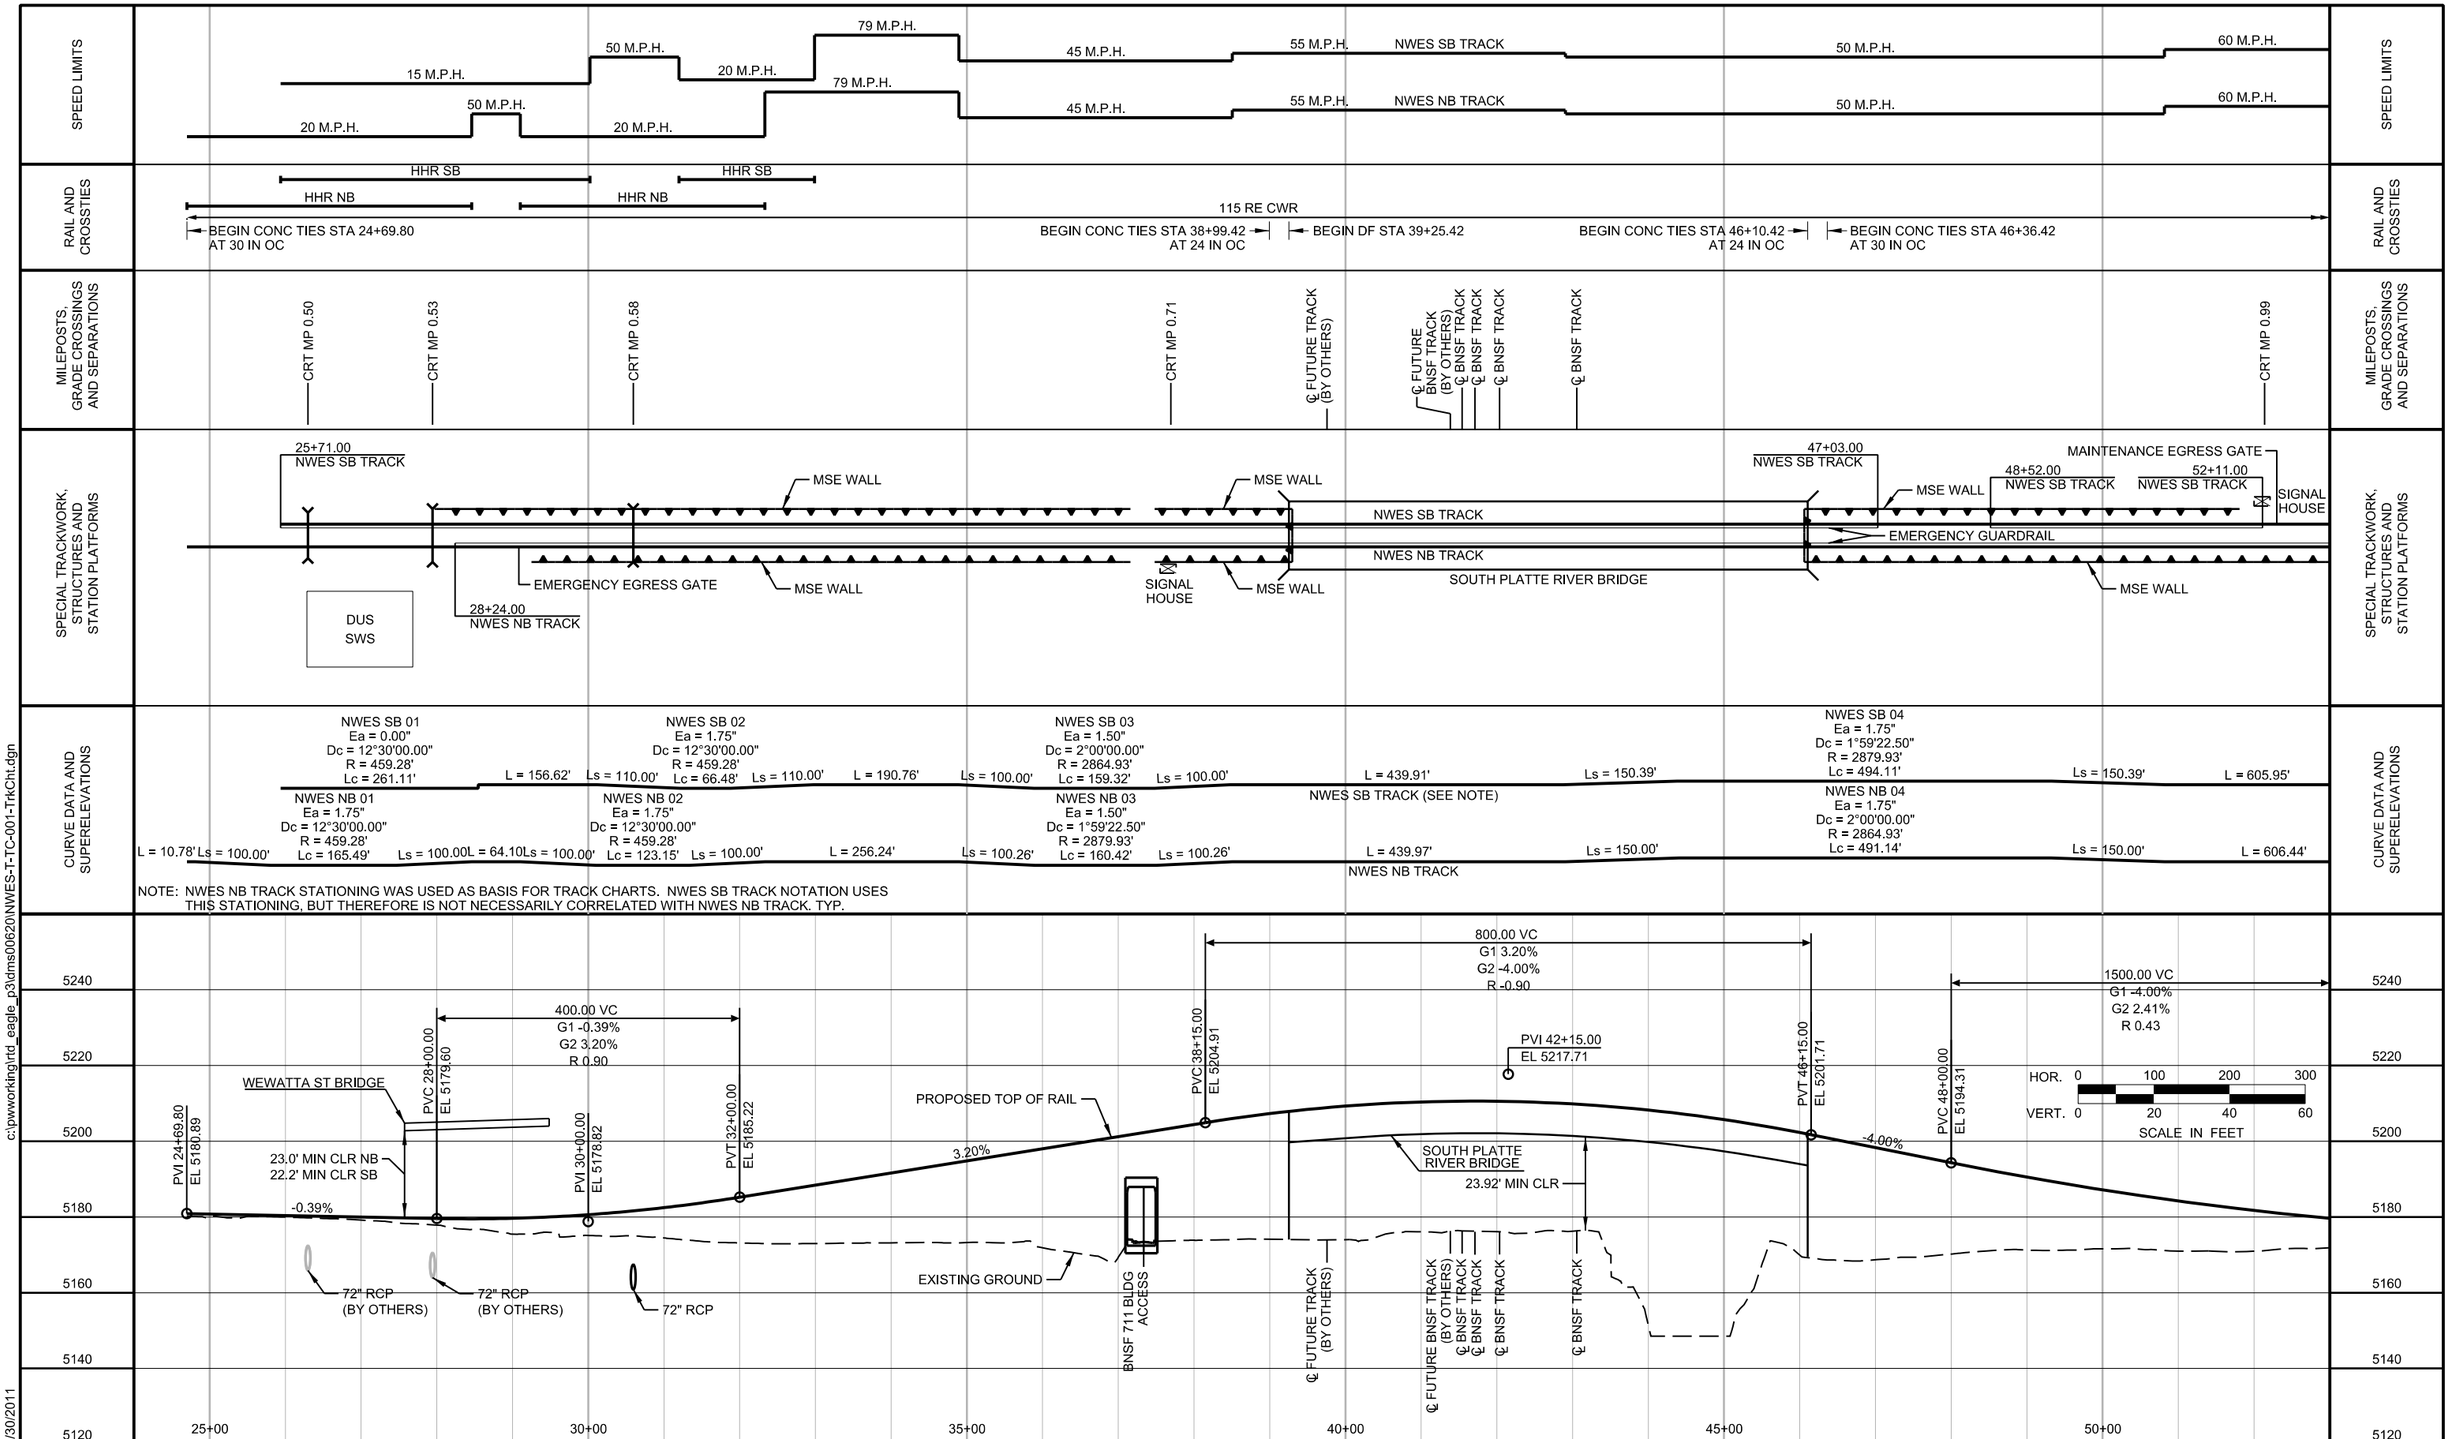

NO.	REVISIONS	BY	DATE
D	ISSUED FOR 100% SUBMITTAL, CDRL #7B-03.04, REV D	IMWC	05/23/11
B1	ISSUED FOR BNSF REVIEW, CDRL #7B-03.04, REV B1	IMWC	03/28/11
B	ISSUED FOR 60% SUBMITTAL, CDRL #7B-03.04, REV B	IMWC	02/21/11

DESIGNED BY: IMWC DATE: 01/20/11
DRAWN BY: DTO DATE: 02/01/11
CHECKED BY: DATE:
APPROVED BY: DATE:

RTD FASTTRACKS eagle P3 FLUOR HDR GLOBAL DESIGN CONSULTANTS ATKINS DENVER TRANSIT PARTNERS

NORTHWEST RAIL ELECTRIFIED SEGMENT

TRACK CHARTS
STA 24+70 TO STA 53+00

SHEET REFERENCE NUMBER: TC-001

c:\pwworking\rtd_eagle_p3\dms00620\NWES-T-TC-001-TrkCht.dgn
6/30/2011
USER: icrowe

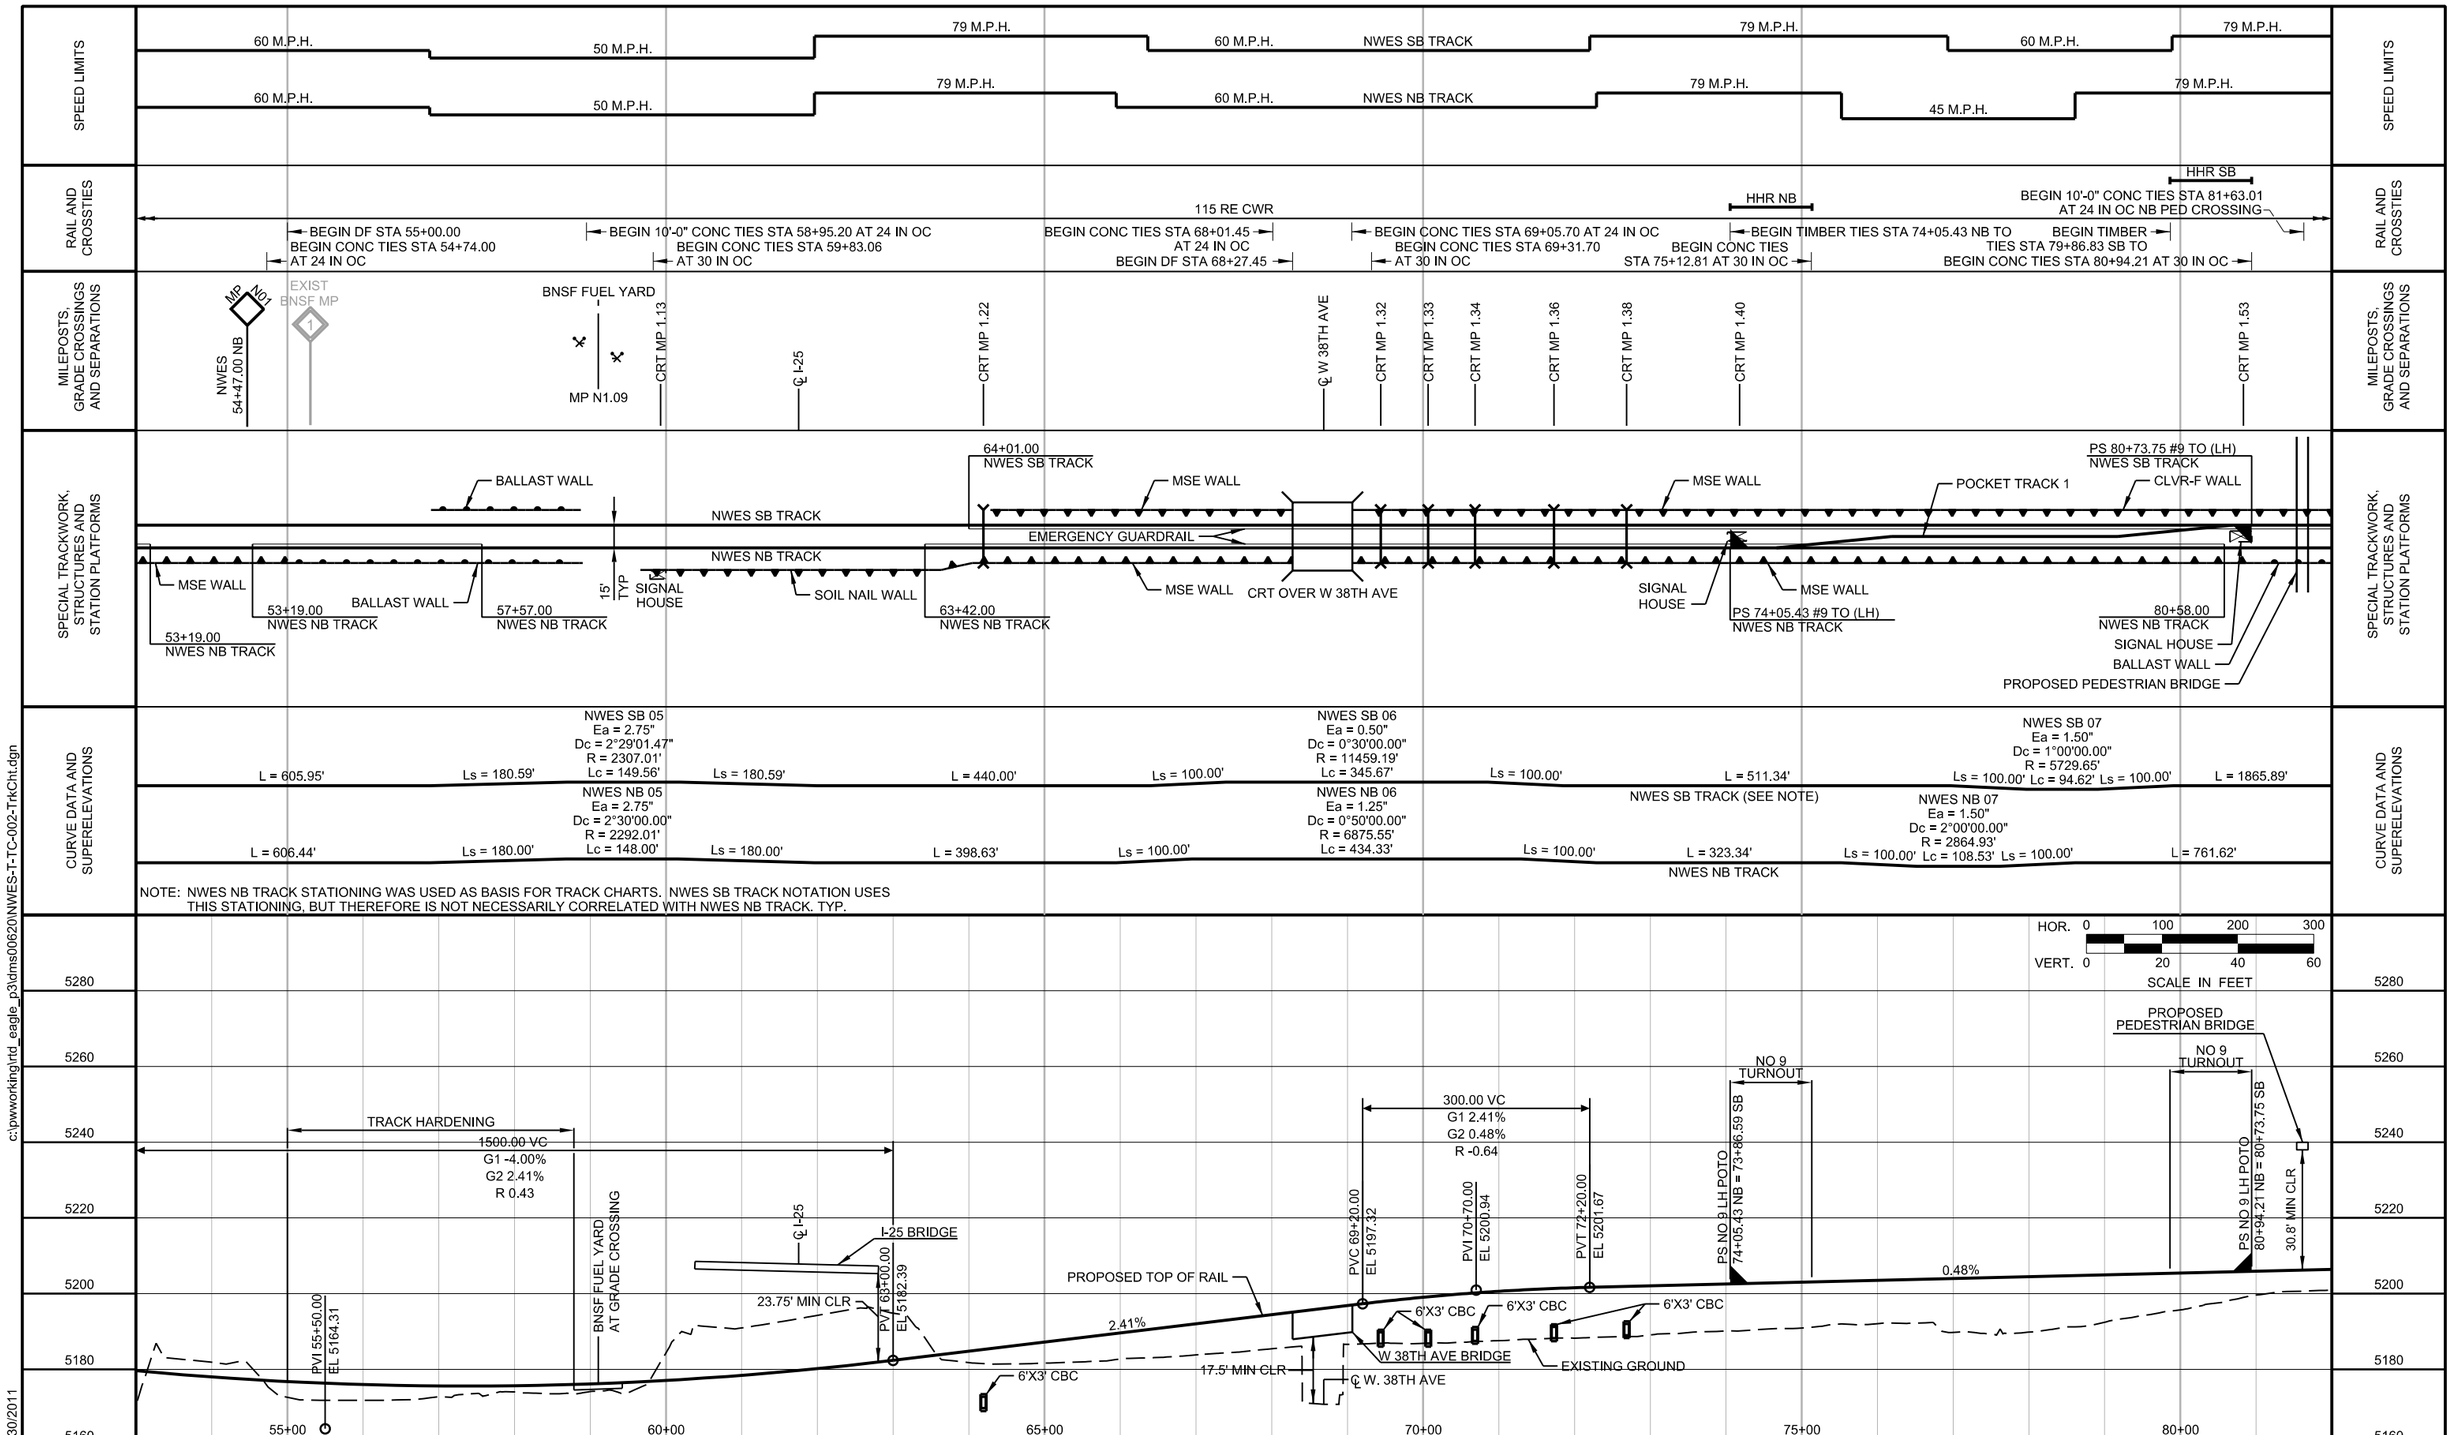

c:\pwworking\rtd_eagle_p3\dms00620\NWES-T-TC-002-TrkCht.dgn

6/30/2011

USER: icrowe

NO.	REVISIONS	BY	DATE
D	ISSUED FOR 100% SUBMITTAL, CDRL #7B-03.04, REV D	IMWC	05/23/11
B1	ISSUED FOR BNSF REVIEW, CDRL #7B-03.04, REV B1	IMWC	03/28/11
B	ISSUED FOR 60% SUBMITTAL, CDRL #7B-03.04, REV B	IMWC	02/21/11

DESIGNED BY: IMWC DATE: 01/20/11
DRAWN BY: DTO DATE: 02/01/11
CHECKED BY: DATE:
APPROVED BY: DATE:

RTD FASTRACKS eagle P3 FLUOR HDR GLOBAL DESIGN CONSULTANTS ATKINS DENVER TRANSIT PARTNERS

NORTHWEST RAIL ELECTRIFIED SEGMENT

TRACK CHARTS
STA 53+00 TO STA 82+00

SHEET REFERENCE NUMBER: TC-002

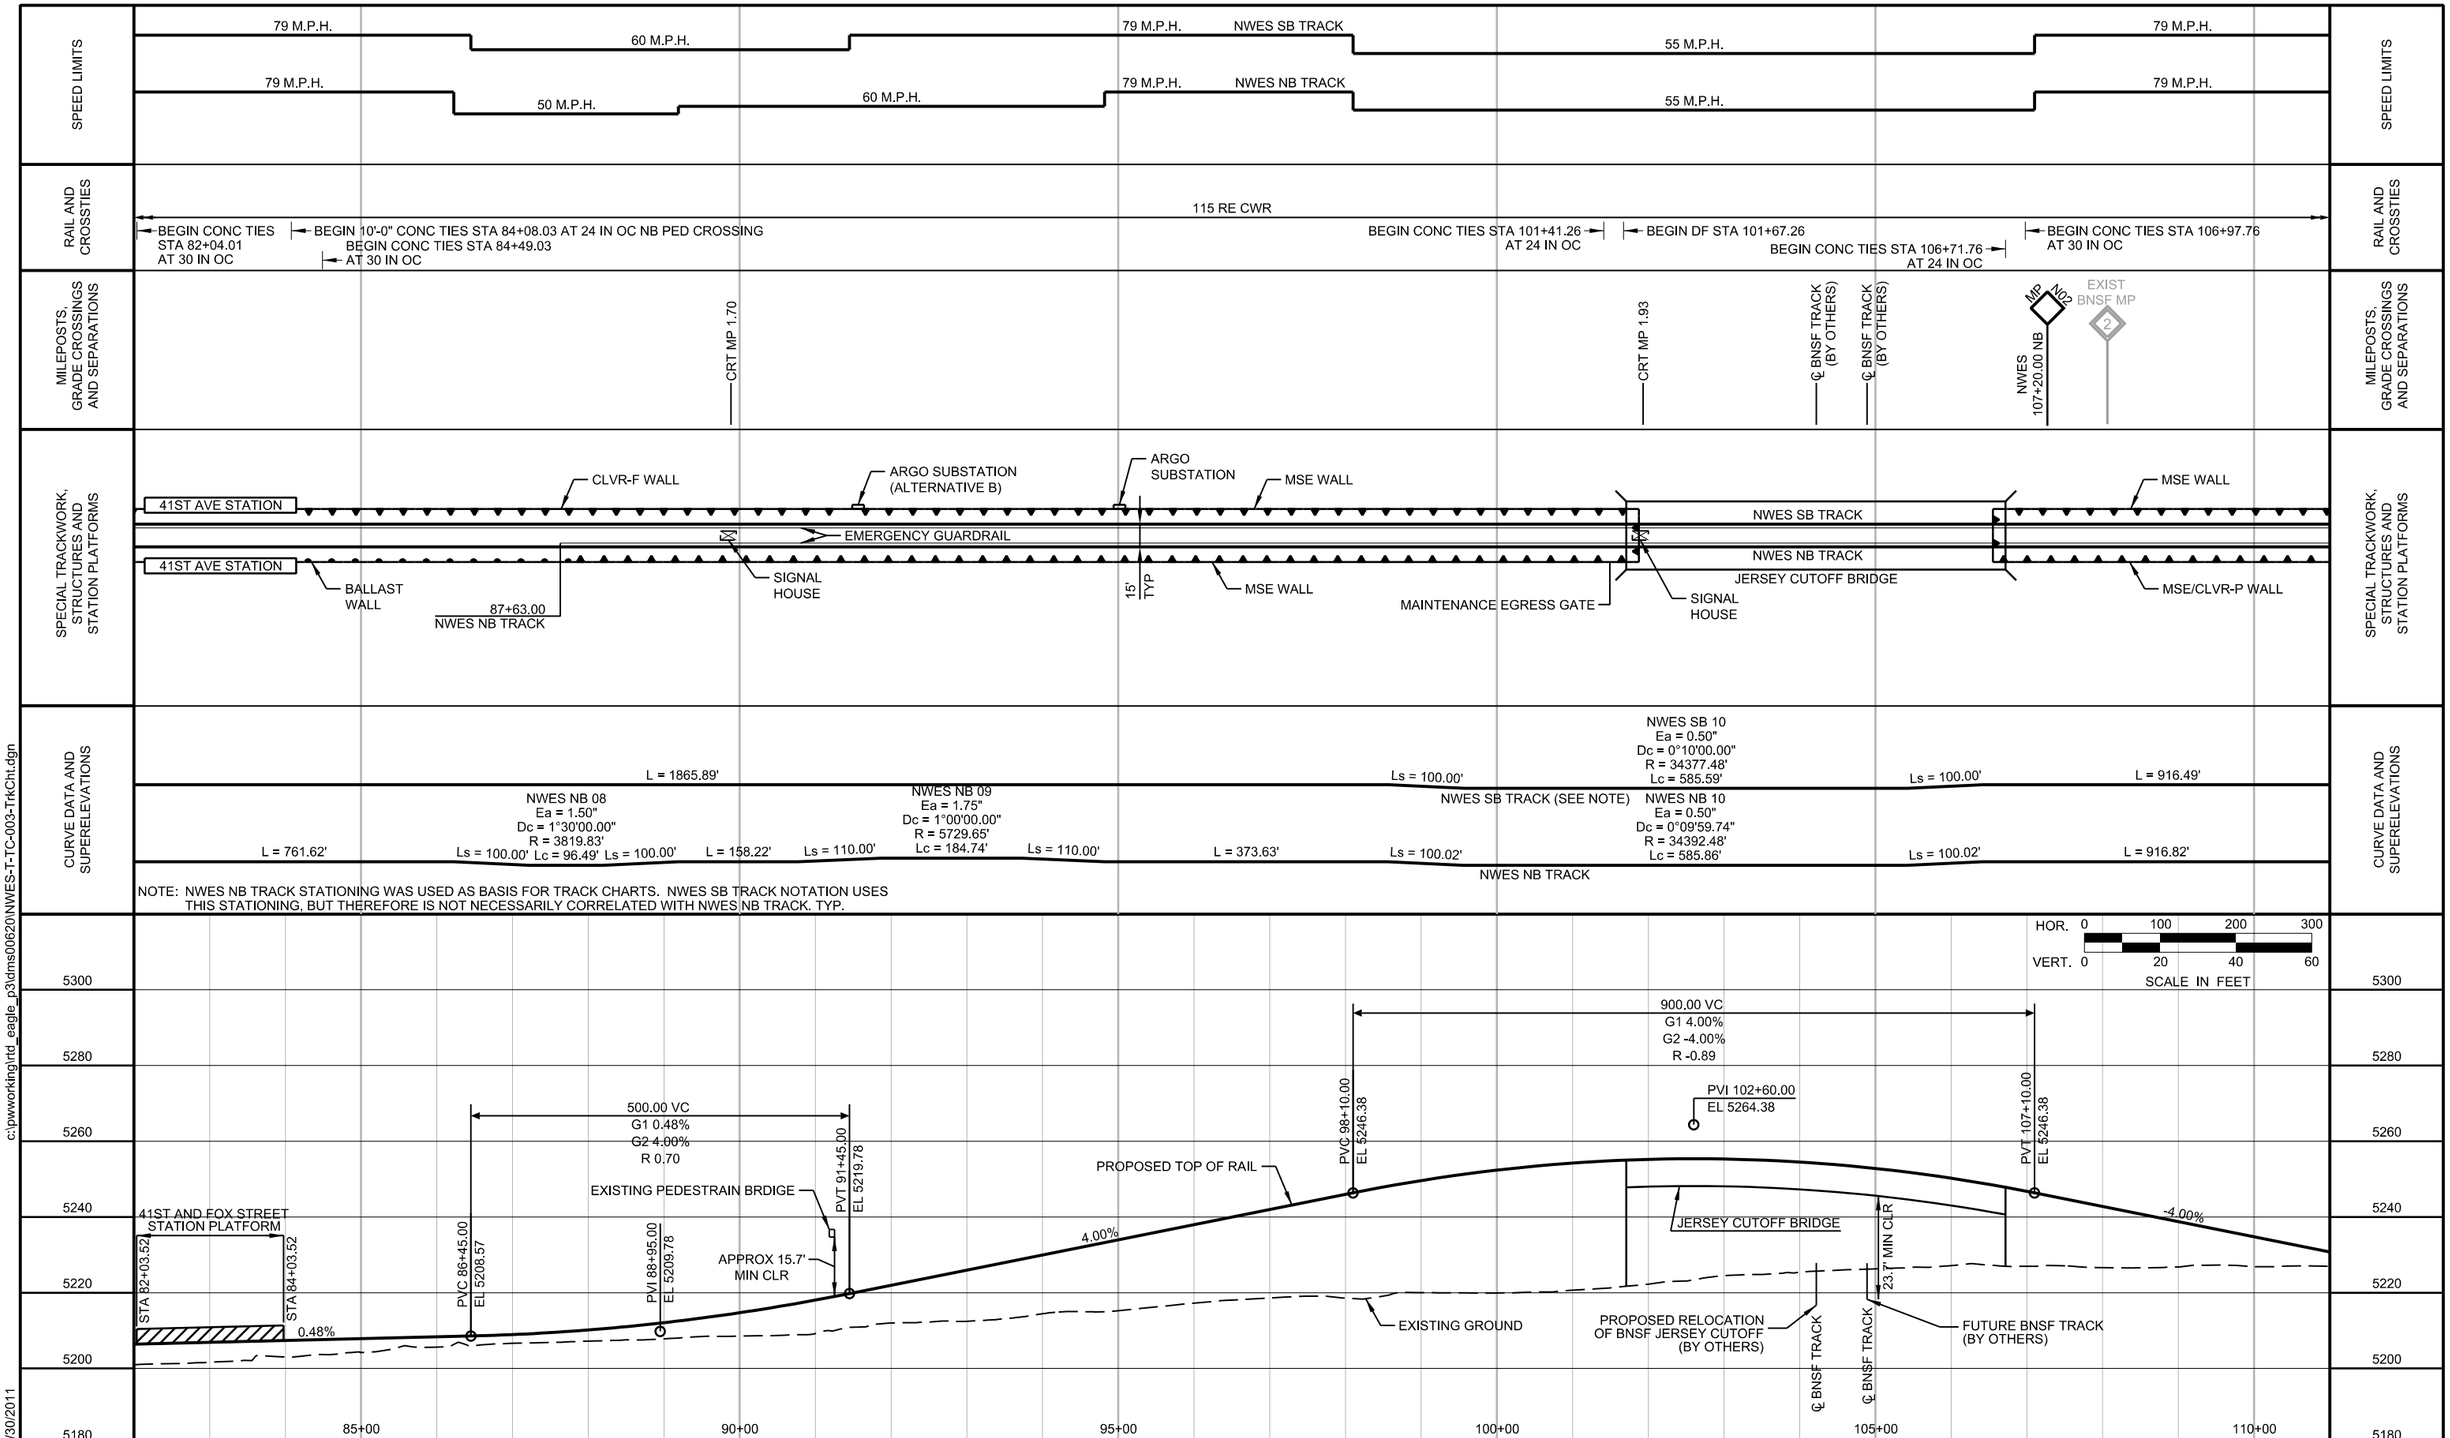

NO.	REVISIONS	BY	DATE
D	ISSUED FOR 100% SUBMITTAL, CDRL #7B-03.04, REV D	IMWC	05/23/11
B1	ISSUED FOR BNSF REVIEW, CDRL #7B-03.04, REV B1	IMWC	03/28/11
B	ISSUED FOR 60% SUBMITTAL, CDRL #7B-03.04, REV B	IMWC	02/21/11

DESIGNED BY: IMWC DATE: 01/20/11
DRAWN BY: DTO DATE: 02/01/11
CHECKED BY: DATE:
APPROVED BY: DATE:

RTD FASTRACKS eagle P3 — FLUOR HDR GLOBAL DESIGN CONSULTANTS — ATKINS — DENVER TRANSIT PARTNERS

NORTHWEST RAIL ELECTRIFIED SEGMENT

TRACK CHARTS
STA 82+00 TO STA 111+00

SHEET REFERENCE NUMBER: TC-003

c:\pwworking\rtd_eagle_p3\dms00620\NWES-T-TC-003-TrkCht.dgn
6/30/2011
USER: icrowe

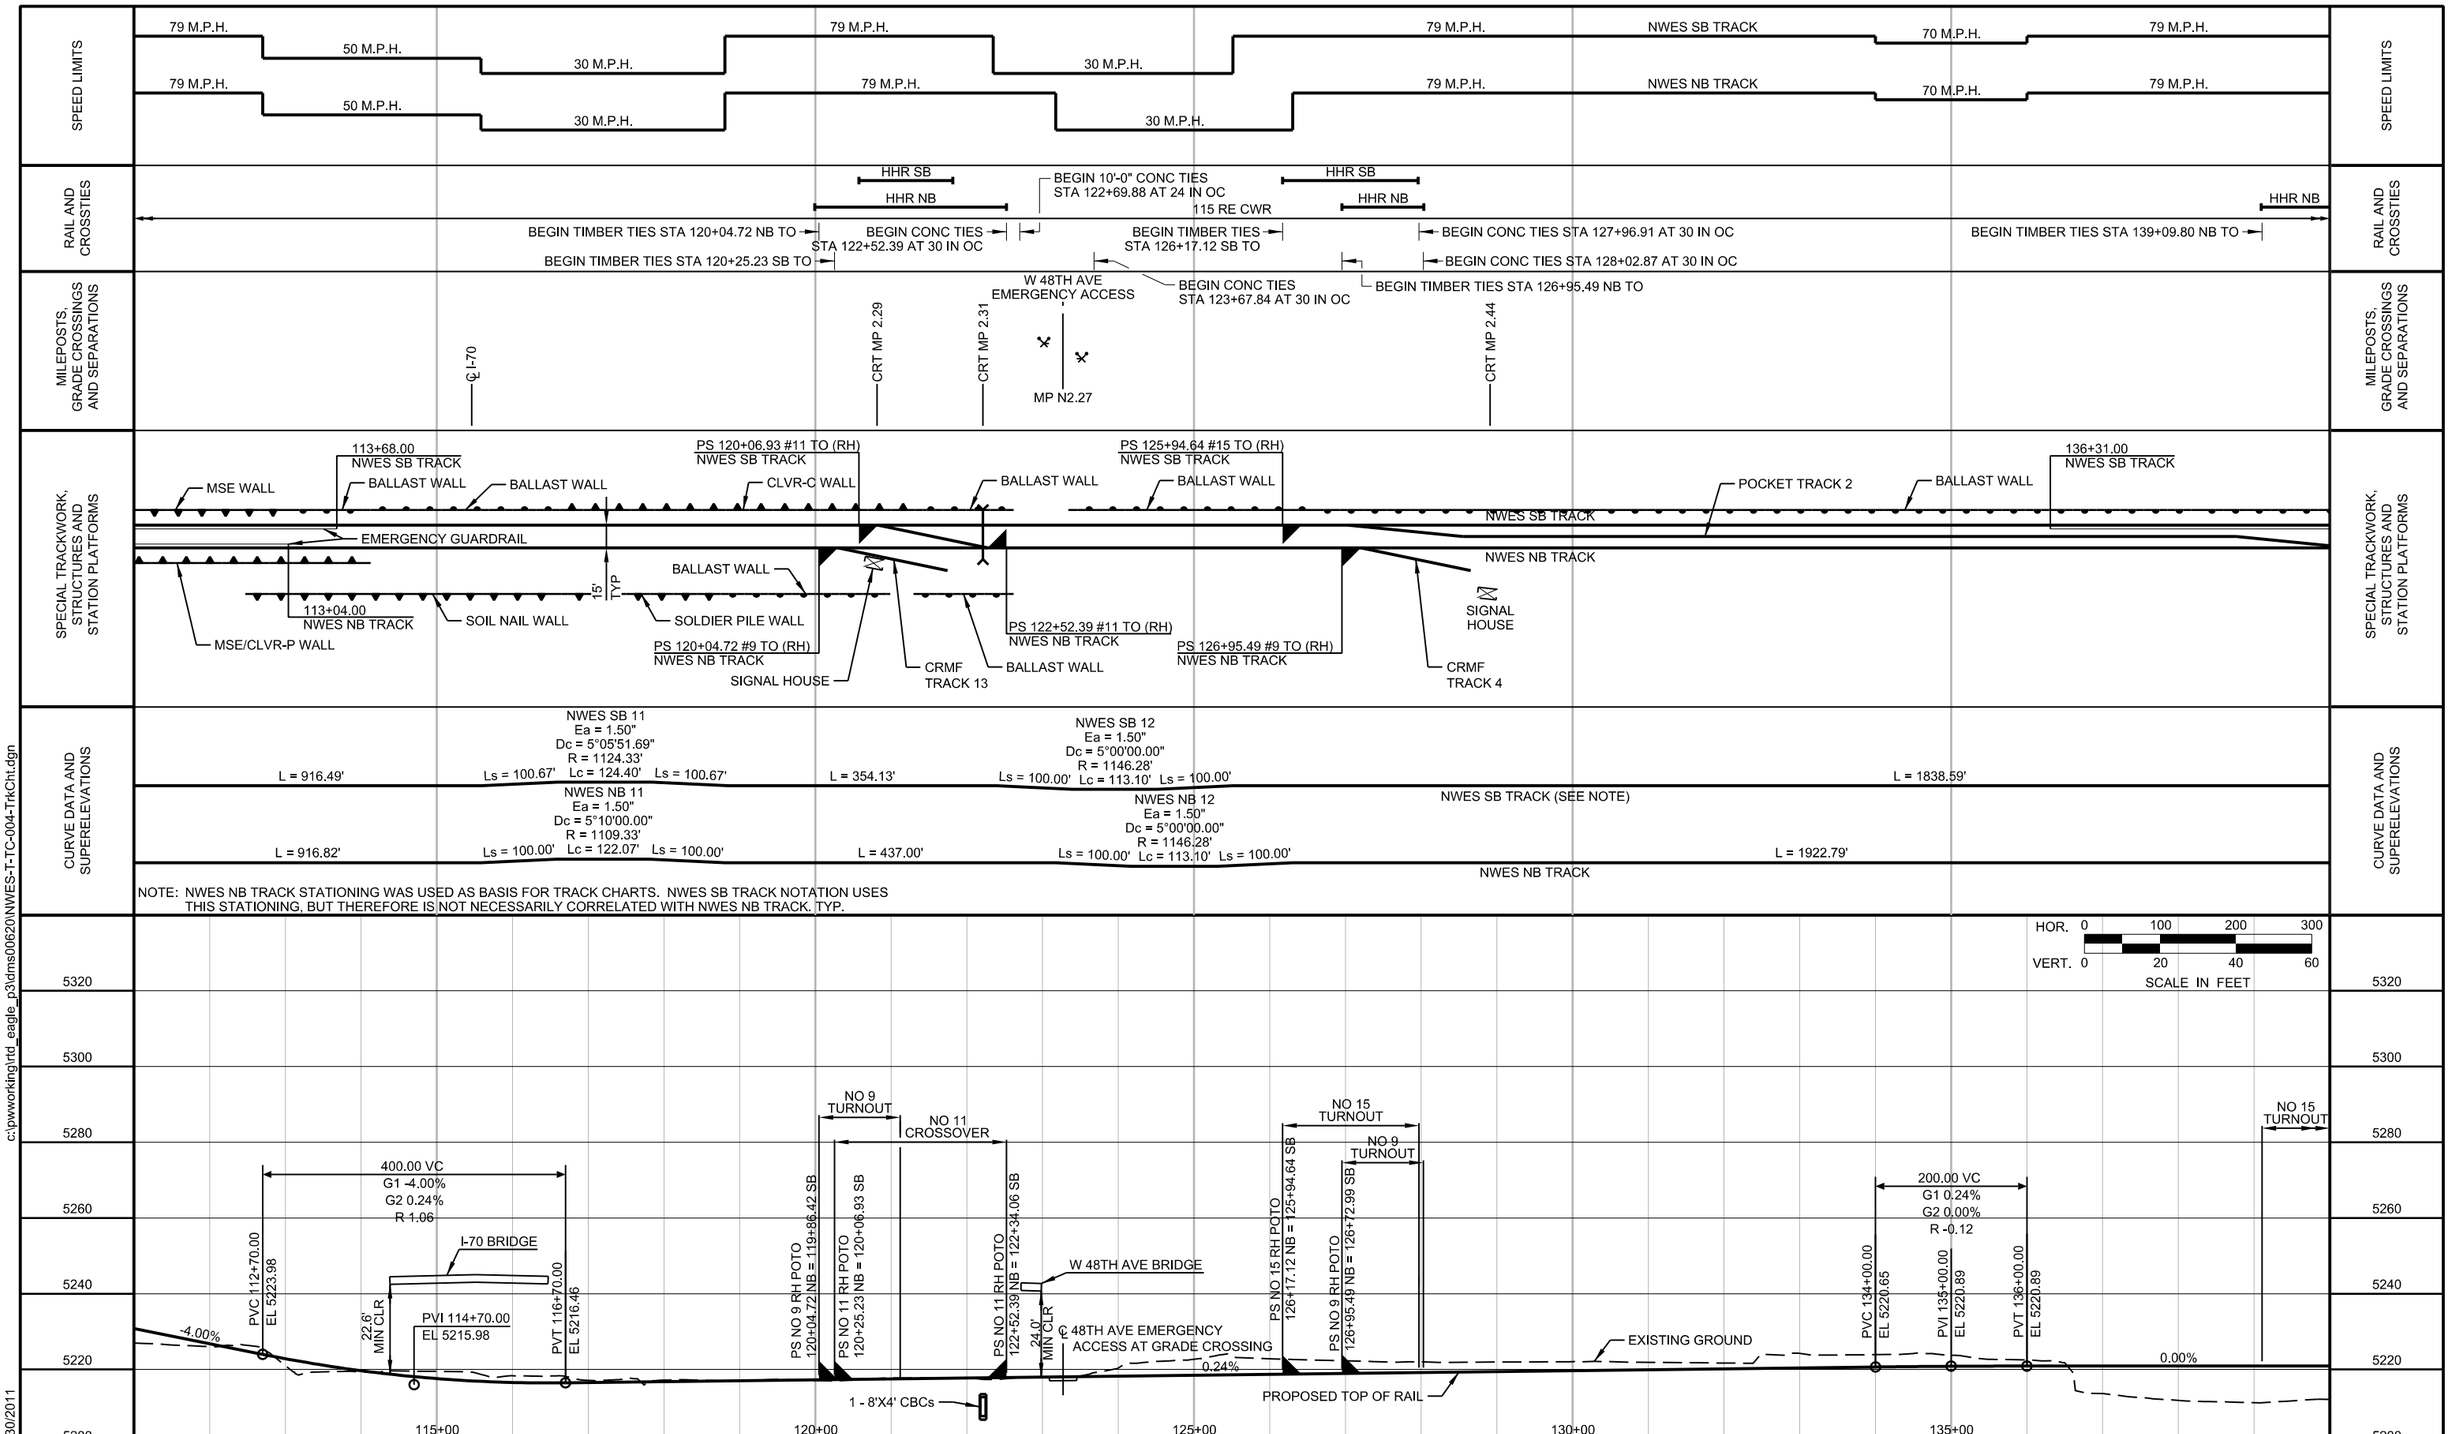

c:\pwworking\rtd_eagle_p3\dms00620\NWES-T-TC-004-TrkCht.dgn

6/30/2011

USER: icrowe

NO.	REVISIONS	BY	DATE
D	ISSUED FOR 100% SUBMITTAL, CDRL #7B-03.04, REV D	IMWC	05/23/11
B1	ISSUED FOR BNSF REVIEW, CDRL #7B-03.04, REV B1	IMWC	03/28/11
B	ISSUED FOR 60% SUBMITTAL, CDRL #7B-03.04, REV B	IMWC	02/21/11

DESIGNED BY: IMWC DATE: 01/20/11
DRAWN BY: DTO DATE: 02/01/11
CHECKED BY: DATE:
APPROVED BY: DATE:

RTD FASTRACKS eagle P3 — FLUOR HDR GLOBAL DESIGN CONSULTANTS — ATKINS — DENVER TRANSIT PARTNERS

NORTHWEST RAIL ELECTRIFIED SEGMENT

TRACK CHARTS
STA 111+00 TO STA 140+00

SHEET REFERENCE NUMBER: TC-004

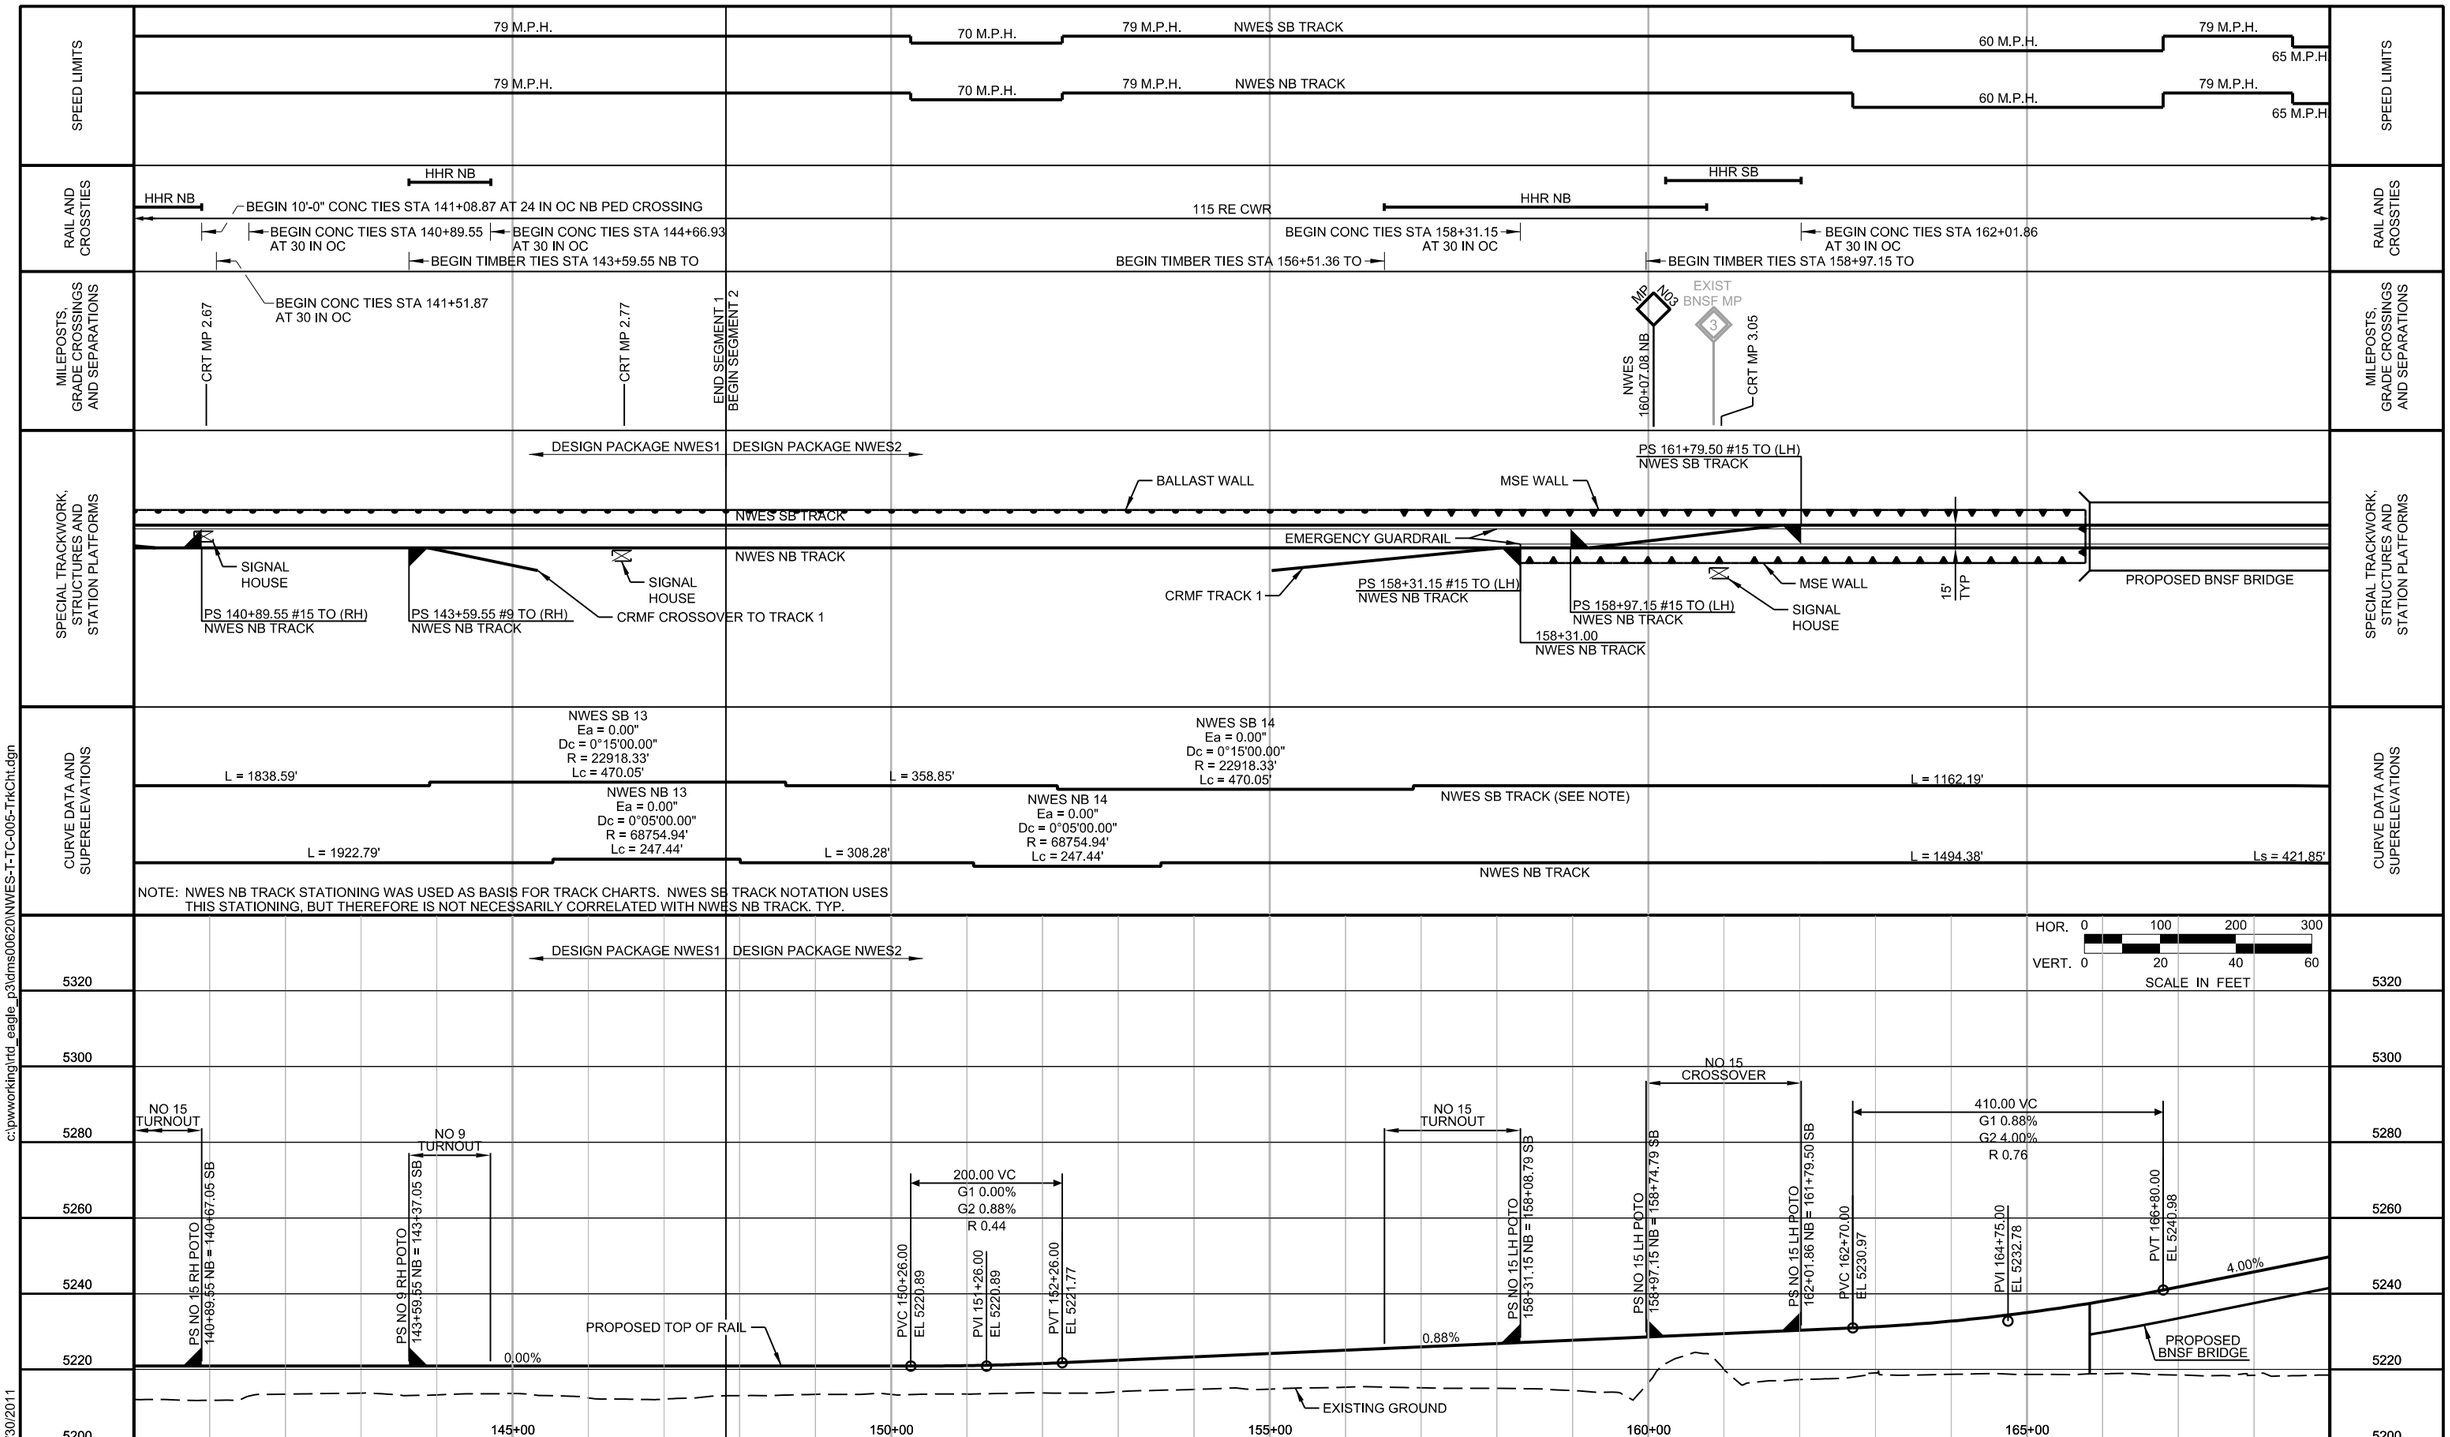

c:\pwworking\rtd_eagle_p3\dms00620\NWES-T-TC-005-TrkCht.dgn

6/30/2011

USER: icrowe

NO.	REVISIONS	BY	DATE
D	ISSUED FOR 100% SUBMITTAL, CDRL #7B-03.04, REV D	IMWC	05/23/11
B1	ISSUED FOR BNSF REVIEW, CDRL #7B-03.04, REV B1	IMWC	03/28/11
B	ISSUED FOR 60% SUBMITTAL, CDRL #7B-03.04, REV B	IMWC	02/21/11

DESIGNED BY: IMWC DATE: 01/20/11
DRAWN BY: DTO DATE: 02/01/11
CHECKED BY: DATE:
APPROVED BY: DATE:

RTD FASTTRACKS eagle P3 FLUOR HDR GLOBAL DESIGN CONSULTANTS ATKINS DENVER TRANSIT PARTNERS

NORTHWEST RAIL ELECTRIFIED SEGMENT

TRACK CHARTS
STA 140+00 TO STA 169+00

SHEET REFERENCE NUMBER: TC-005

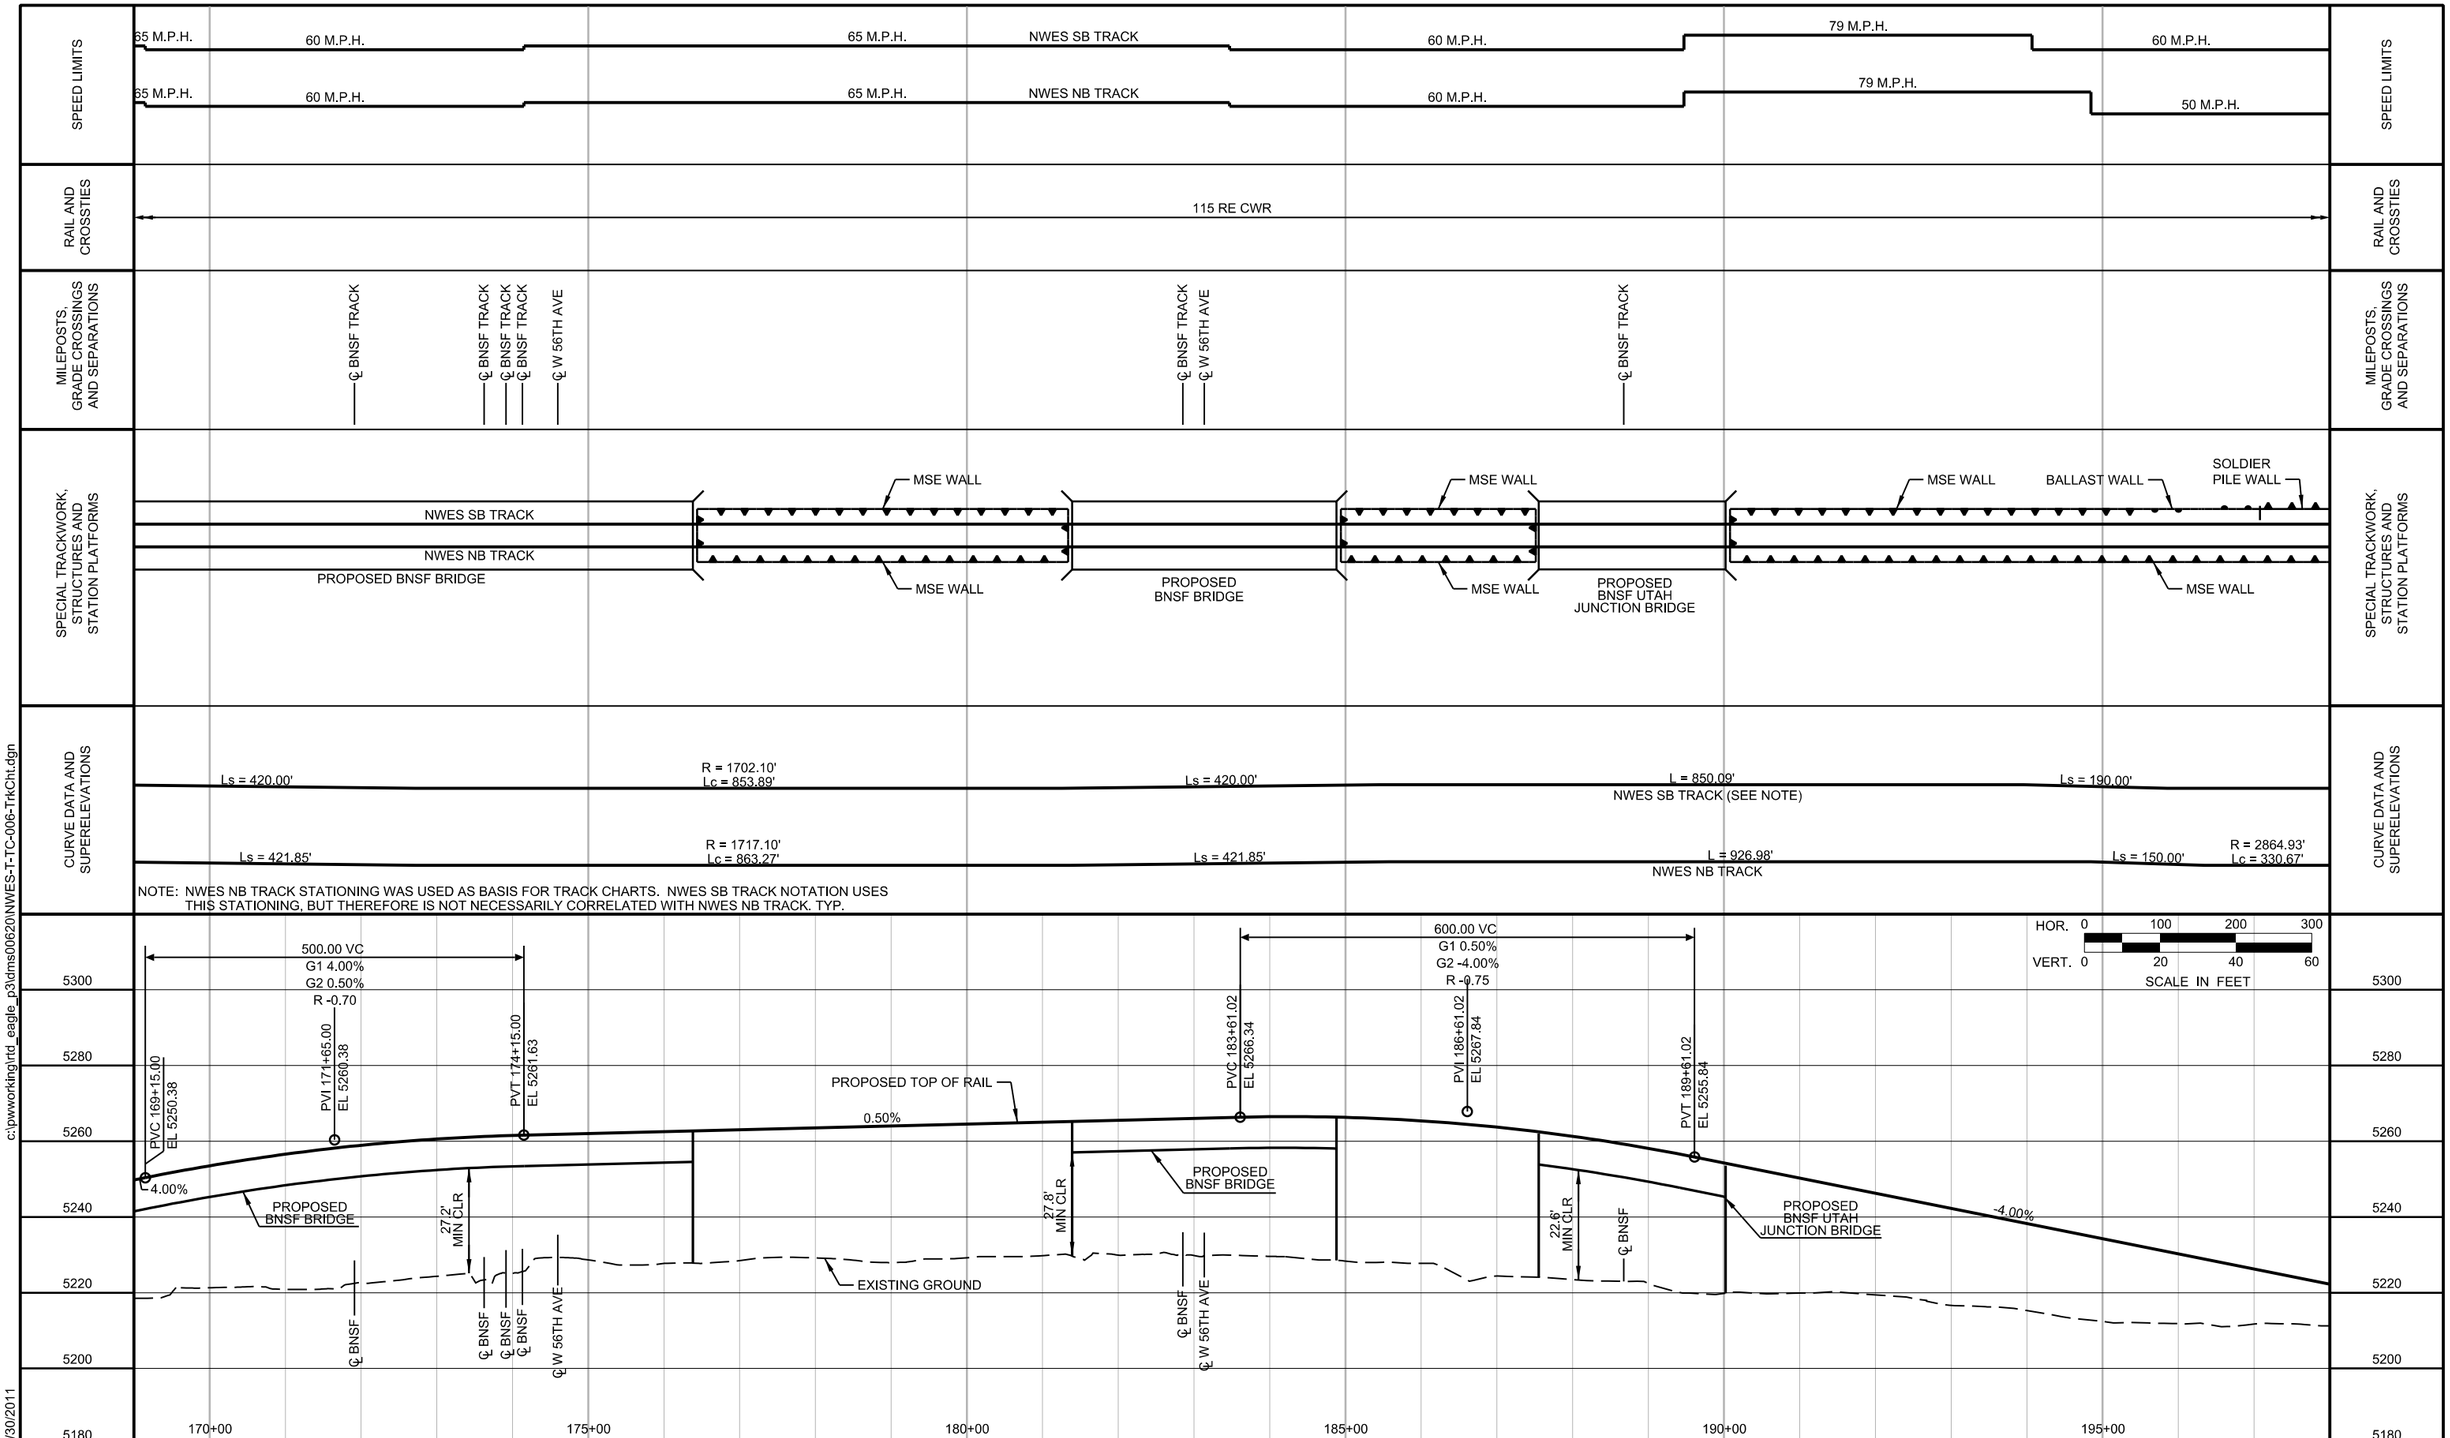

c:\pwworking\rtd_eagle_p3\dms00620\NWES-T-TC-006-TrkCht.dgn

6/30/2011

USER: icrowe

NO.	REVISIONS	BY	DATE
B	ISSUED FOR 60% SUBMITTAL, CDRL #7B-03.05, REV B	IMWC	06/22/11
A1	ISSUED FOR CONST REVIEW, CDRL #7B-03.05, REV A1	IMWC	05/27/11
A	ISSUED FOR PRE 60% PDRM, CDRL #7B-03.06, REV A	IMWC	05/03/11

DESIGNED BY: IMWC DATE: 02/28/11
DRAWN BY: DTO DATE: 02/28/11
CHECKED BY: DATE:
APPROVED BY: DATE:

RTD FASTRACKS eagle P3 FLUOR HDR GLOBAL DESIGN CONSULTANTS ATKINS DENVER TRANSIT PARTNERS

NORTHWEST RAIL ELECTRIFIED SEGMENT

TRACK CHARTS
STA 169+00 TO STA 198+00

SHEET REFERENCE NUMBER: TC-006

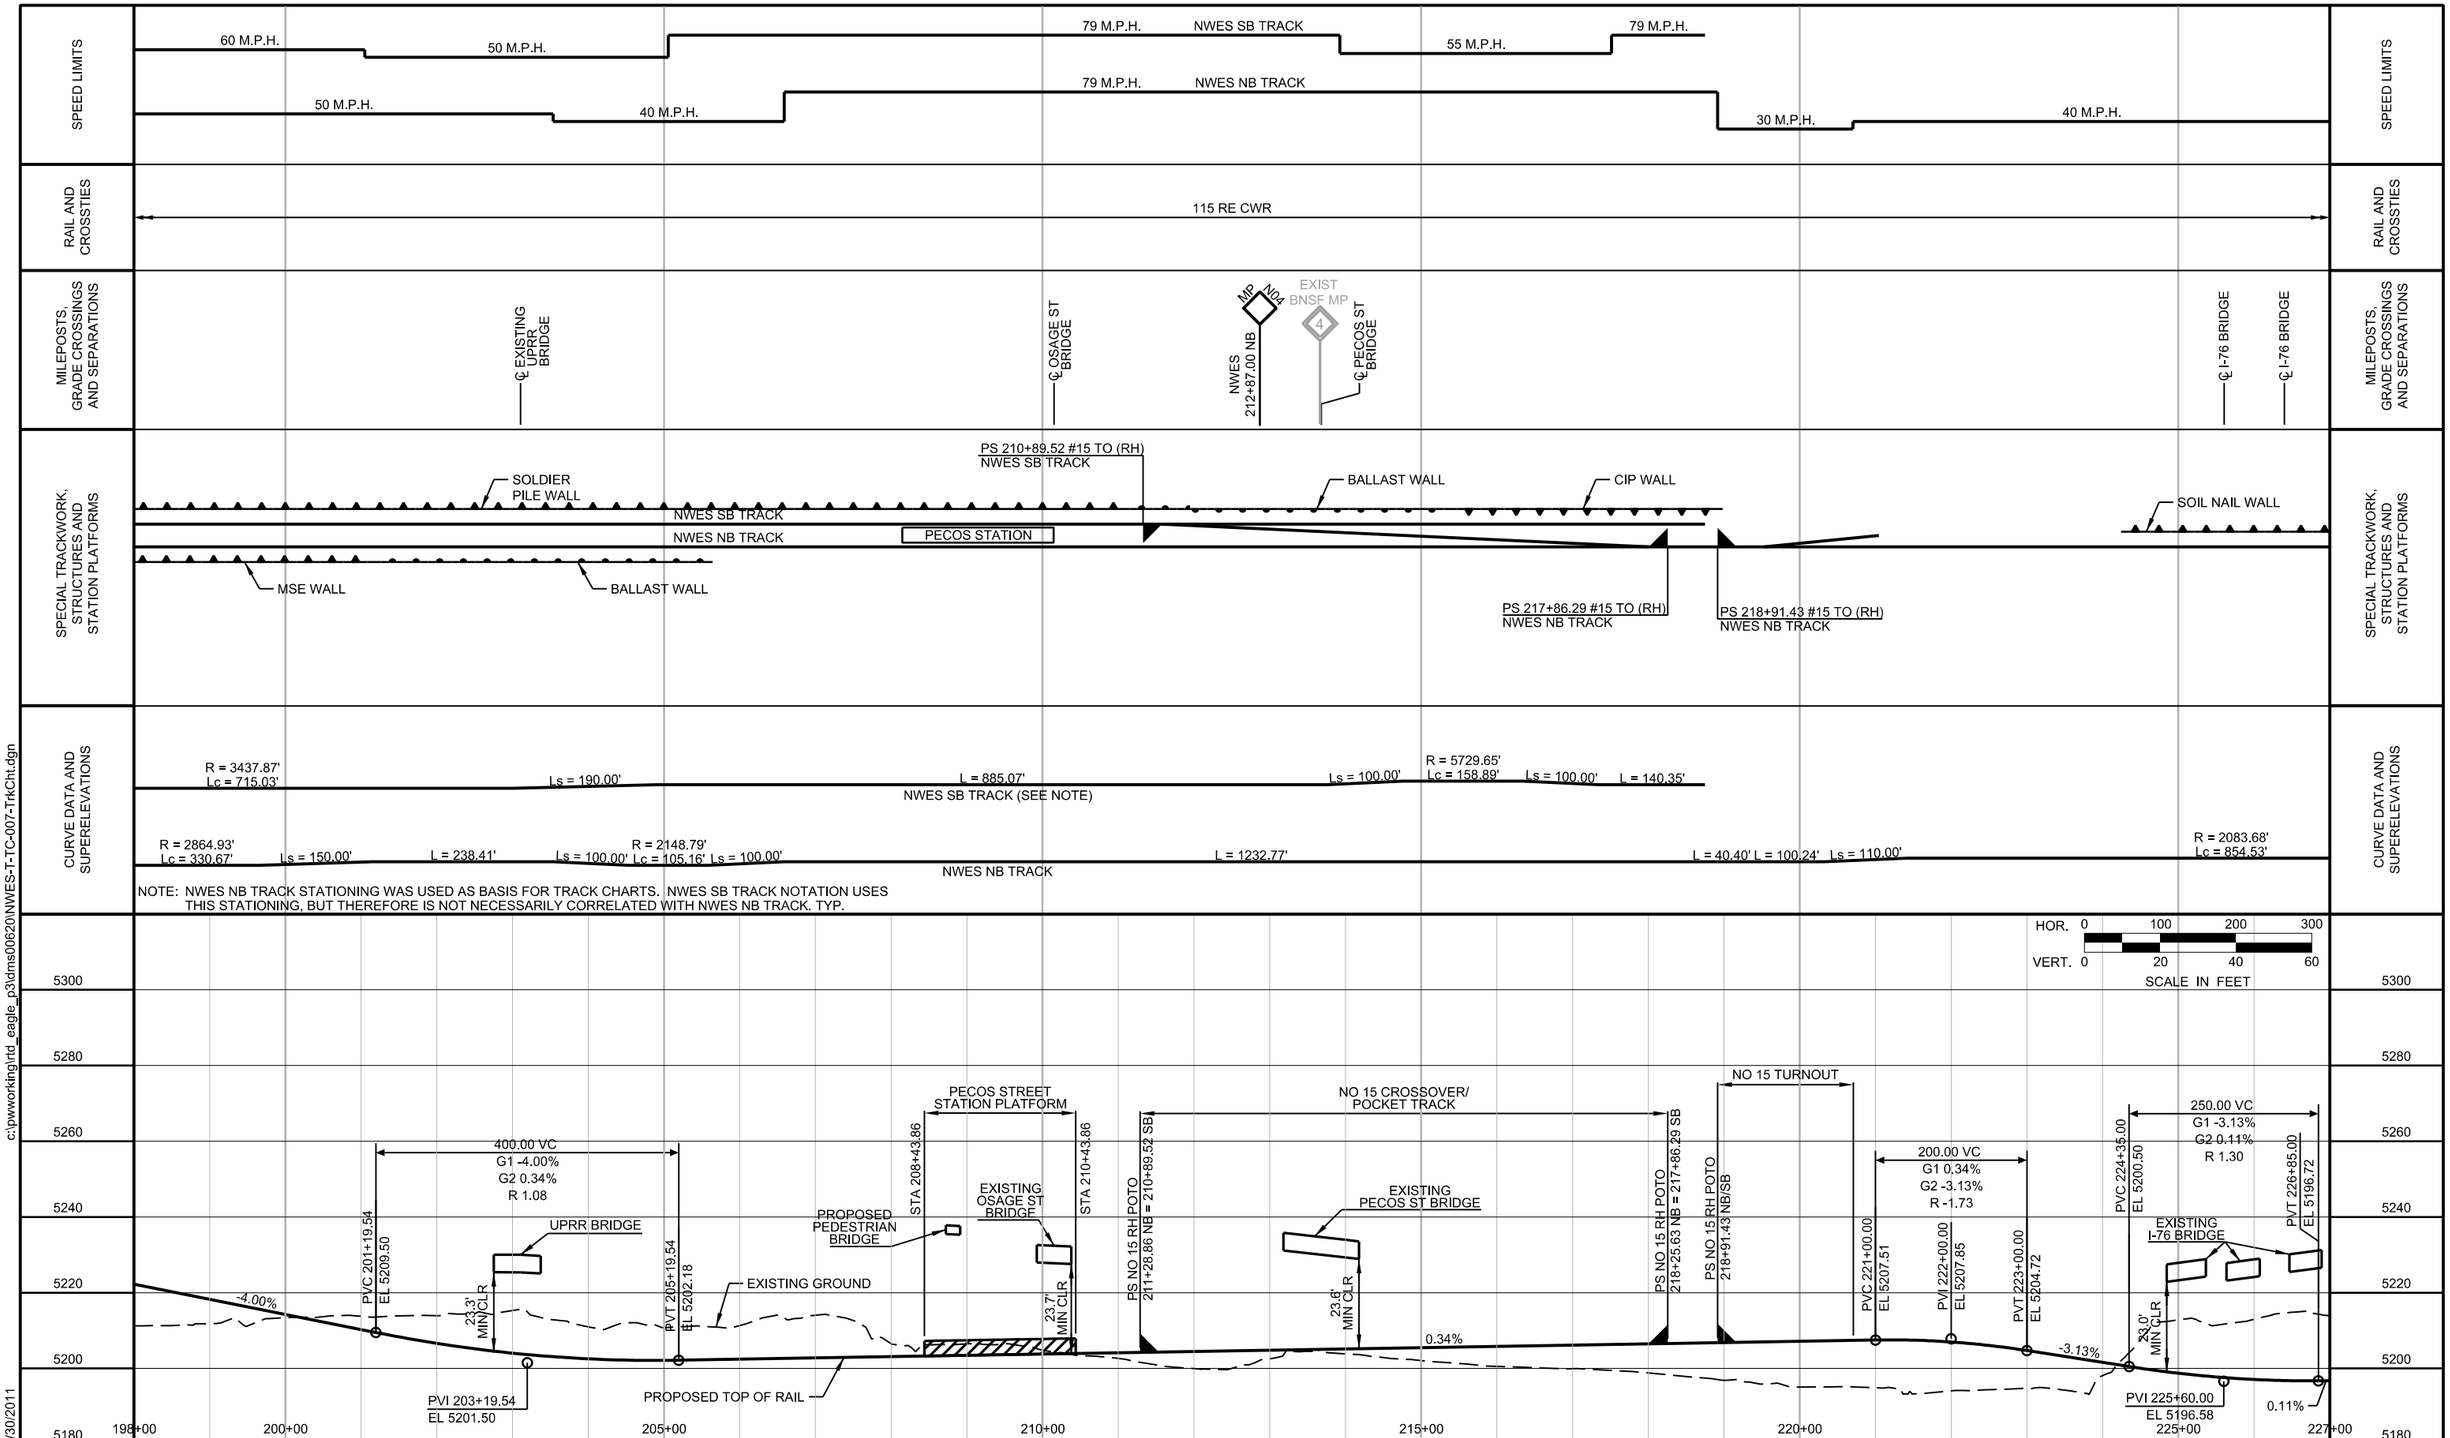

NO.	REVISIONS	BY	DATE
B	ISSUED FOR 60% SUBMITTAL, CDRL #7B-03.05, REV B	IMWC	06/22/11
A1	ISSUED FOR CONST REVIEW, CDRL #7B-03.05, REV A1	IMWC	05/27/11
A	ISSUED FOR PRE 60% PDRM, CDRL #7B-03.06, REV A	IMWC	05/03/11

DESIGNED BY: IMWC DATE: 02/28/11
DRAWN BY: DTO DATE: 02/28/11
CHECKED BY: DATE:
APPROVED BY: DATE:

RTD FASTRACKS eagle P3 FLUOR HDR GLOBAL DESIGN CONSULTANTS ATKINS DENVER TRANSIT PARTNERS

NORTHWEST RAIL ELECTRIFIED SEGMENT

TRACK CHARTS
STA 198+00 TO STA 227+00

SHEET REFERENCE NUMBER: TC-007

c:\pwworking\rtd_eagle_p3\dms00620\NWES-T-TC-007-TrkCht.dgn
6/30/2011
USER: icrowe

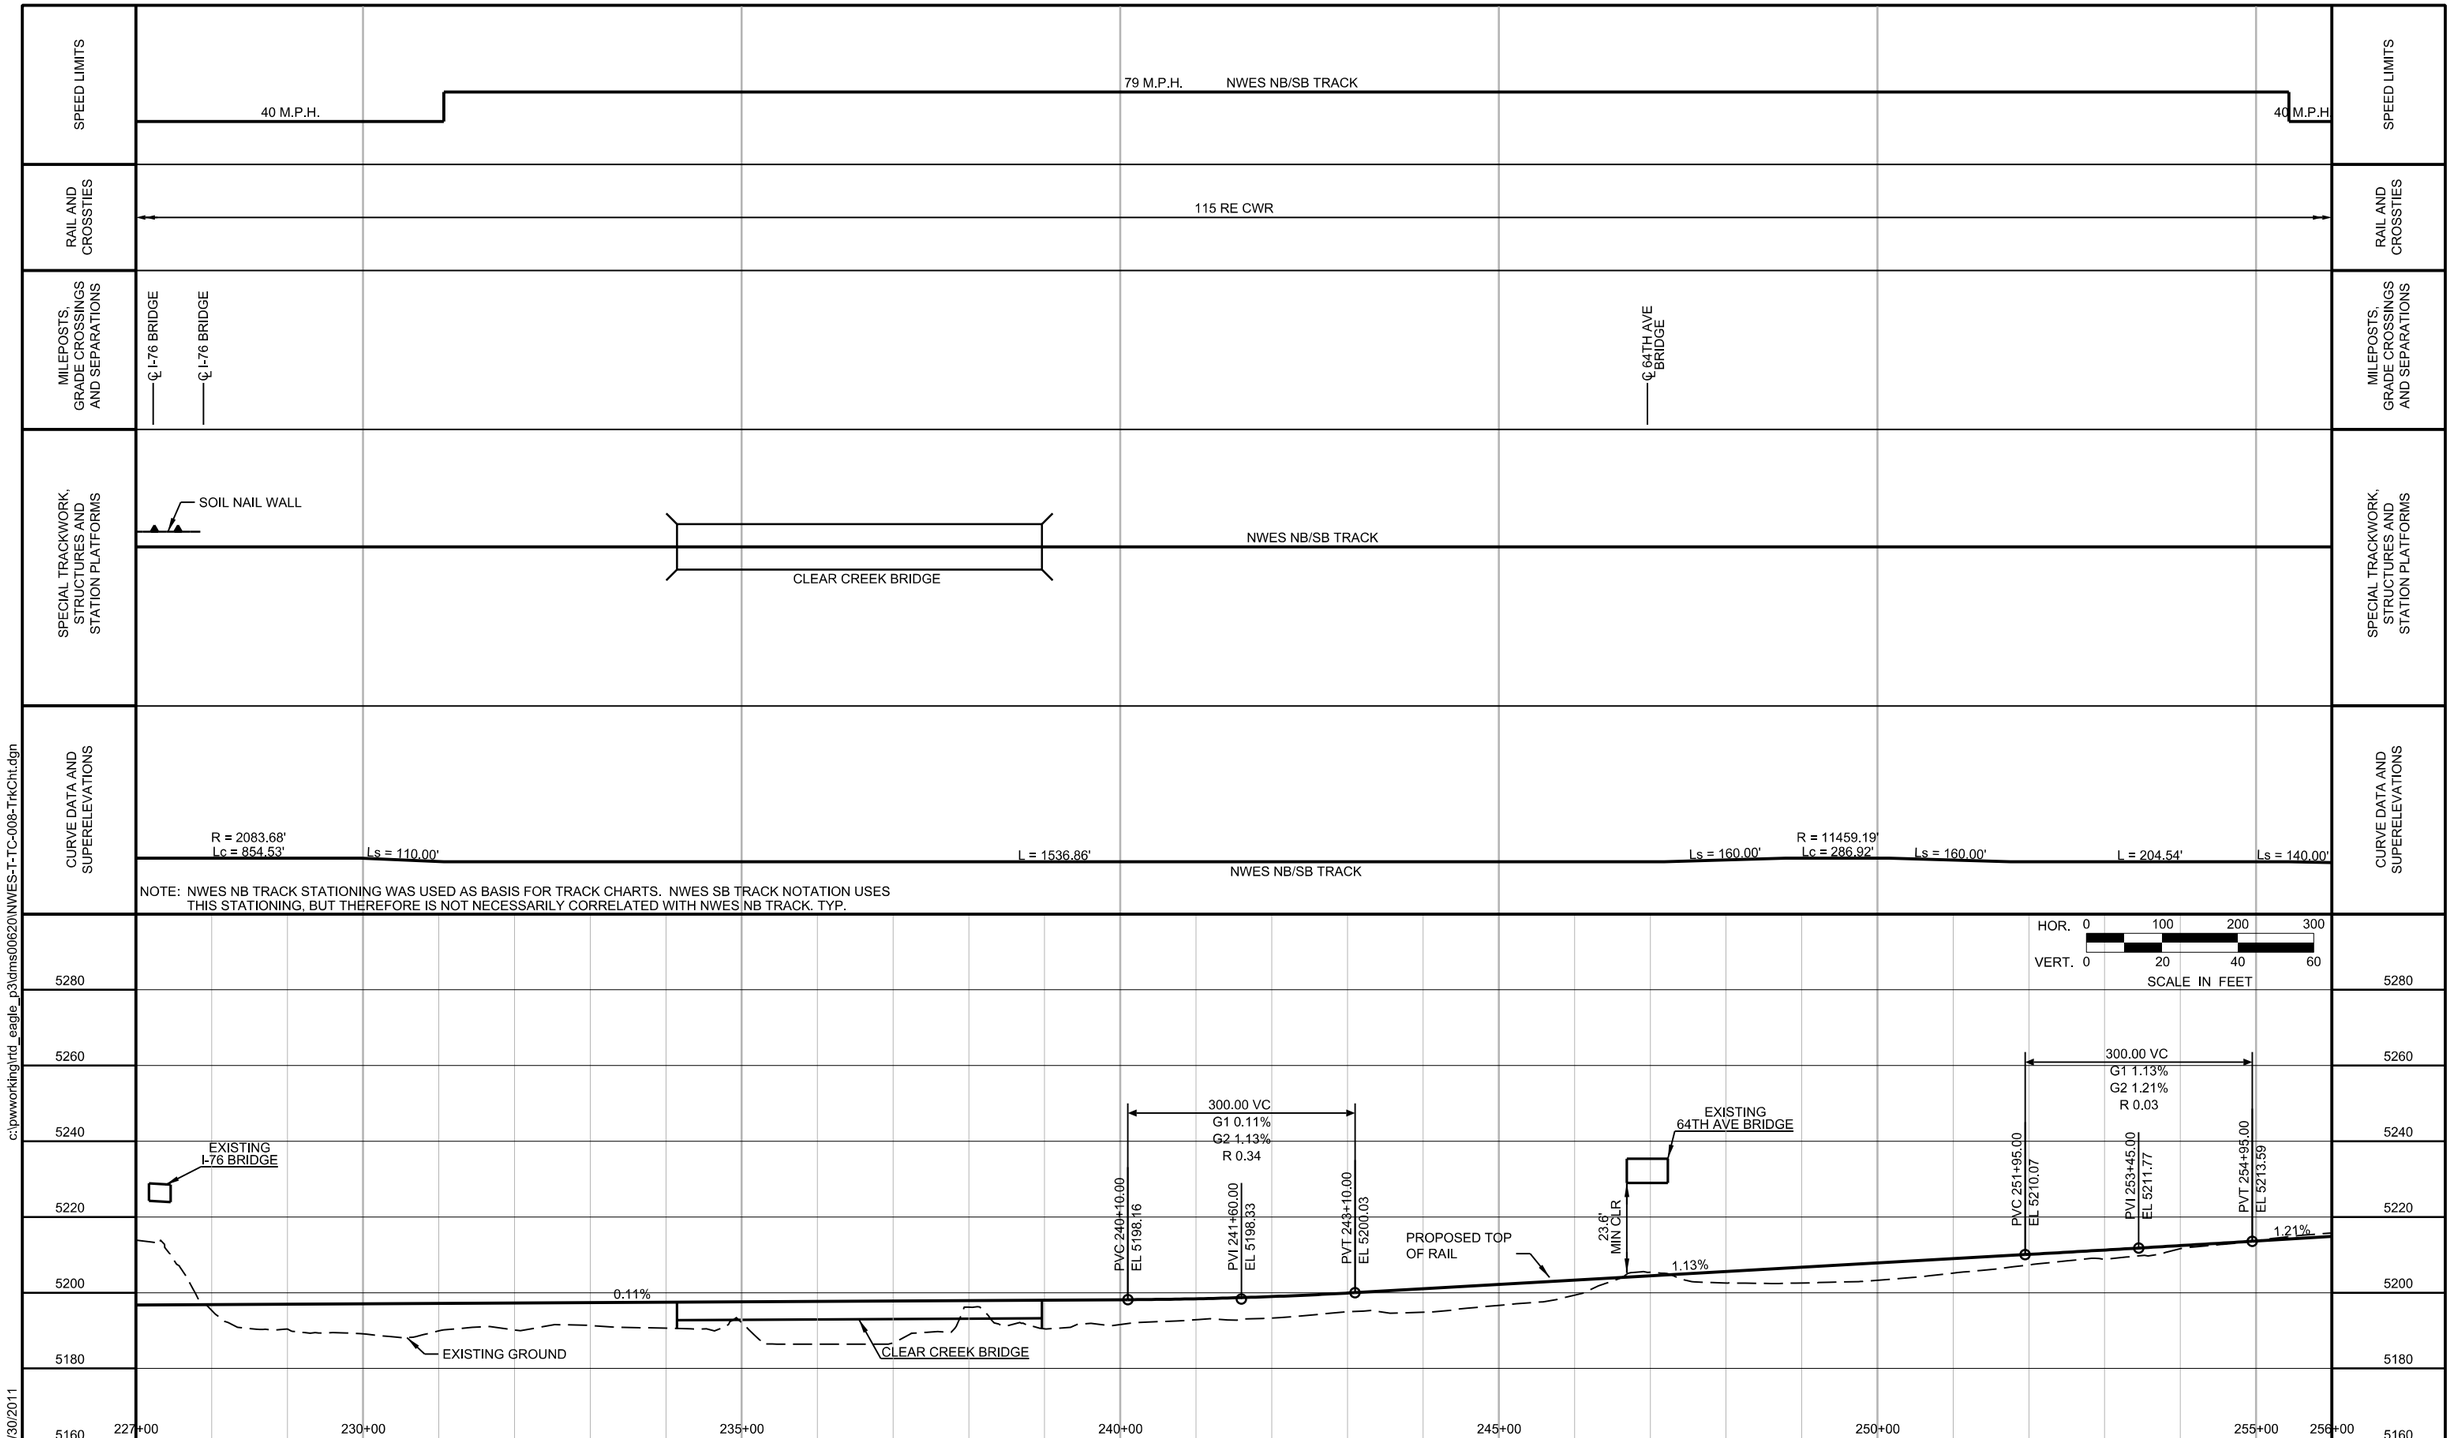

NO.	REVISIONS	BY	DATE
B	ISSUED FOR 60% SUBMITTAL, CDRL #7B-03.05, REV B	IMWC	06/22/11
A1	ISSUED FOR CONST REVIEW, CDRL #7B-03.05, REV A1	IMWC	05/27/11
A	ISSUED FOR PRE 60% PDRM, CDRL #7B-03.06, REV A	IMWC	05/03/11

DESIGNED BY: IMWC DATE: 02/28/11
DRAWN BY: DTO DATE: 02/28/11
CHECKED BY: DATE:
APPROVED BY: DATE:

RTD FASTRACKS eagle P3 FLUOR HDR GLOBAL DESIGN CONSULTANTS ATKINS DENVER TRANSIT PARTNERS

NORTHWEST RAIL ELECTRIFIED SEGMENT

TRACK CHARTS
STA 227+00 TO STA 256+00

SHEET REFERENCE NUMBER: TC-008

c:\pwworking\rtd_eagle_p3\dms00620\NWES-T-TC-008-TrkCht.dgn
6/30/2011
USER: icrowe

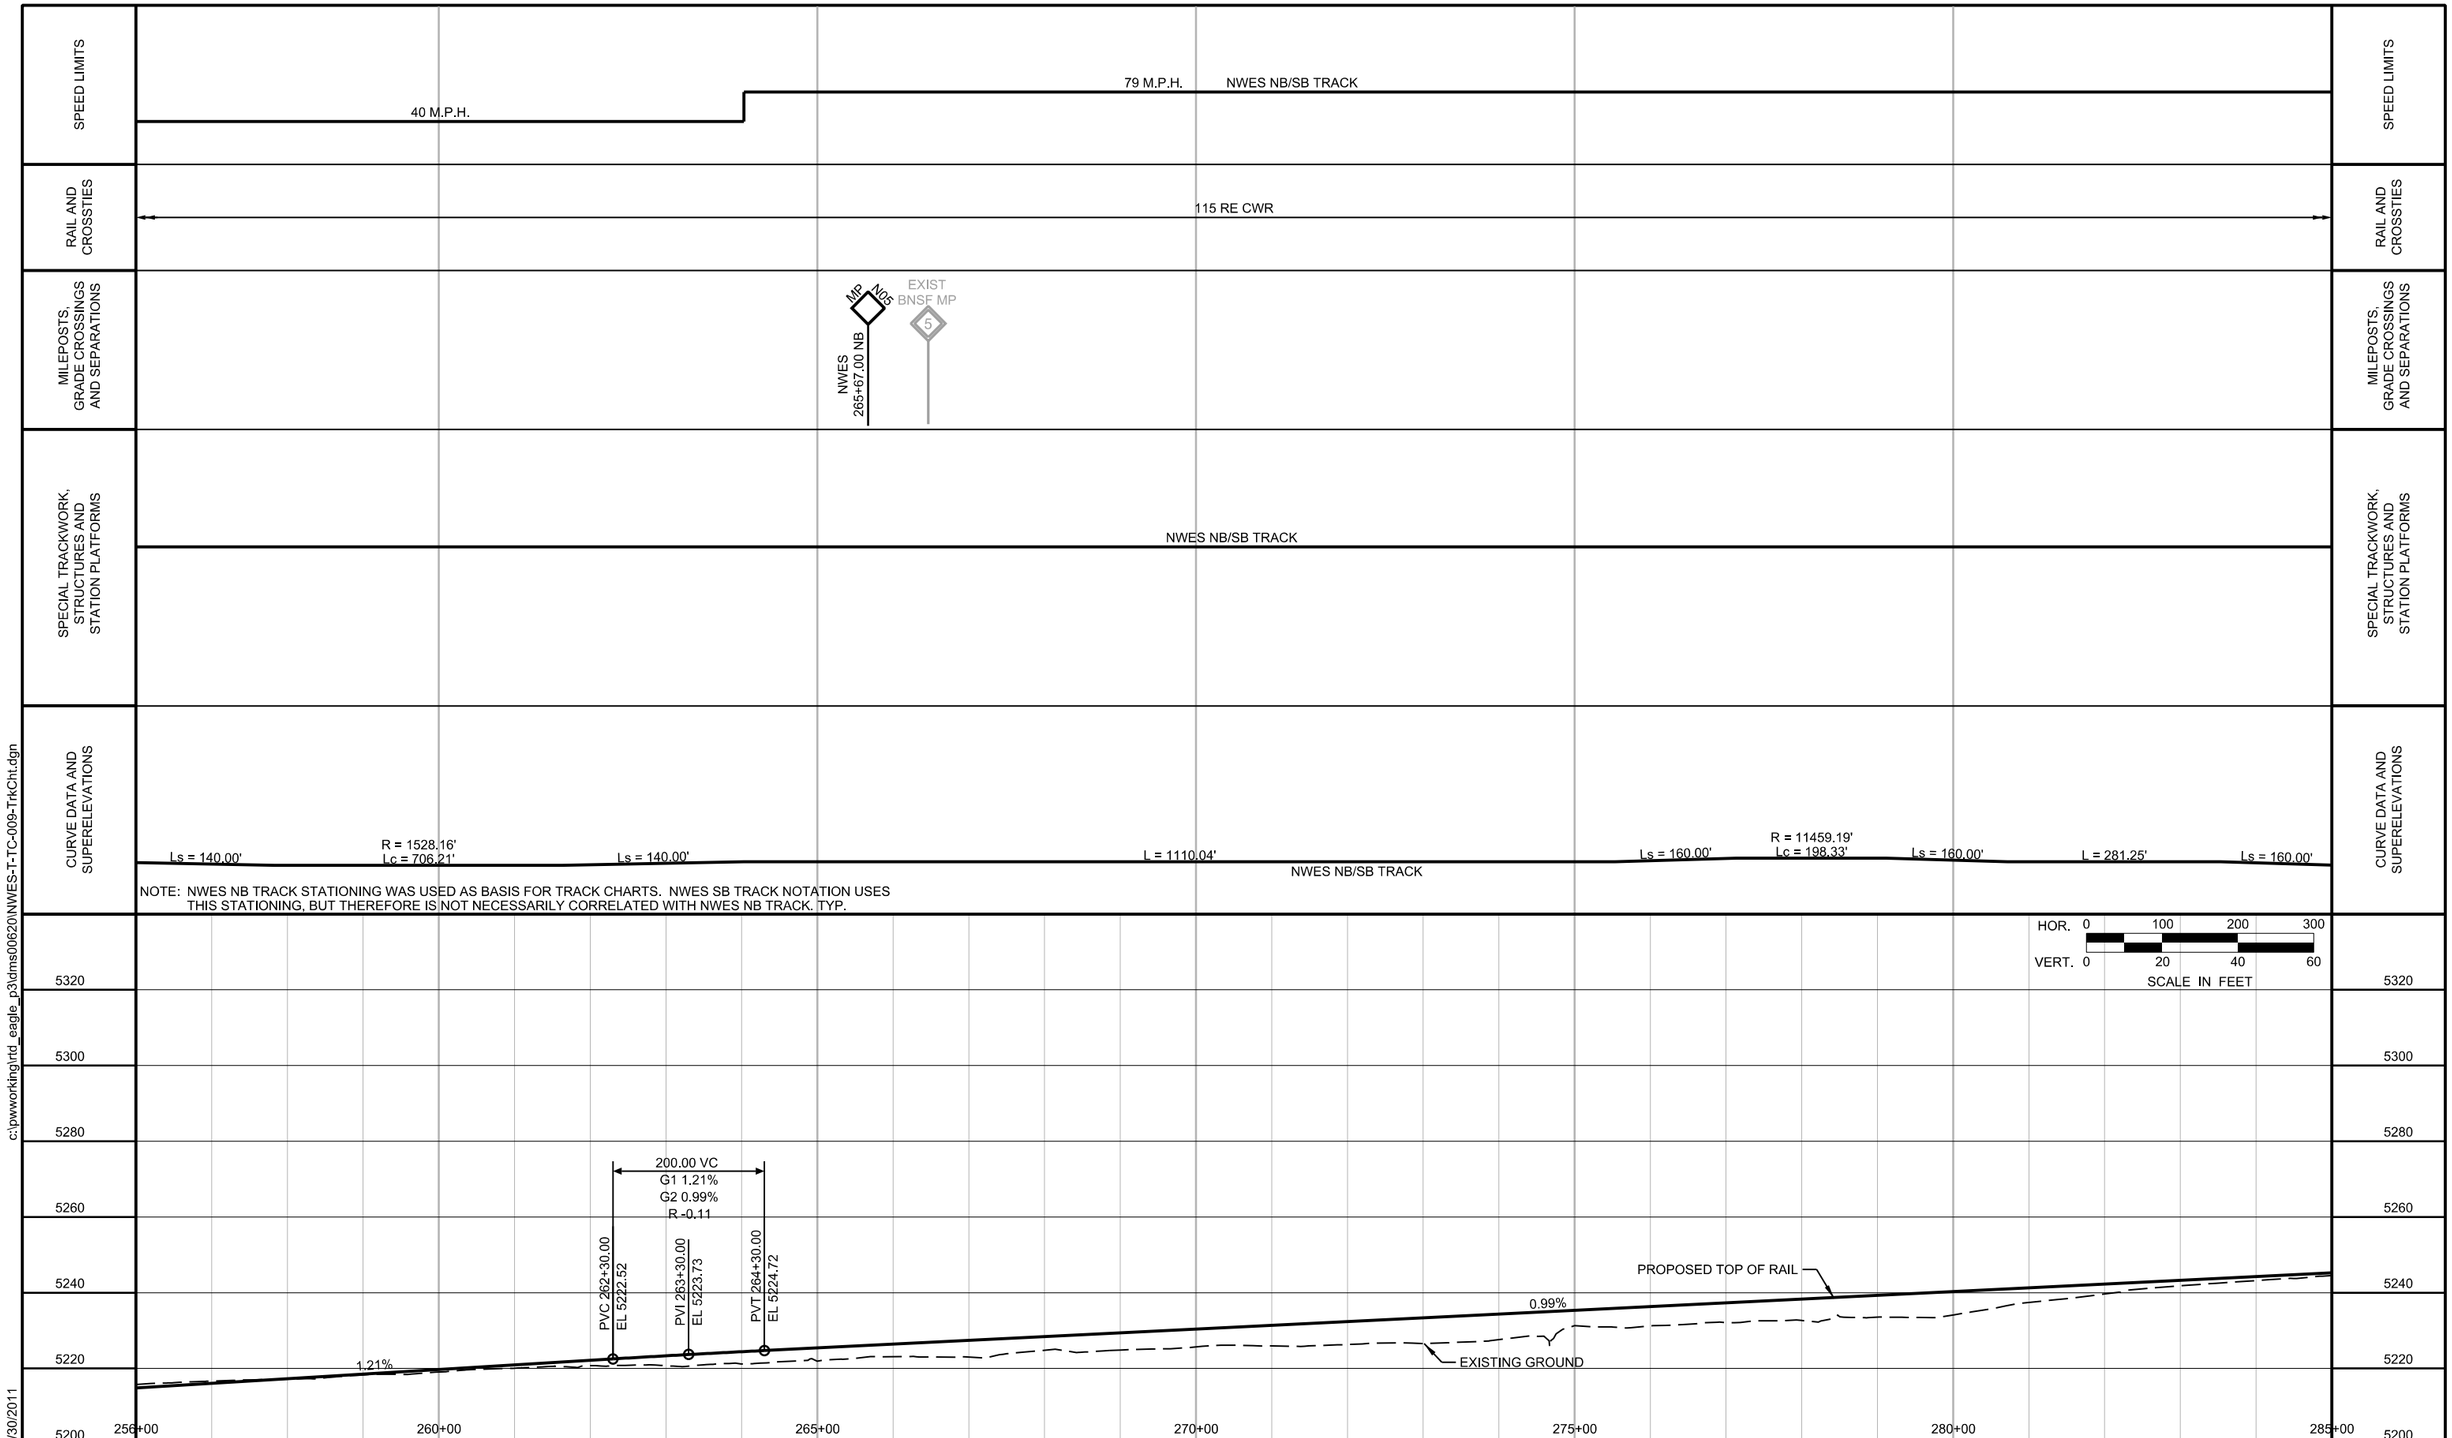

NO.	REVISIONS	BY	DATE
B	ISSUED FOR 60% SUBMITTAL, CDRL #7B-03.05, REV B	IMWC	06/22/11
A1	ISSUED FOR CONST REVIEW, CDRL #7B-03.05, REV A1	IMWC	05/27/11
A	ISSUED FOR PRE 60% PDRM, CDRL #7B-03.05, REV A	IMWC	05/03/11

DESIGNED BY: IMWC DATE: 02/28/11
DRAWN BY: DTO DATE: 02/28/11
CHECKED BY: DATE:
APPROVED BY: DATE:

RTD FASTRACKS eagle P3 FLUOR HDR GLOBAL DESIGN CONSULTANTS ATKINS DENVER TRANSIT PARTNERS

NORTHWEST RAIL ELECTRIFIED SEGMENT

TRACK CHARTS
STA 256+00 TO STA 285+00

SHEET REFERENCE NUMBER: TC-009

c:\pwworking\rtd_eagle_p3\dms00620\NWES-T-TC-009-TrkCht.dgn
6/30/2011
USER: icrowe

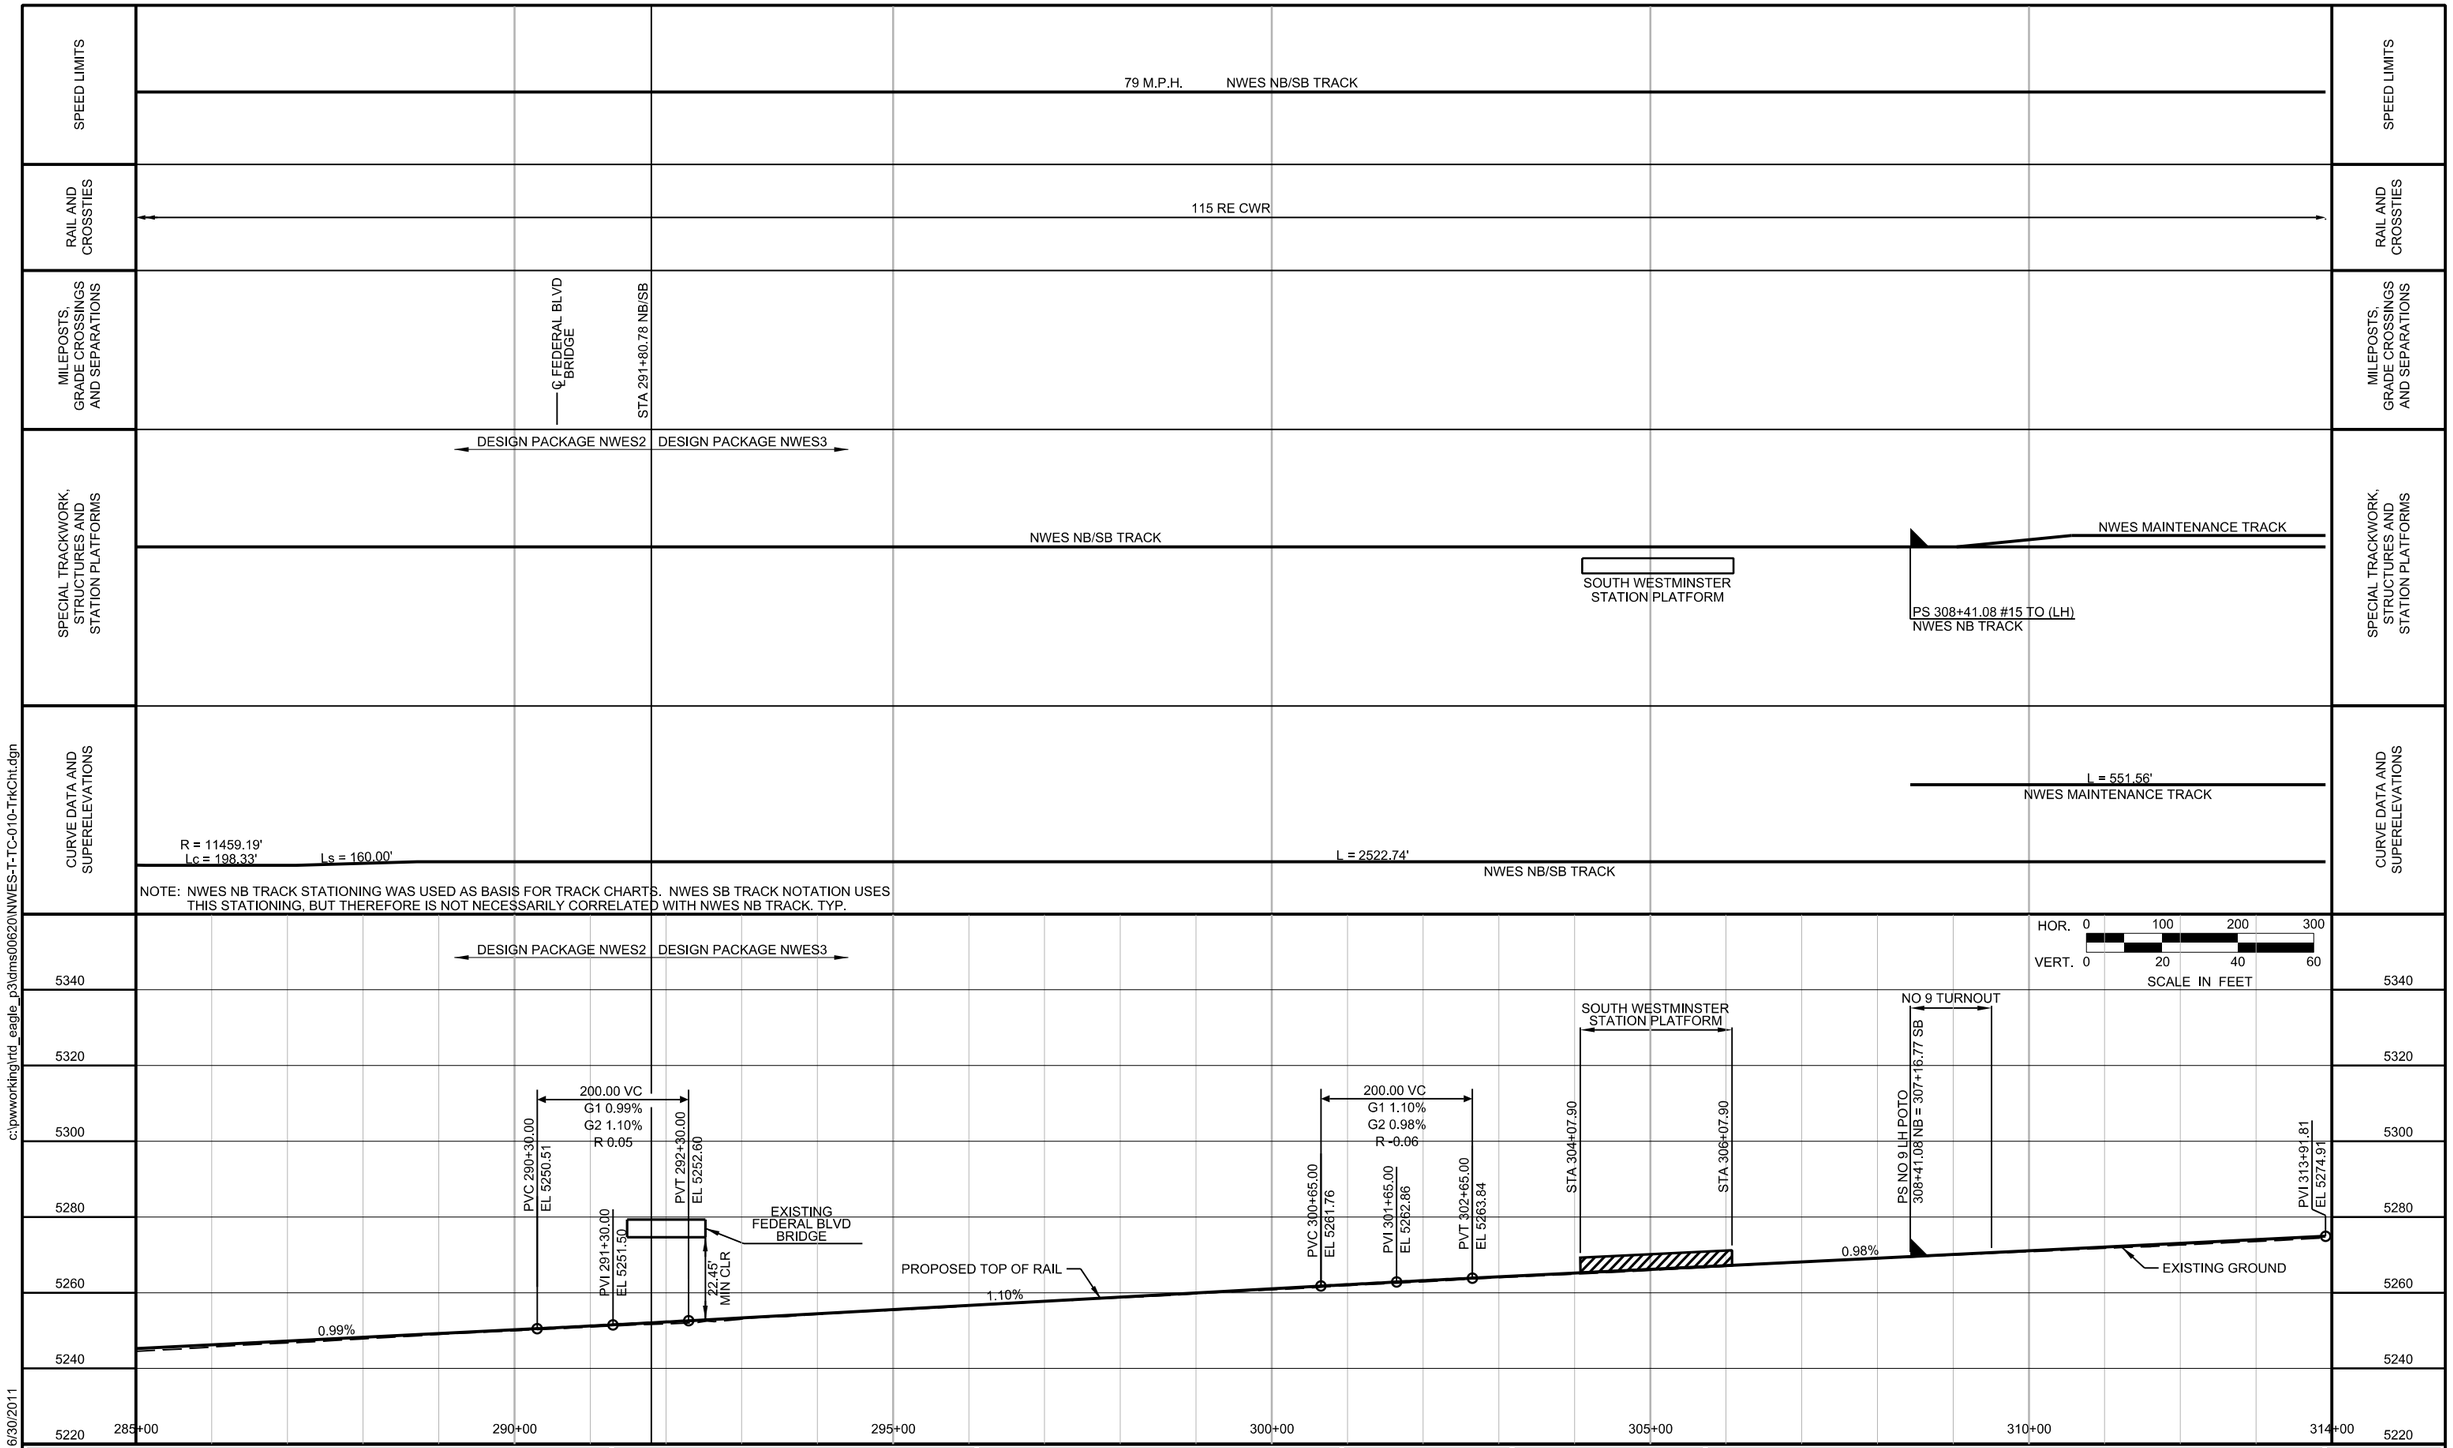

NO.	REVISIONS	BY	DATE
B	ISSUED FOR 60% SUBMITTAL, CDRL #7B-03.06, REV B	IMWC	06/22/11
A1	ISSUED FOR CONST REVIEW, CDRL #7B-03.06, REV A1	IMWC	05/27/11
A	ISSUED FOR PRE 60% PDRM, CDRL #7B-03.06, REV A	IMWC	05/03/11

DESIGNED BY: IMWC DATE: 02/28/11
DRAWN BY: DTO DATE: 02/28/11
CHECKED BY: DATE:
APPROVED BY: DATE:

RTD FASTTRACKS eagle P3 FLUOR HDR GLOBAL DESIGN CONSULTANTS ATKINS DENVER TRANSIT PARTNERS

NORTHWEST RAIL ELECTRIFIED SEGMENT

TRACK CHARTS
STA 285+00 TO STA 314+00

SHEET REFERENCE NUMBER: TC-010

c:\pwworking\rtd_eagle_p3\dms00620\NWES-T-TC-010-TrkCht.dgn
6/30/2011
USER: icrowe