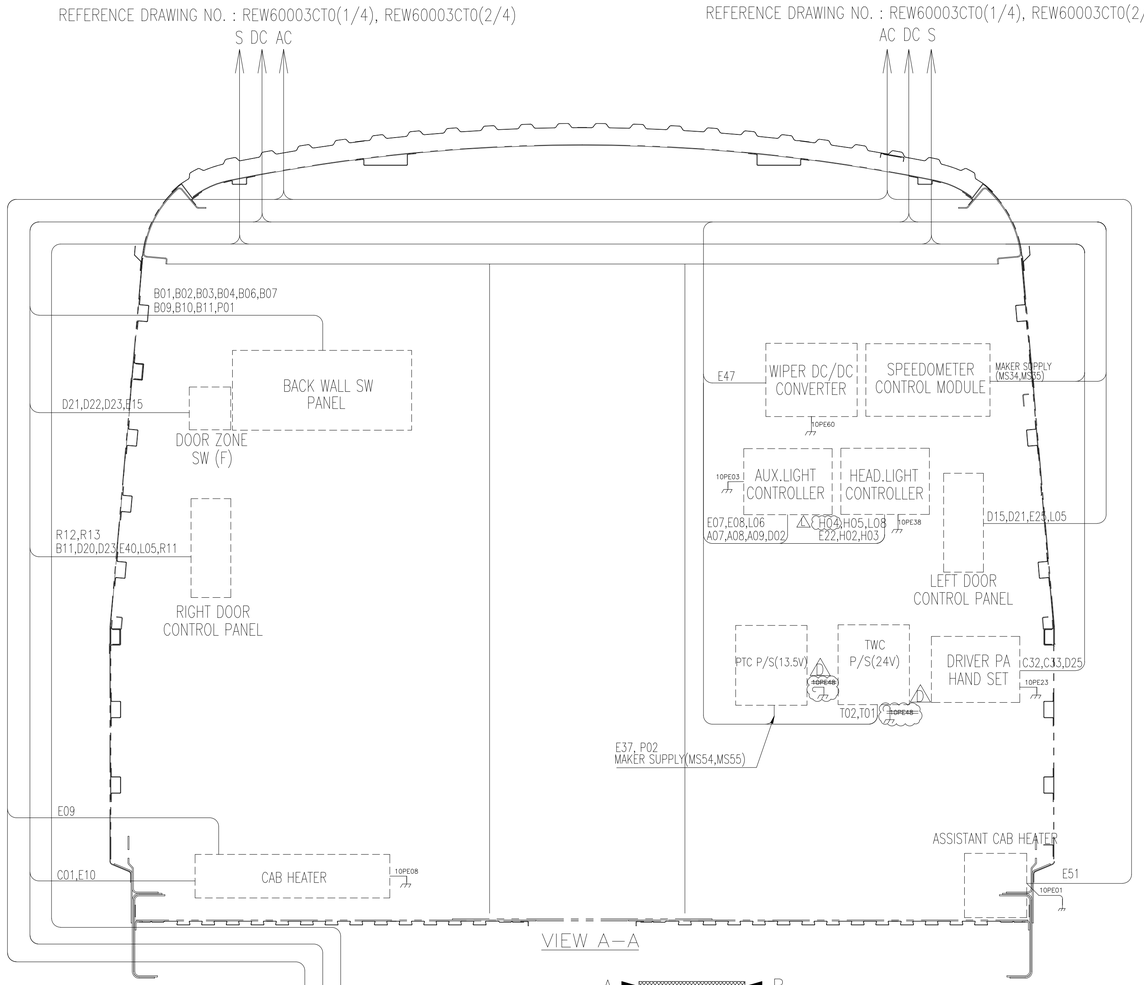

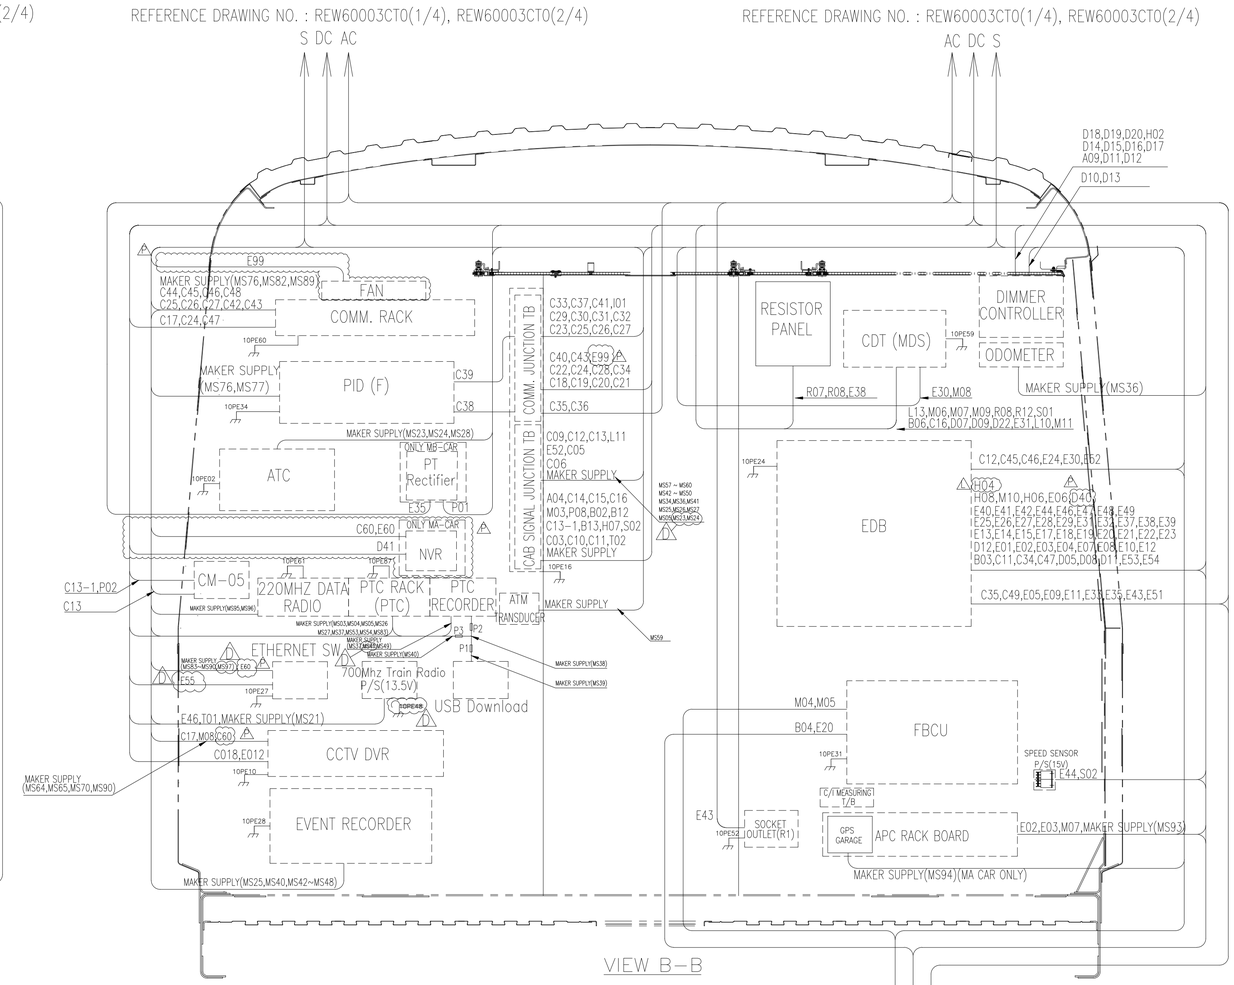

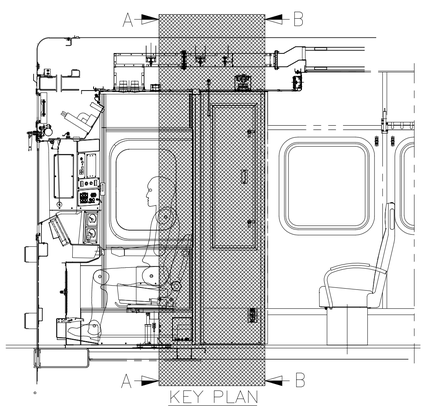

	DESCRIPTION
APC	AUTOMATIC PASSENGER COUNTING
ATC	AUTOMATIC TRAIN CONTROL
CDT	CENTRAL DIAGNOSTIC TERMINAL
C/I	CONVERTER INVERTER
EDB	ELECTRICAL DISTRIBUTION BOARD
FBCU	FRICTION BRAKE CONTROL UNIT
FDI	FRONT DESTINATION INDICATOR
FDP	FAULT DISPLAY PANEL
MDS	MONITORING DIAGNOSTIC SYSTEM
PID	PASSENGER INFORMATION DISPLAY
PT	POTENTIAL TRANSFORMER
PTC	POSITIVE TRAIN CONTROL

등급 GRADE		A	B	C
주물,주강품 CASTING (±)				
~ 20M		8	14	24
~ 15M		7	12	21
~ 12M		6	10	18
~ 8M		5	8	14
~ 4M		4	6	11
~ 2M		3	4	8
~ 1M		2	3	6
~ 315		1	2	4
~ 120		1	2	3
~ 30		1	1	1
등급 GRADE		A	B	C
용접 구조물 WELDING (±)				
~ 20M	–	6.0	8.0	
~ 15M	–	5.0	7.0	
~ 12M	–	4.0	6.0	
~ 8M	–	3.0	5.0	
~ 4M	0.8	2.0	4.0	
~ 2M	0.5	1.2	3.0	
~ 1M	0.3	0.8	2.0	
~ 315	0.2	0.5	1.2	
~ 120	0.15	0.3	0.8	
~ 30	0.1	0.2	0.5	
3 ~ 6	0.05	0.1	0.2	
등급 GRADE	A	B	C	
기계 가공품 MACHINING (±)				
규정치않은 일반공차로 GENERAL TOLERANCE				

기호 MARK	일자 DATE	변경내역 DETAIL OF REVISION(E.C ZONE)	설변번호 E.C NO.	설계 DGN	검도 CHK	승인 APP
x5	2018.01.11	ADDED FAN,NVR & SYMBOL "C60,D40,D41,E60,E99"	RNE1002-U529	BJHWANG	M.S.KIM	H.G.RYU
x0	2016.01.07	NOT REVISED	RNE1002-U523	BJHWANG	M.S.KIM	H.G.RYU
x0	2015.04.02	NOT REVISED	RNE1002-U483	BJHWANG	C.H.CHOI	S.H.JEON
x2	2014.10.23	ADDED WIRE SYMBOL "H04"	RNE1002-U467	J.H.KIM	H.S.PARK	D.I.KIM
x0	2014.03.18	NOT REVISED	RNE1002-U405	J.H.KIM	H.S.PARK	D.I.KIM
x8	2012.12.26	UPDATED CABLE SYMBOL 'E55' & MS CABLE SYMBOL ERASED EARTH CABLE OF 13.6VDC POWER SUPPLY	RNE1002-U249	J.H.KIM	H.S.PARK	D.I.KIM
x27	2012.10.12	ADDED EARTH CABLE SYMBOL & ADDED SYMBOL "E06,S02"	RNE1002-U199	J.H.KIM	H.S.PARK	D.I.KIM
x6	2012.10.12	CHANGED WIRING INFORMATION	RNE1002-U180	J.H.KIM	H.S.PARK	D.I.KIM
x16	2012.08.23	CHANGED WIRING INFORMATION	RNE1002-U157	J.H.KIM	H.S.PARK	D.I.KIM

품번 NO.	부품 번호 PART NO.	품명 DESCRIPTION	재질 MATERIAL	수량 QTY	중량 WT	비고 REMARKS
승인 APP	D.I.KIM 2012.05.28	재질 MAT'L N/A				
검도 CHK	H.S.PARK 2012.05.28	총중량 G.W N/A				
설계 DGN	J.H.KIM 2012.05.28	일반공차 MC WD CT				
제도 DRG		SIZE D				

참고번호 REF. NO.

명칭 TITLE: WIRING DIAGRAM, CAB, F-END,MA, MB (3/5)

도면 번호 DRG. NO: MS REW60003CT0 Ver. 00 Rev. -P RNE1002

SCALE | 매수 SHEET 3 of 5

HYUNDAI Rotem 현대로템주식회사

년-PRJT | 정리번호

본 도면은 당사 재산으로서 허가없이 무단복사/배포 금지됨. PROPERTY OF ISSUING ENTITY. CANNOT BE DISTRIBUTED OR REPRODUCED WITHOUT AUTHORIZATION.

AutoCAD